





QR validacion

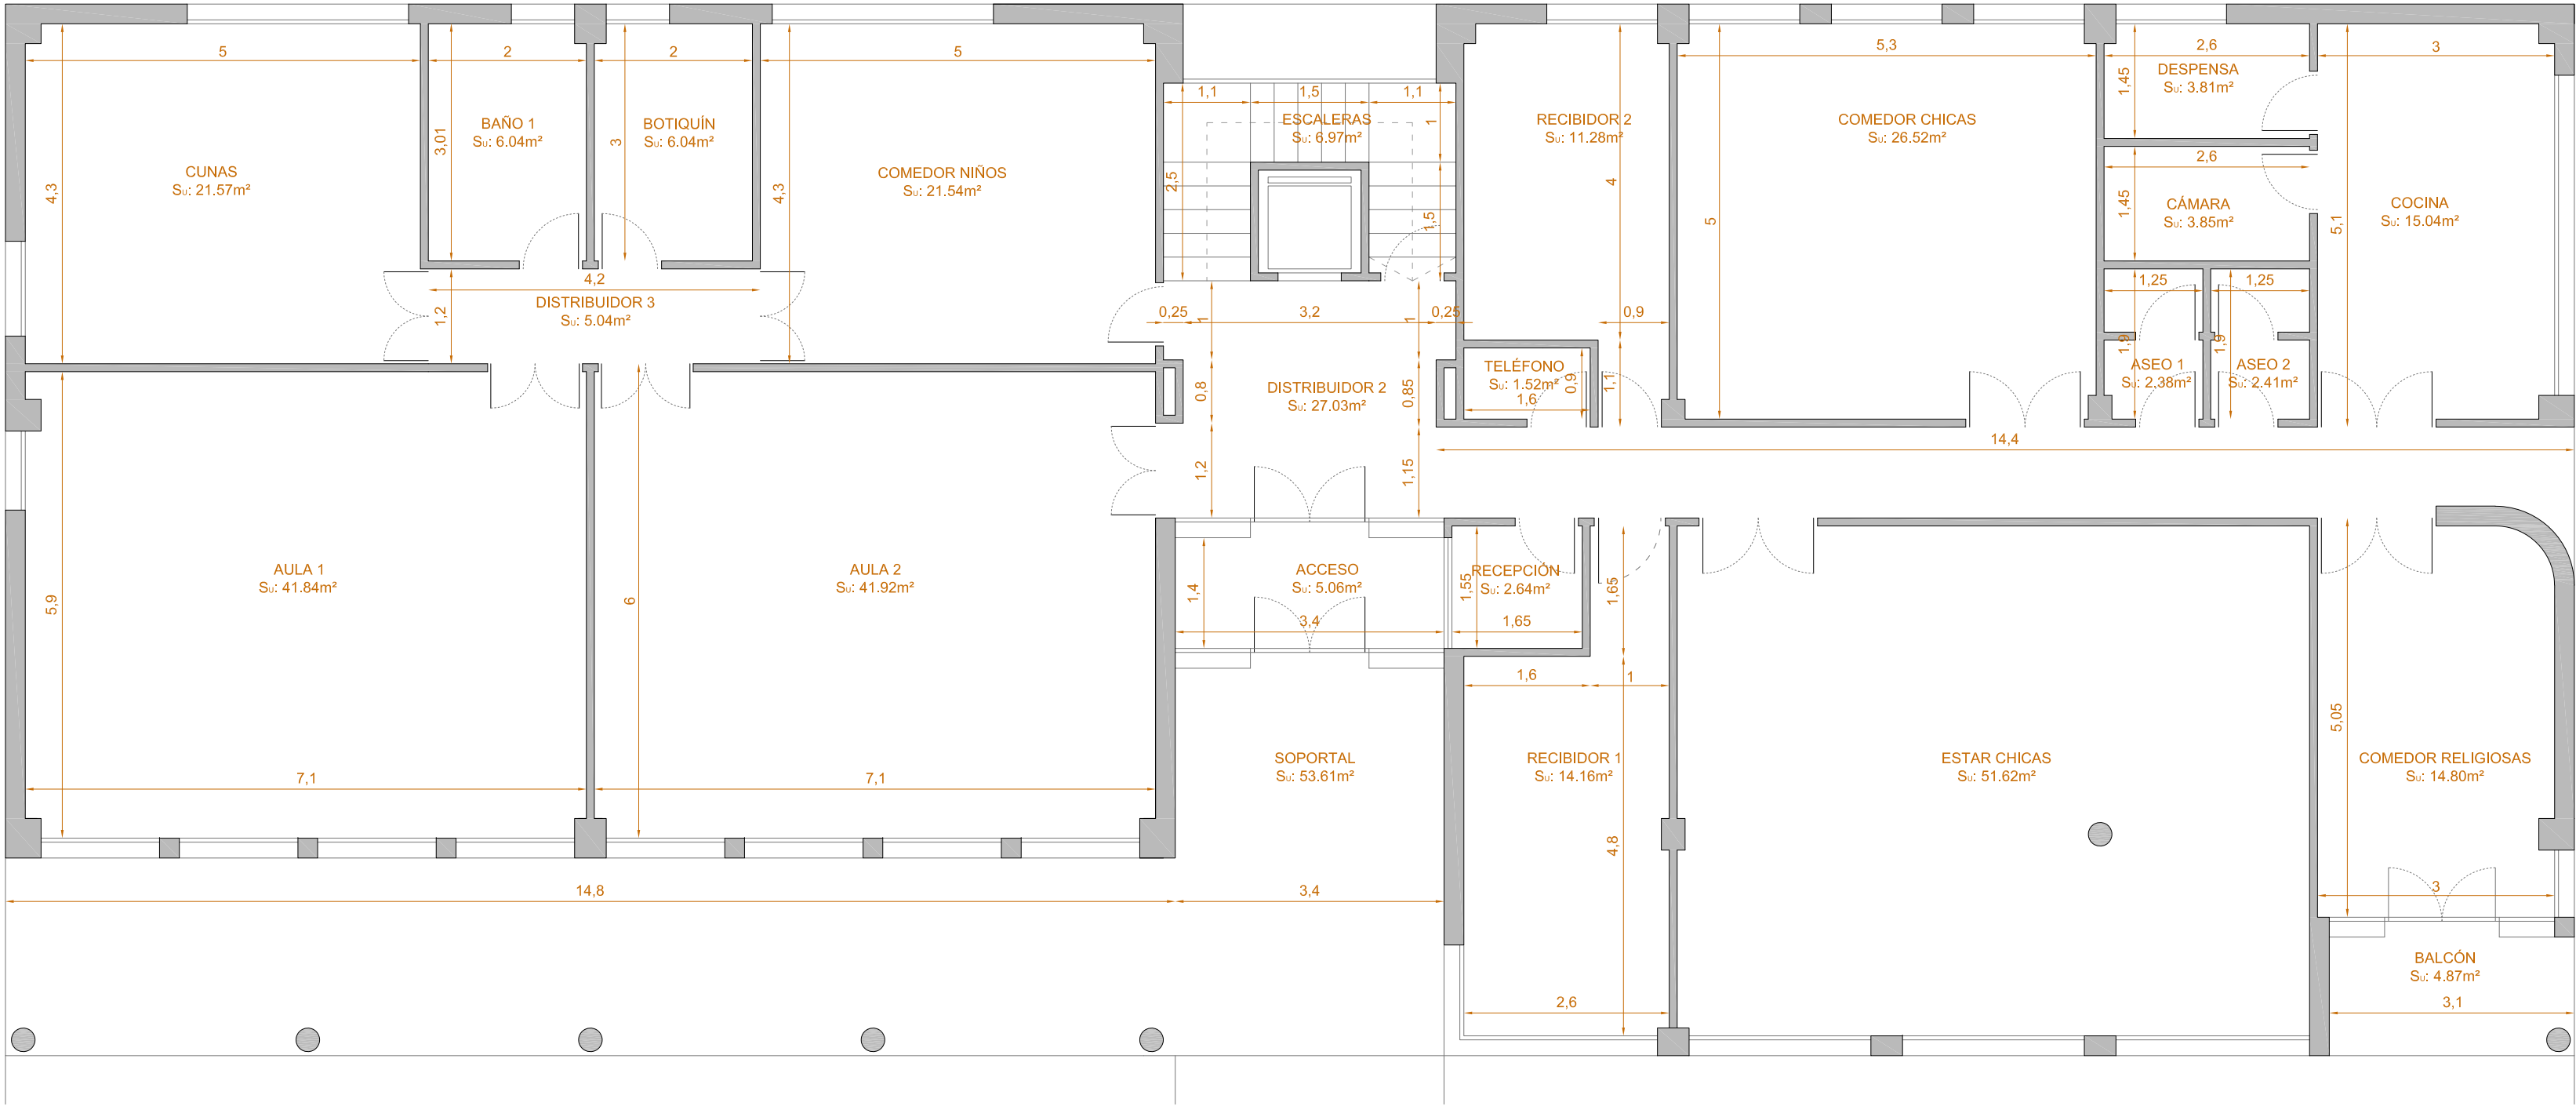

PLANTA BAJA

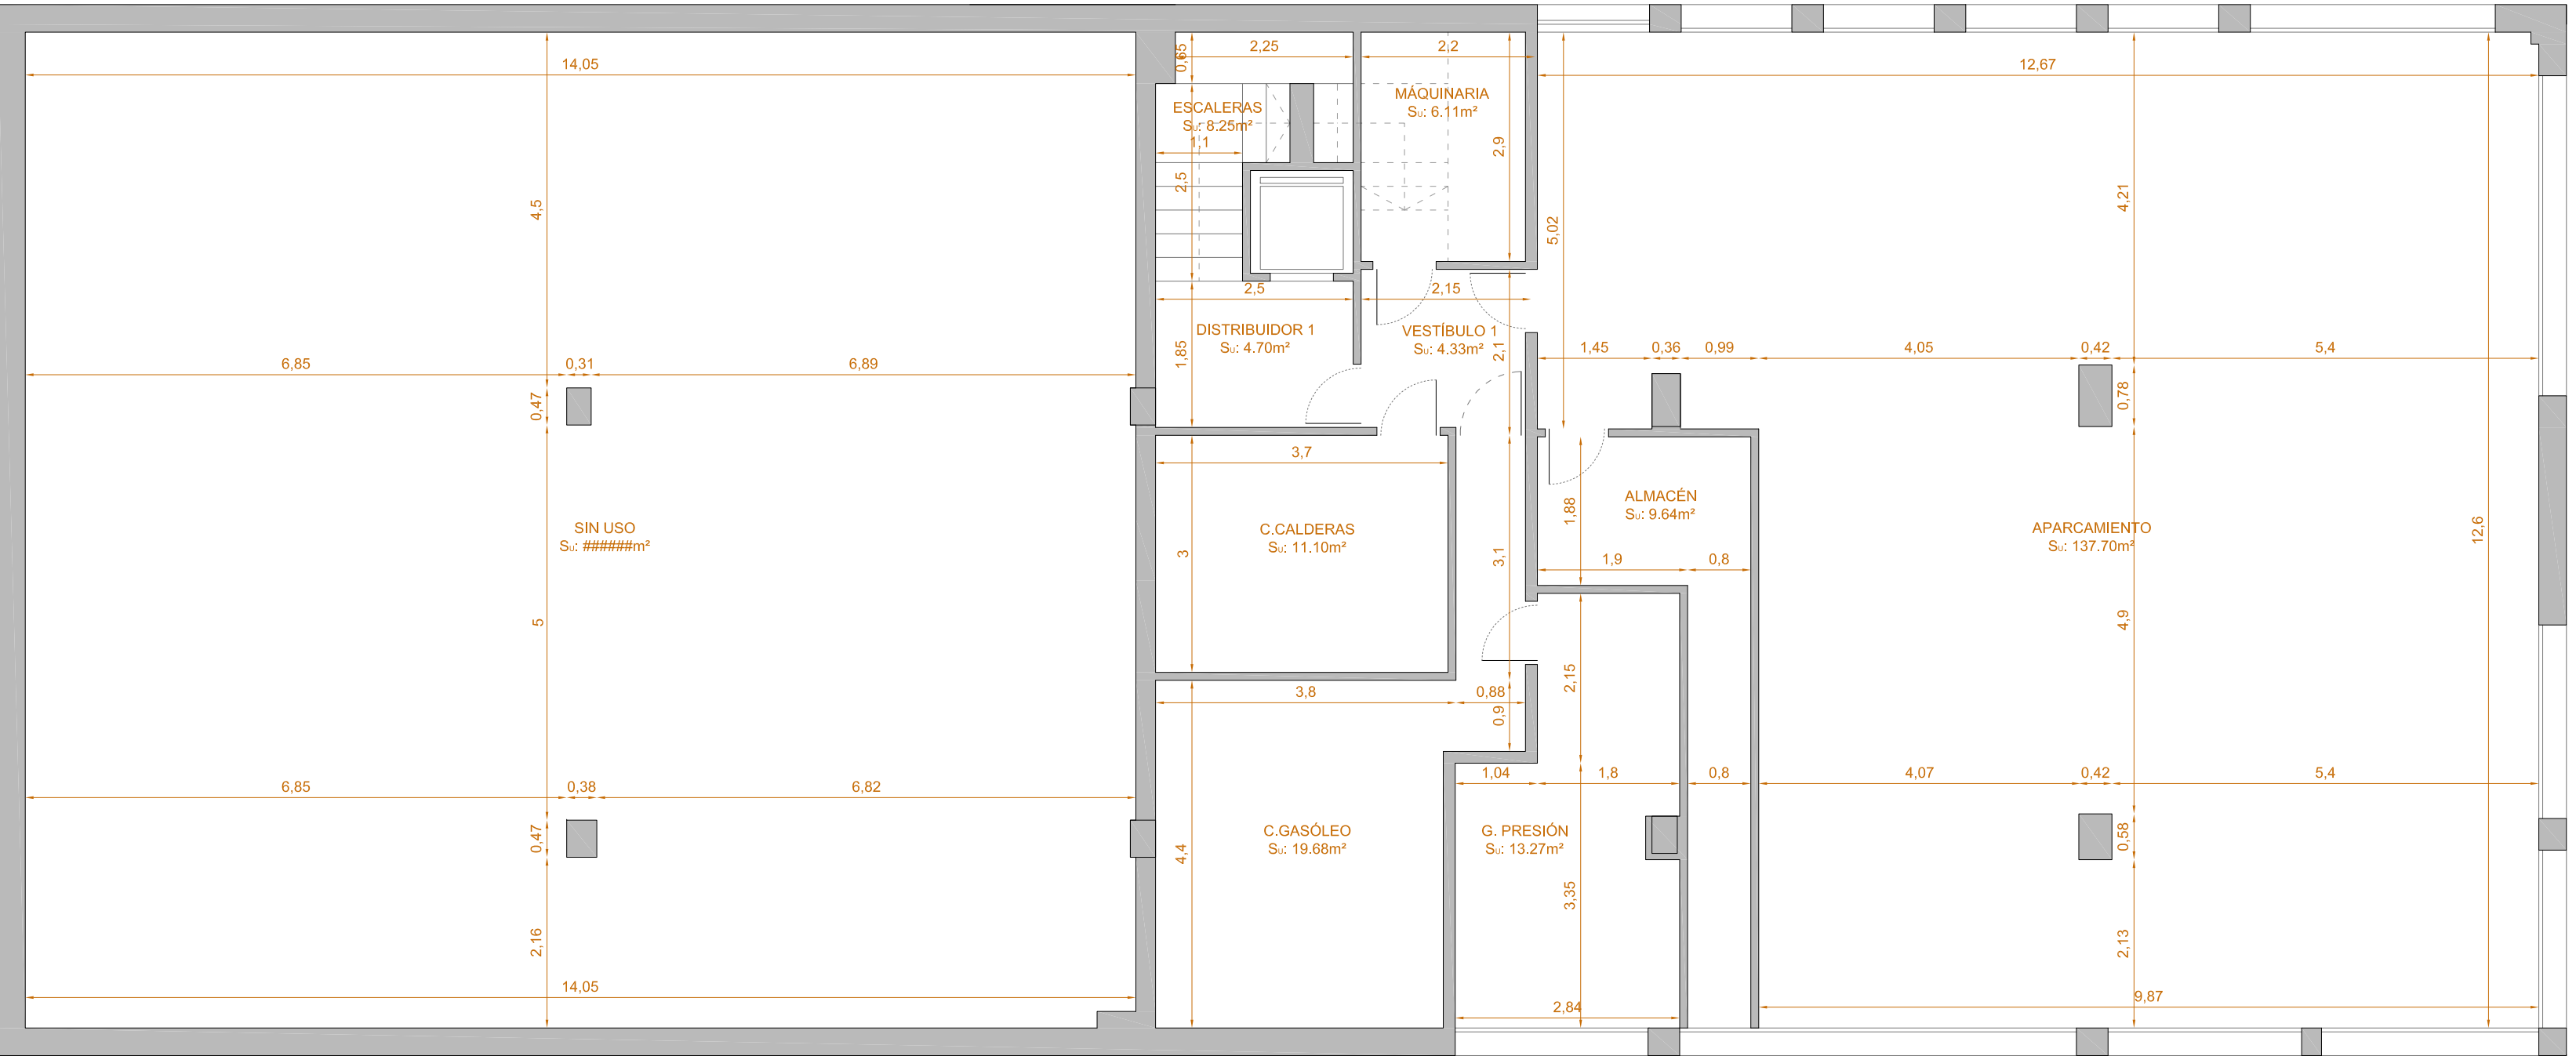

PLANTA SÓTANO



APUNTOARQUITECTURA
teléfono: 649612449
www.apuntoarquitectura.com
oficina@apuntoarquitectura.com

PROYECTO
PROYECTO BÁSICO DE OBRAS PARA EL CAMBIO DE
USO DE EDIFICIO RESIDENCIAL A TERCIARIO
HOSPEDAJE. LICENCIA DE ACTIVIDAD_
HOTEL DE 2 ESTRELLAS. Cl. Haro 5; 28043 Madrid
TITULAR
HARO 5 VENTURES S.L.
N.I.F.: B22599070
REPRESENTANTE
Rafael Garrido Rodrigo
D.N.I.: 00839470Q

TÉCNICO
Jorge Serrano de La Torre
COLEGIADO COAM 17.677

DESCRIPCIÓN
ARQUITECTURA ACTUAL: PLANTAS 1

NÚMERO DE PLANO FECHA ESCALA


A01 17.04.2026 1:75



QR validation



PLANTA PRIMERA

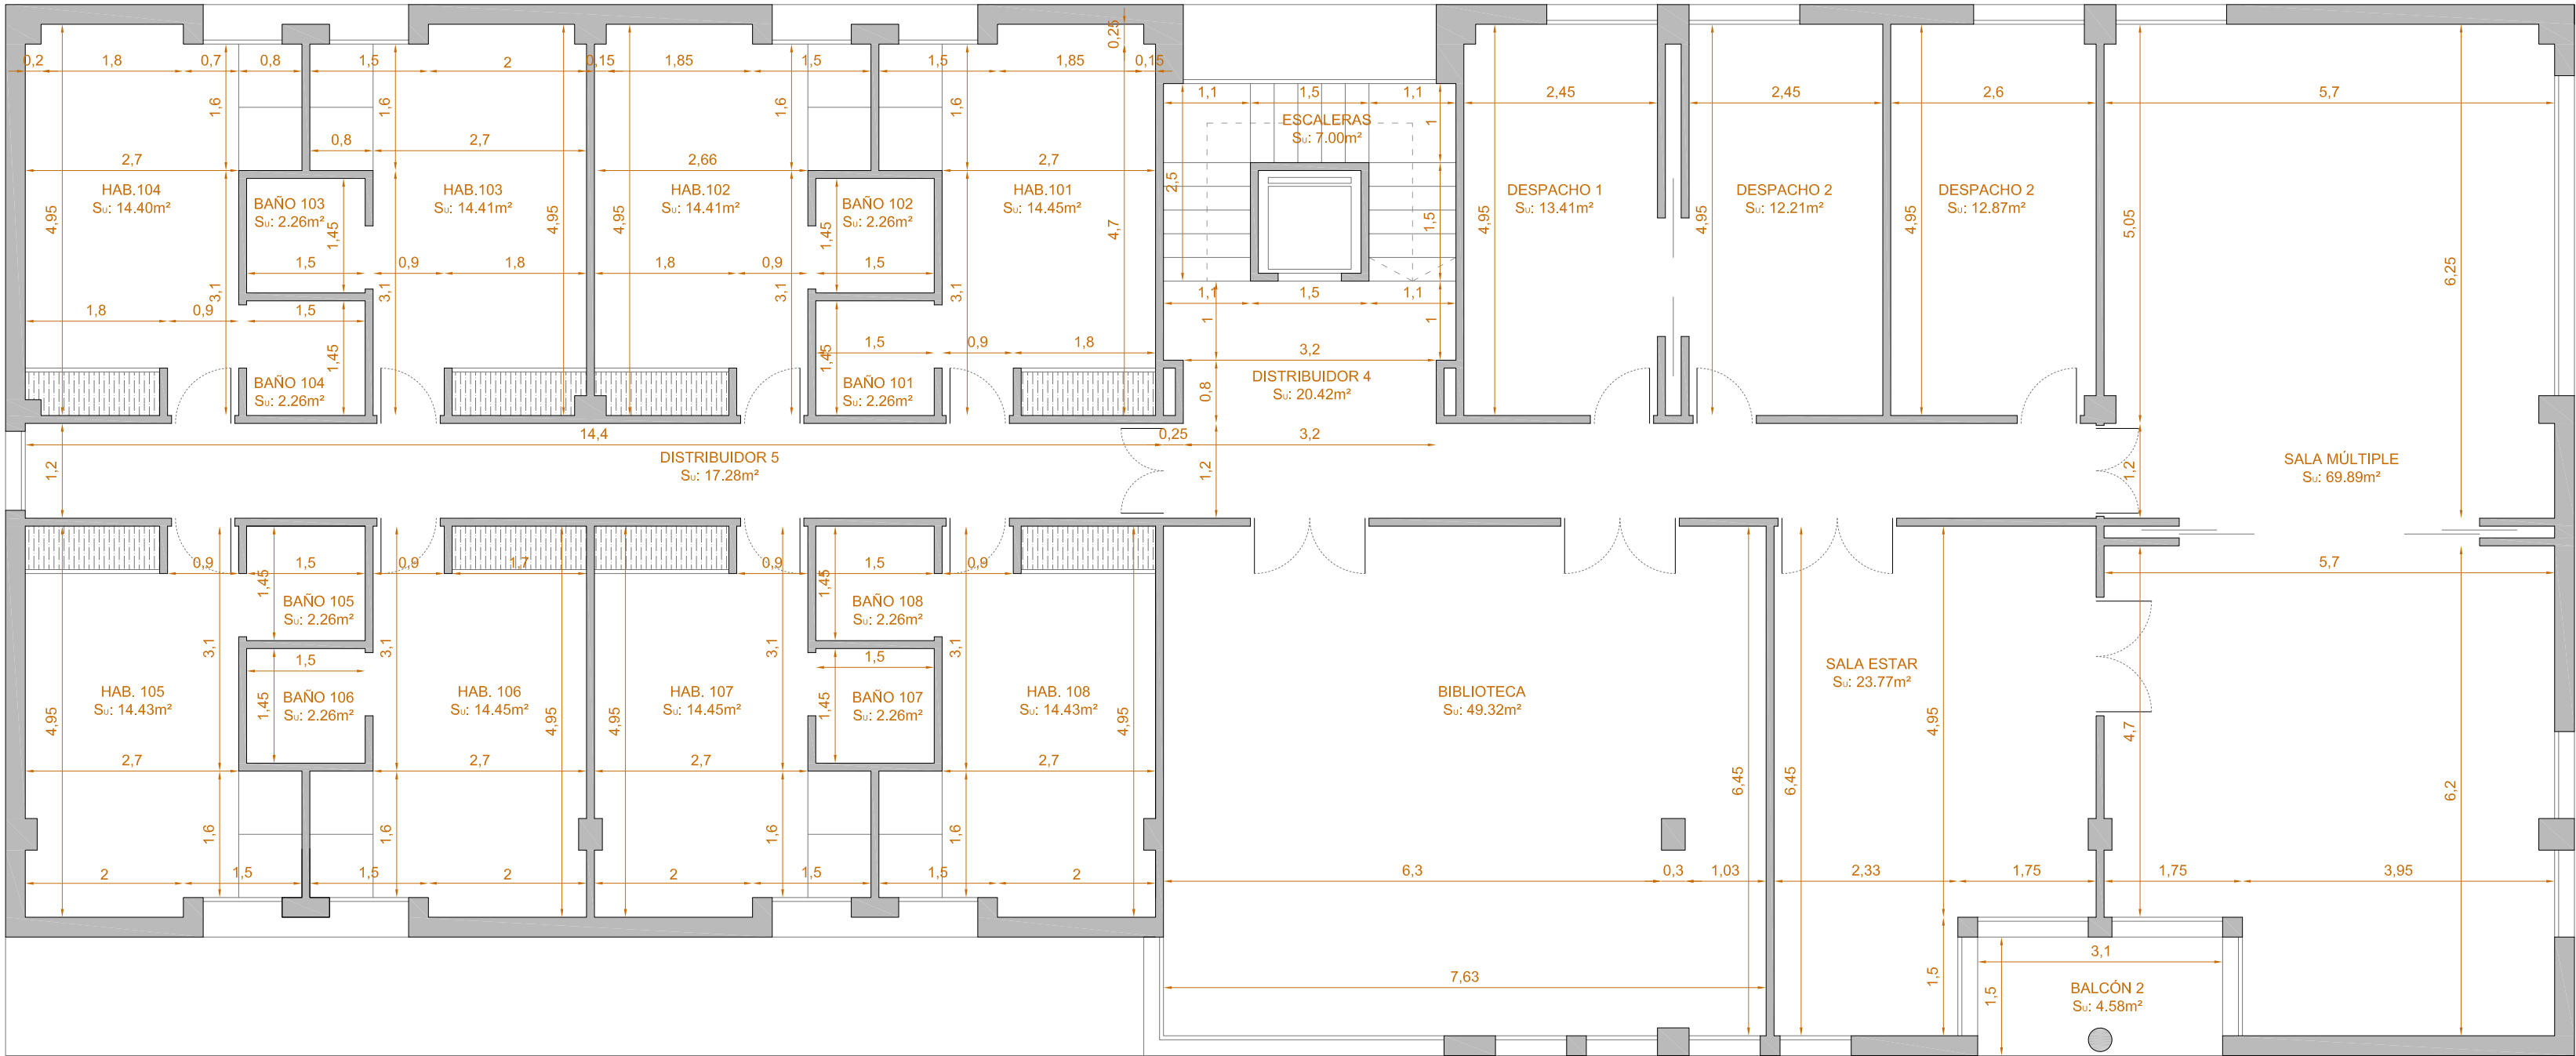

PLANTA SEGUNDA

0 1 5m

APUNTOARQUITECTURA
teléfono: 649612449
www.apuntoarquitectura.com
oficina@apuntoarquitectura.com

PROYECTO
PROYECTO BÁSICO DE OBRAS PARA EL CAMBIO DE
USO DE EDIFICIO RESIDENCIAL A TERCIARIO
HOSPEDAJE. LICENCIA DE ACTIVIDAD_
HOTEL DE 2 ESTRELLAS. Cl. Haro 5; 28043 Madrid

TITULAR
HARO 5 VENTURES S.L.
N.I.F.: B22599070
REPRESENTANTE
Rafael Garrido Rodrigo
D.N.I.: 00839470Q

TÉCNICO
Jorge Serrano de La Torre
COLEGIADO COAM 17.677


DESCRIPCIÓN
ARQUITECTURA ACTUAL: PLANTAS 2

NÚMERO DE PLANO FECHA ESCALA


A02 17.04.2026 1:75



QR validation

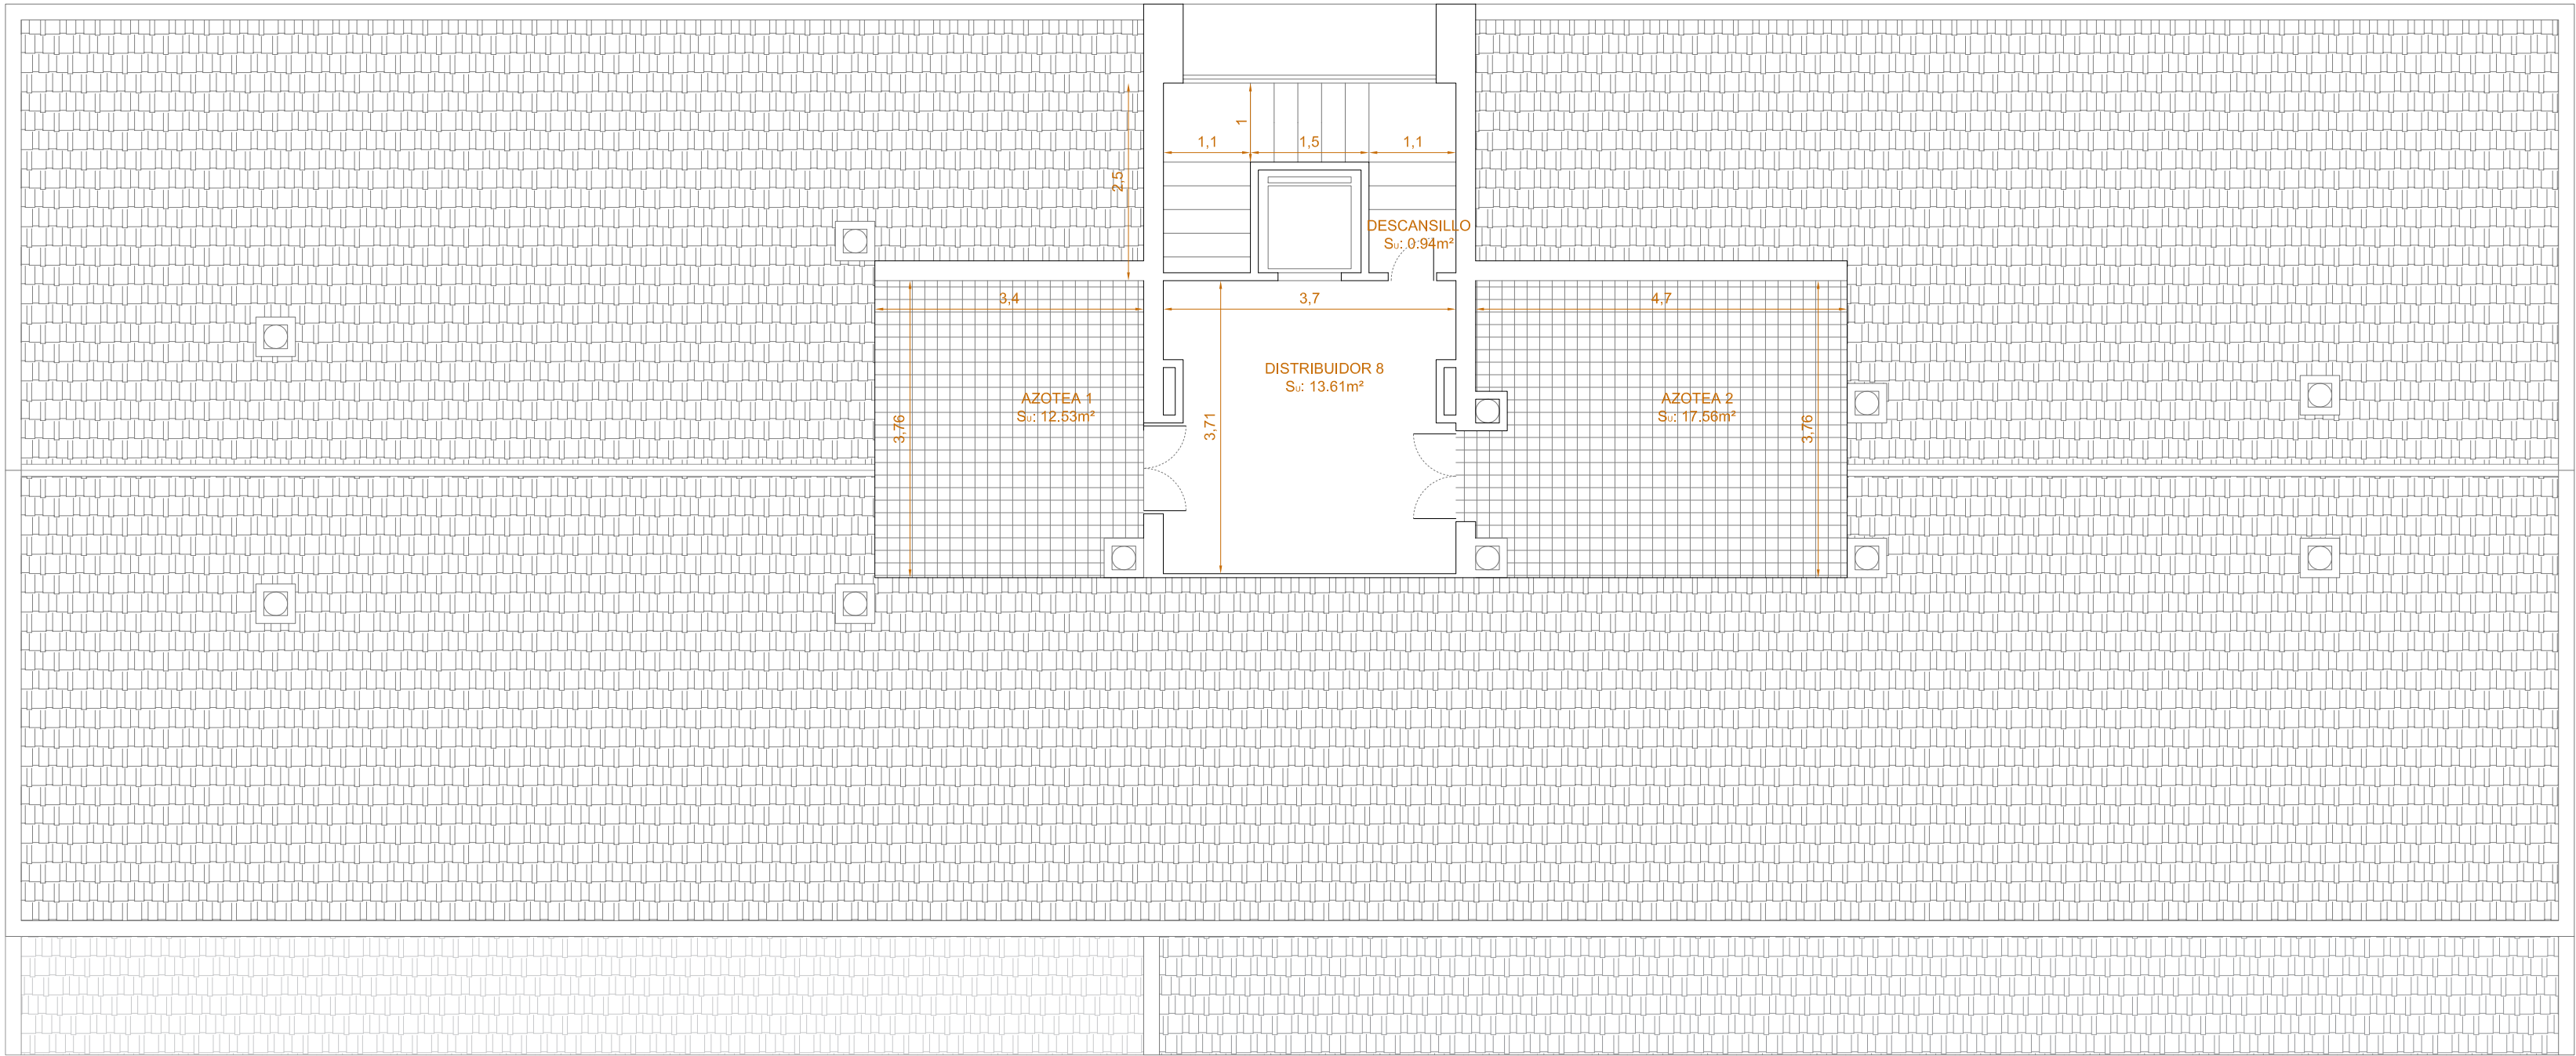

PLANTA BAJO CUBIERTA

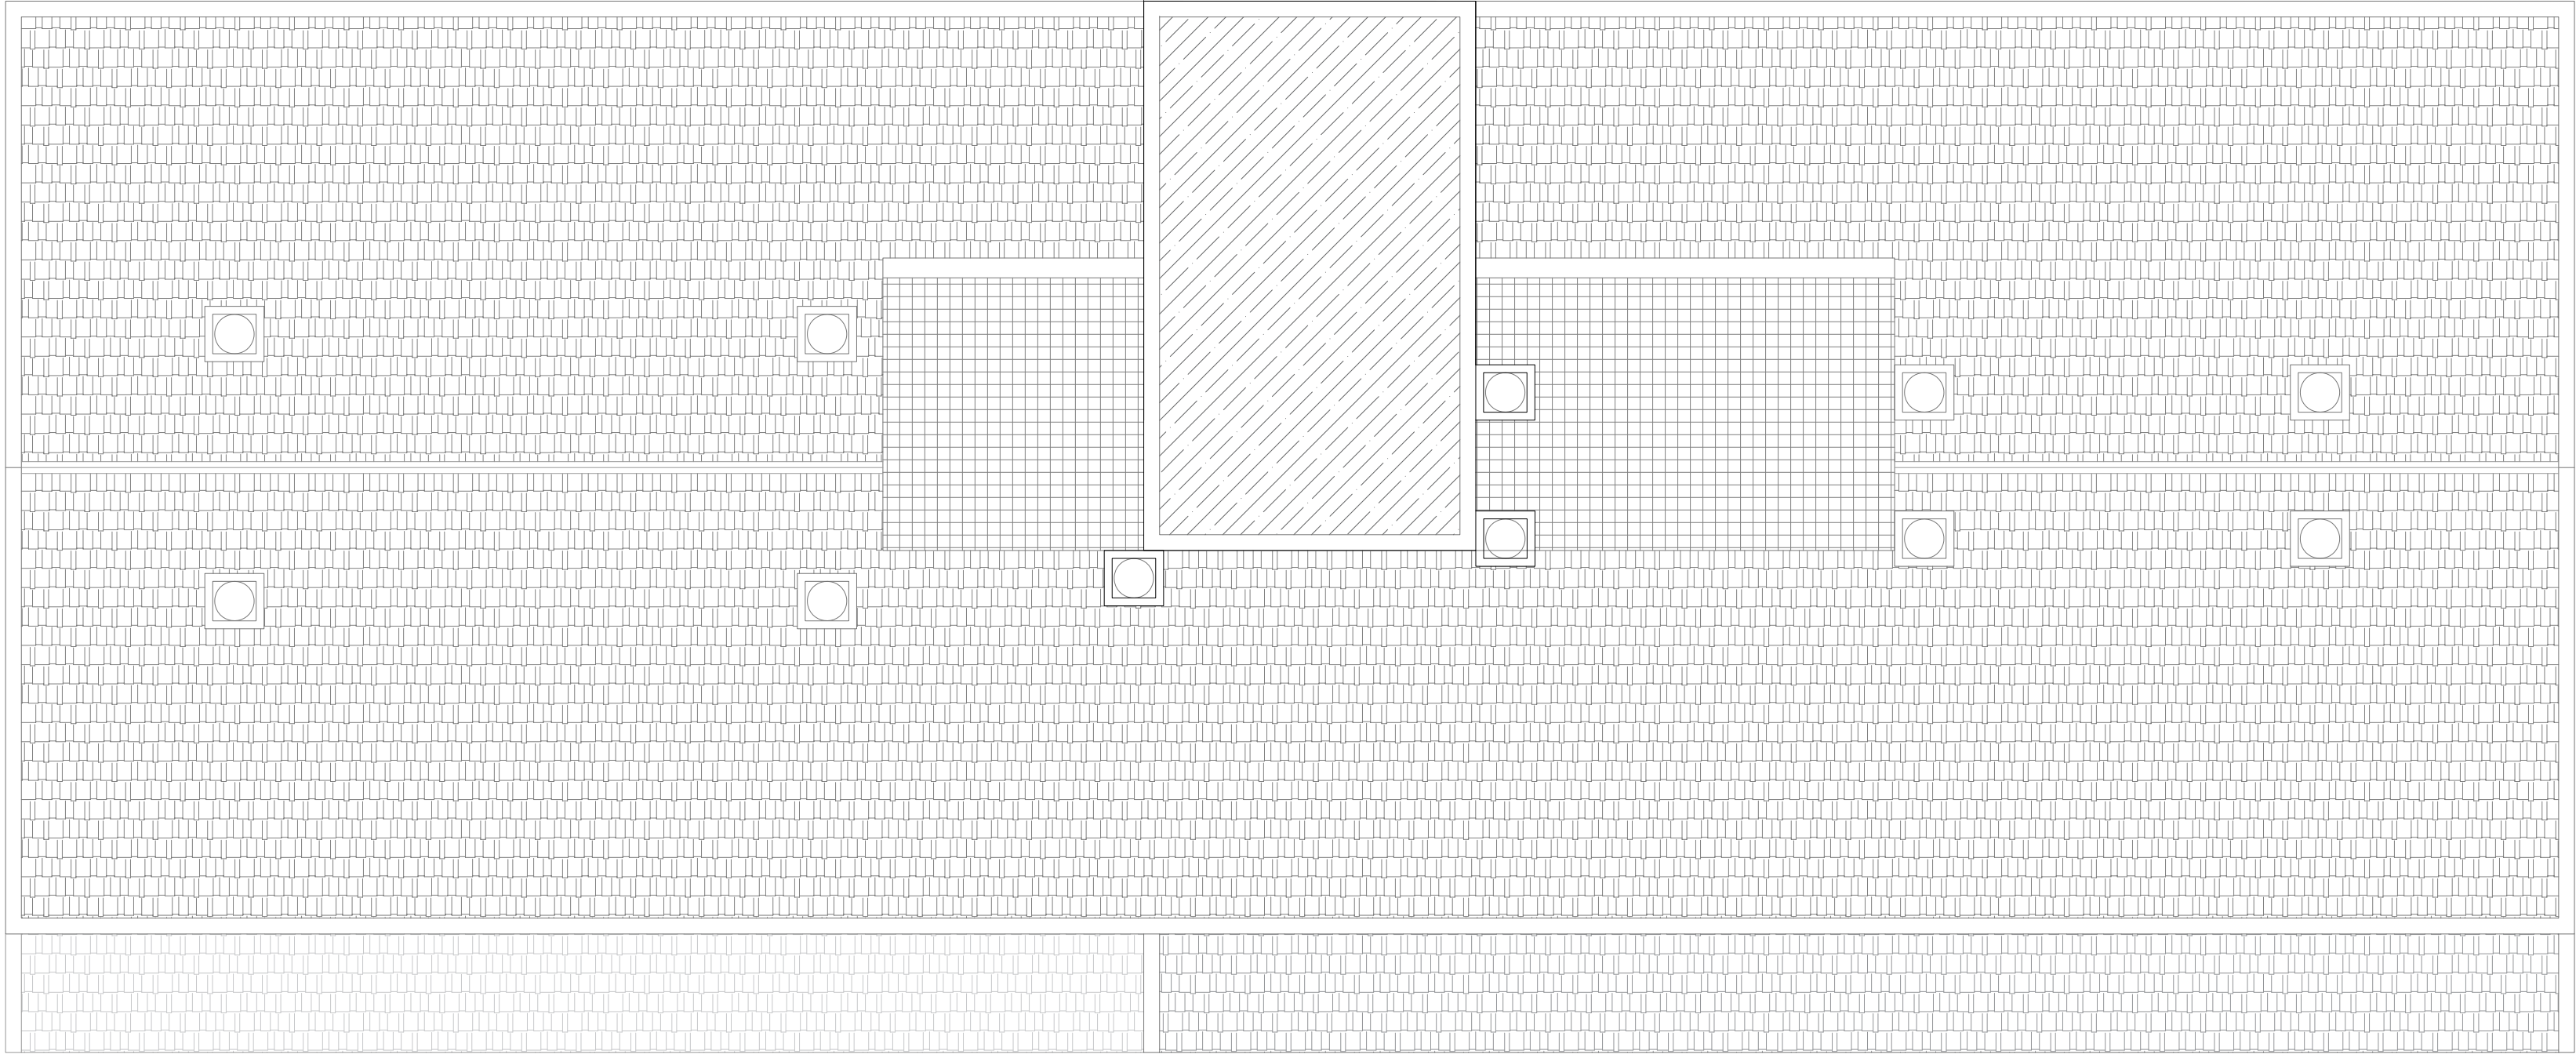

PLANTA CUBIERTA



APUNTOARQUITECTURA
teléfono: 649612449
www.apuntoarquitectura.com
oficina@apuntoarquitectura.com

PROYECTO
PROYECTO BÁSICO DE OBRAS PARA EL CAMBIO DE
USO DE EDIFICIO RESIDENCIAL A TERCIARIO
HOSPEDAJE. LICENCIA DE ACTIVIDAD_
HOTEL DE 2 ESTRELLAS. Cl. Haro 5; 28043 Madrid
TITULAR
HARO 5 VENTURES S.L.
N.I.F.: B22599070
REPRESENTANTE
Rafael Garrido Rodrigo
D.N.I.: 00839470Q

TÉCNICO
Jorge Serrano de La Torre
COLEGIADO COAM 17.677

DESCRIPCIÓN


ARQUITECTURA ACTUAL: PLANTAS 2

NÚMERO DE PLANO FECHA ESCALA

A03 17.04.2026 1:75



QR validation

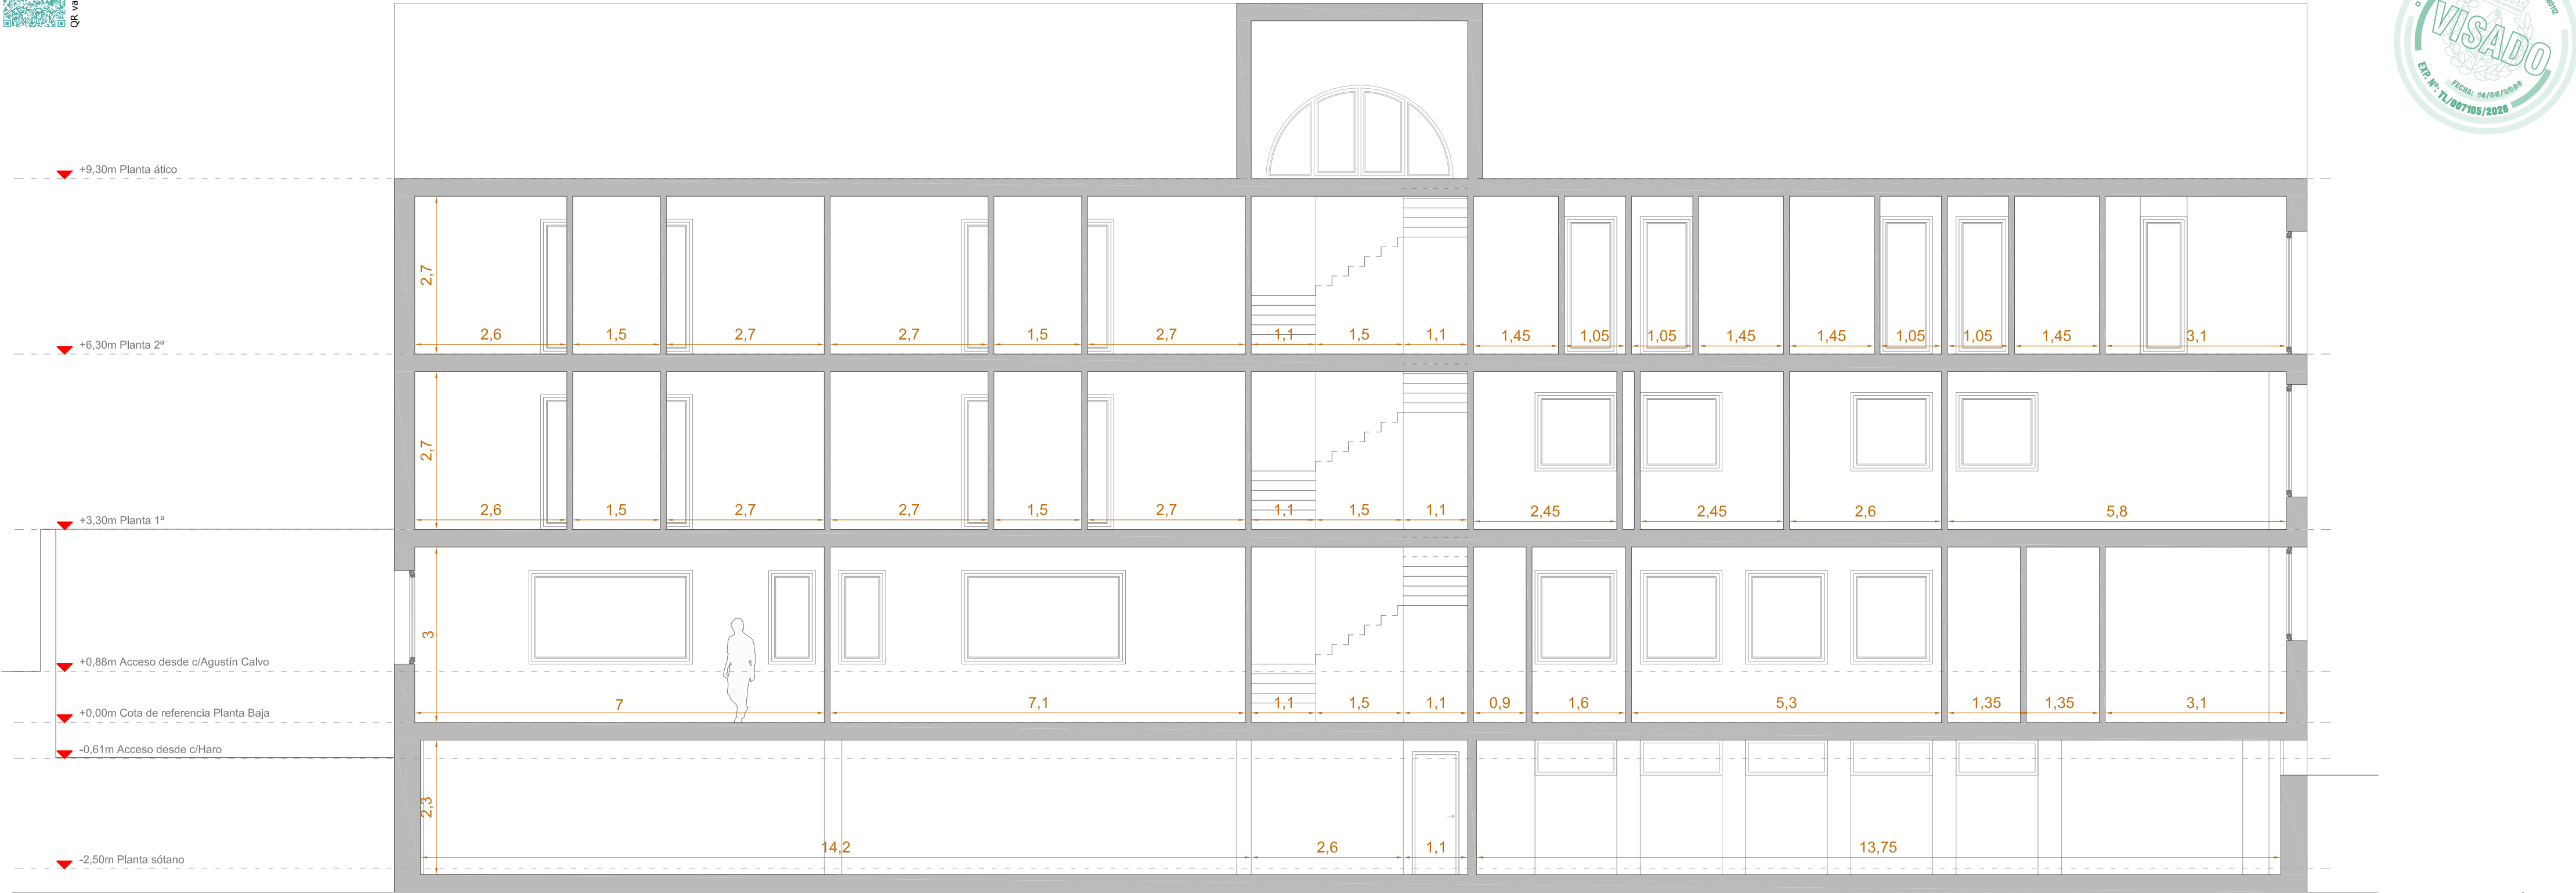

SECCIÓN 1



APUNTOARQUITECTURA
teléfono: 649612449
www.apuntoarquitectura.com
oficina@apuntoarquitectura.com

PROYECTO
PROYECTO BÁSICO DE OBRAS PARA EL CAMBIO DE
USO DE EDIFICIO RESIDENCIAL A TERCIARIO
HOSPEDAJE. LICENCIA DE ACTIVIDAD_
HOTEL DE 2 ESTRELLAS. Cl. Haro 5; 28043 Madrid
TITULAR
HARO 5 VENTURES S.L.
N.I.F.: B22599070
REPRESENTANTE
Rafael Garrido Rodrigo
D.N.I.: 00839470Q

TÉCNICO
Jorge Serrano de La Torre
COLEGIADO COAM 17.677


DESCRIPCIÓN
ARQUITECTURA ACTUAL: SECCIÓN 1

NÚMERO DE PLANO FECHA ESCALA


A04 17.04.2026 1:75



QR validacion

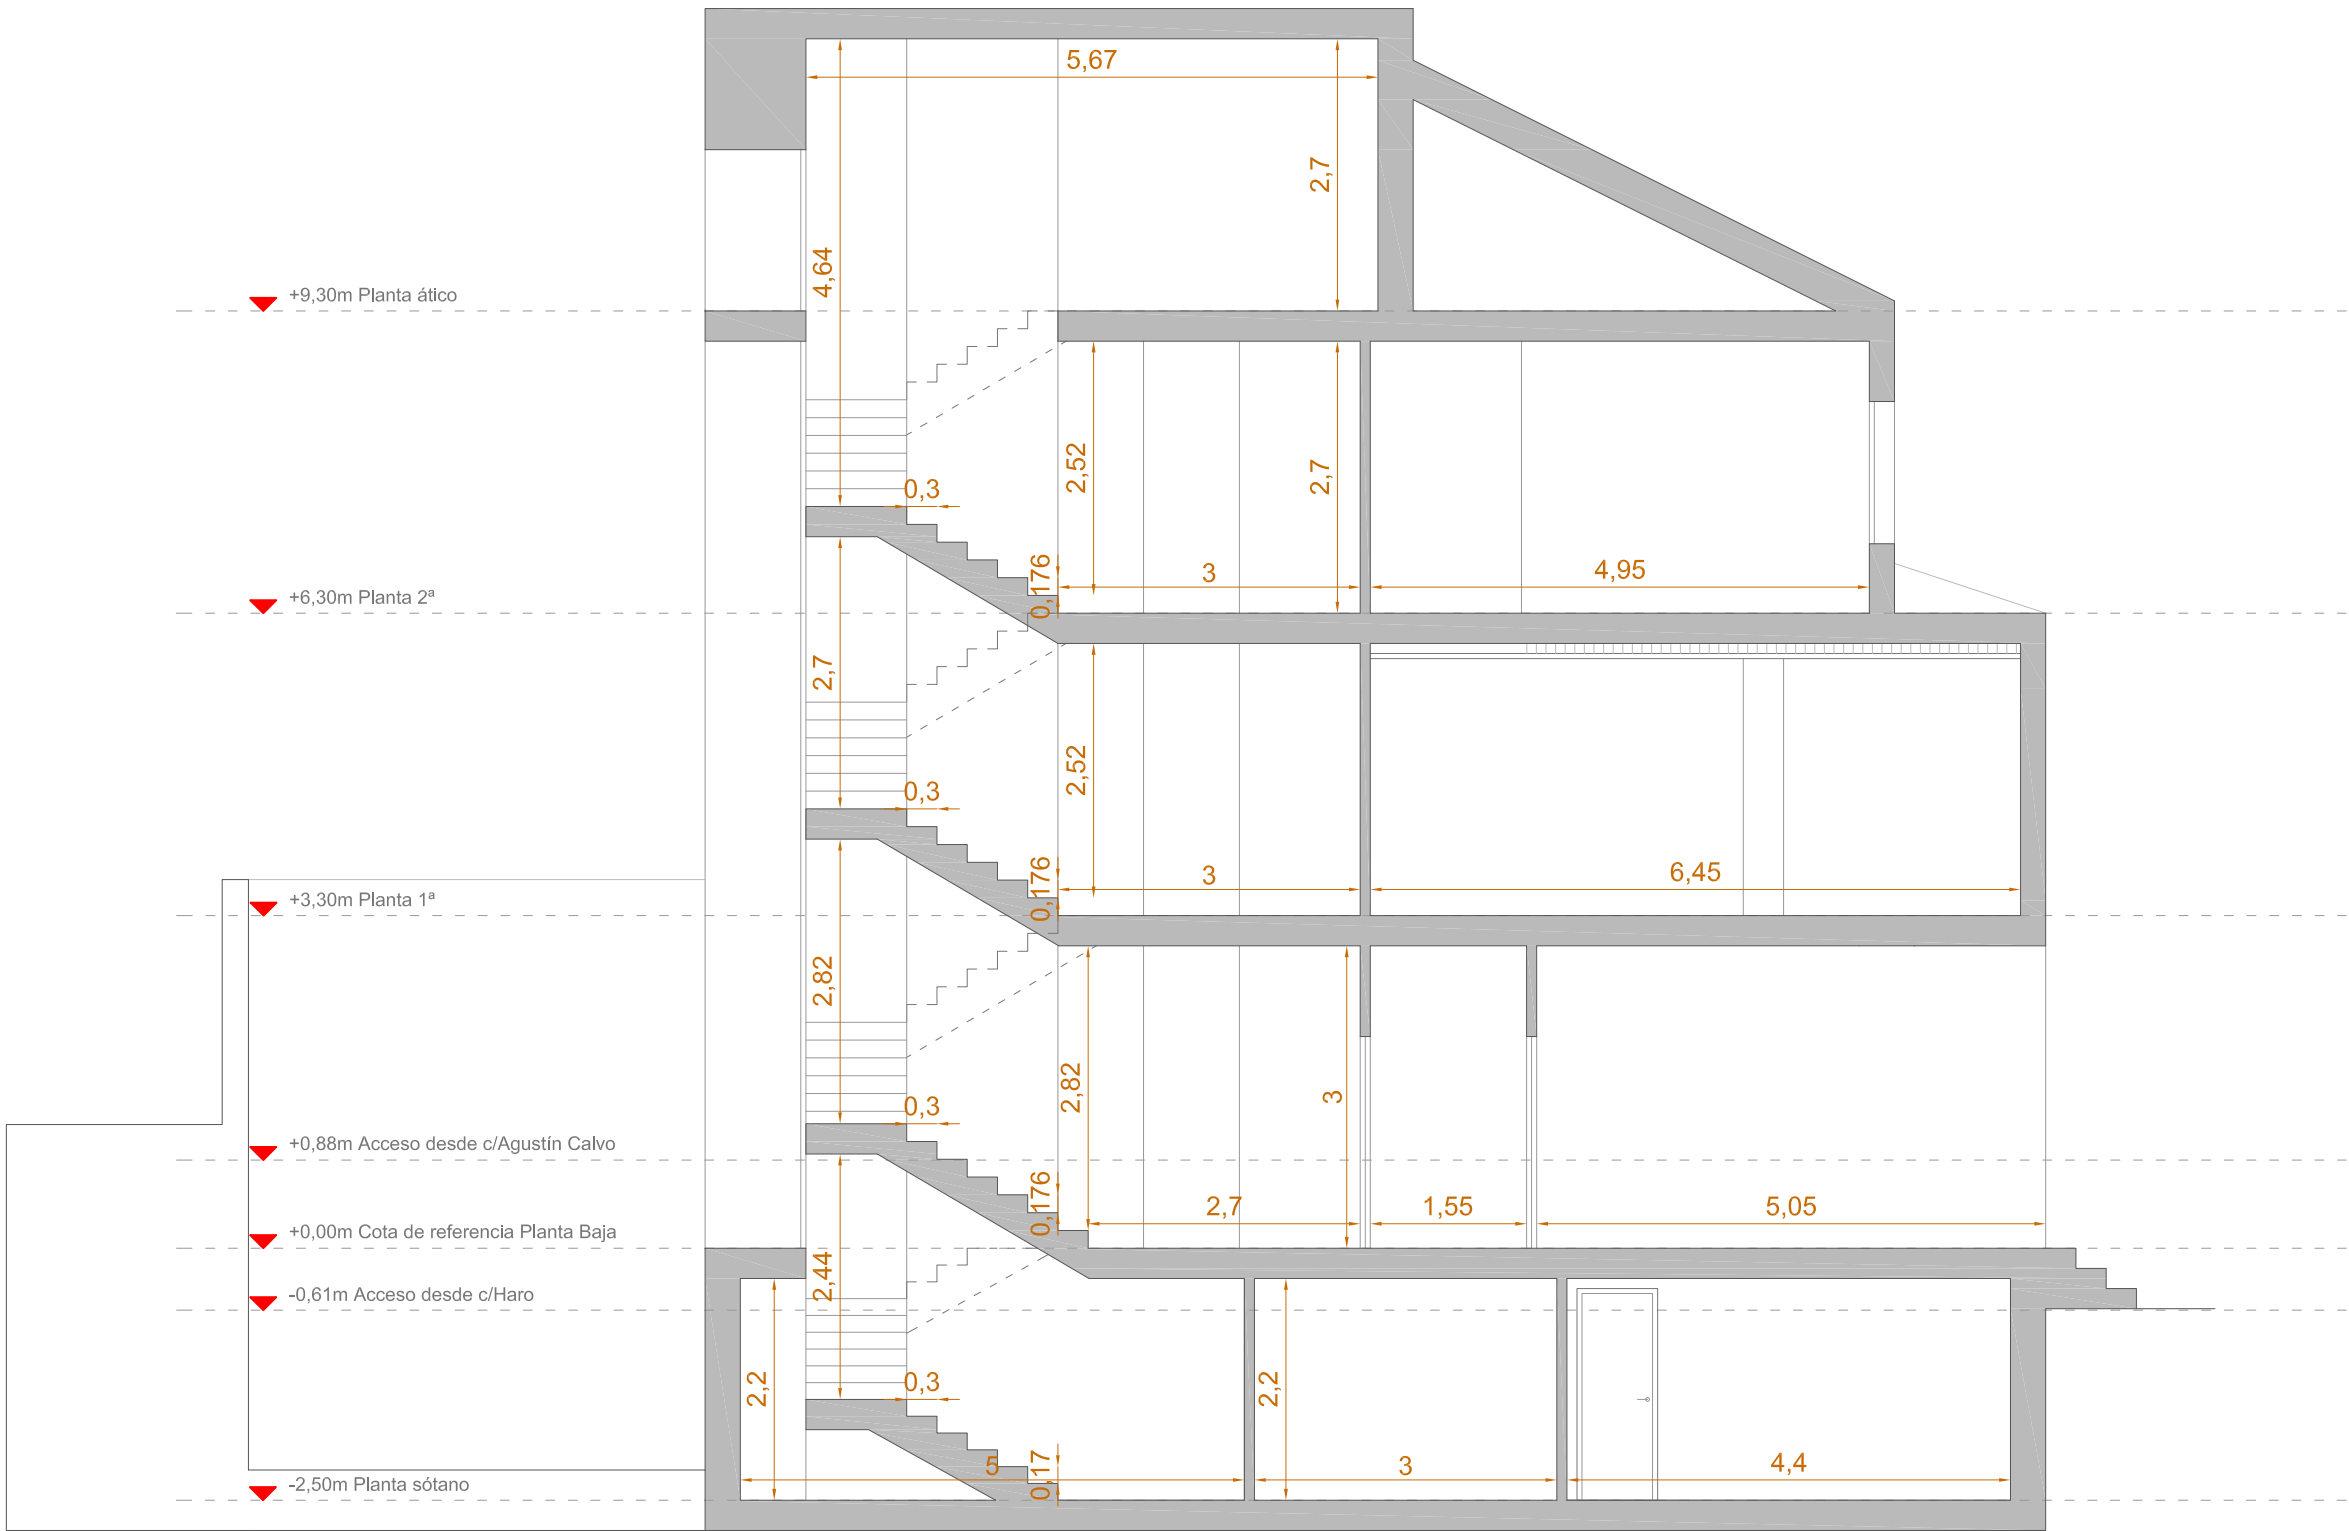

SECCIÓN 2

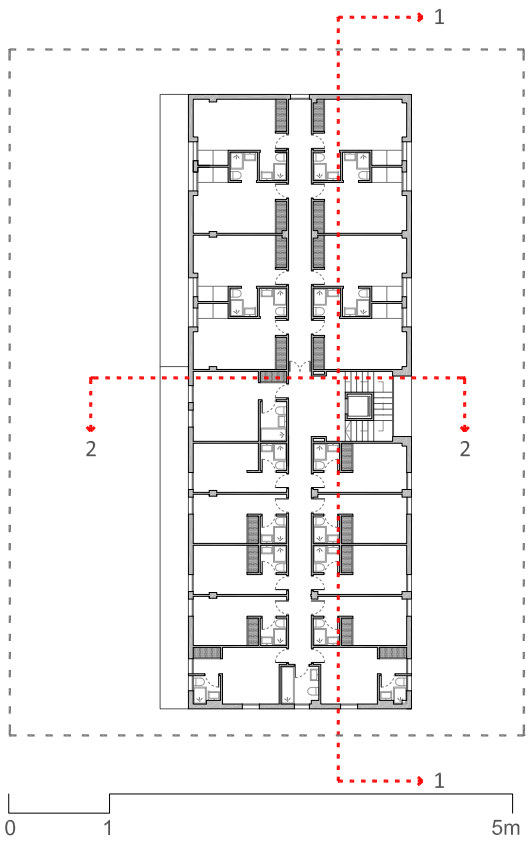

APUNTOARQUITECTURA
teléfono: 649612449
www.apuntoarquitectura.com
oficina@apuntoarquitectura.com

PROYECTO
PROYECTO BÁSICO DE OBRAS PARA EL CAMBIO DE
USO DE EDIFICIO RESIDENCIAL A TERCARIO
HOSPEDAJE. LICENCIA DE ACTIVIDAD_
HOTEL DE 2 ESTRELLAS. Cl. Haro 5; 28043 Madrid
TITULAR
HARO 5 VENTURES S.L.
N.I.F.: B22599070
REPRESENTANTE
Rafael Garrido Rodrigo
D.N.I.: 00839470Q

TÉCNICO
Jorge Serrano de La Torre
COLEGIADO COAM 17.677


DESCRIPCIÓN
ARQUITECTURA ACTUAL: SECCIÓN 2

NÚMERO DE PLANO FECHA ESCALA

A05 17.04.2026 1:75



QR validacion

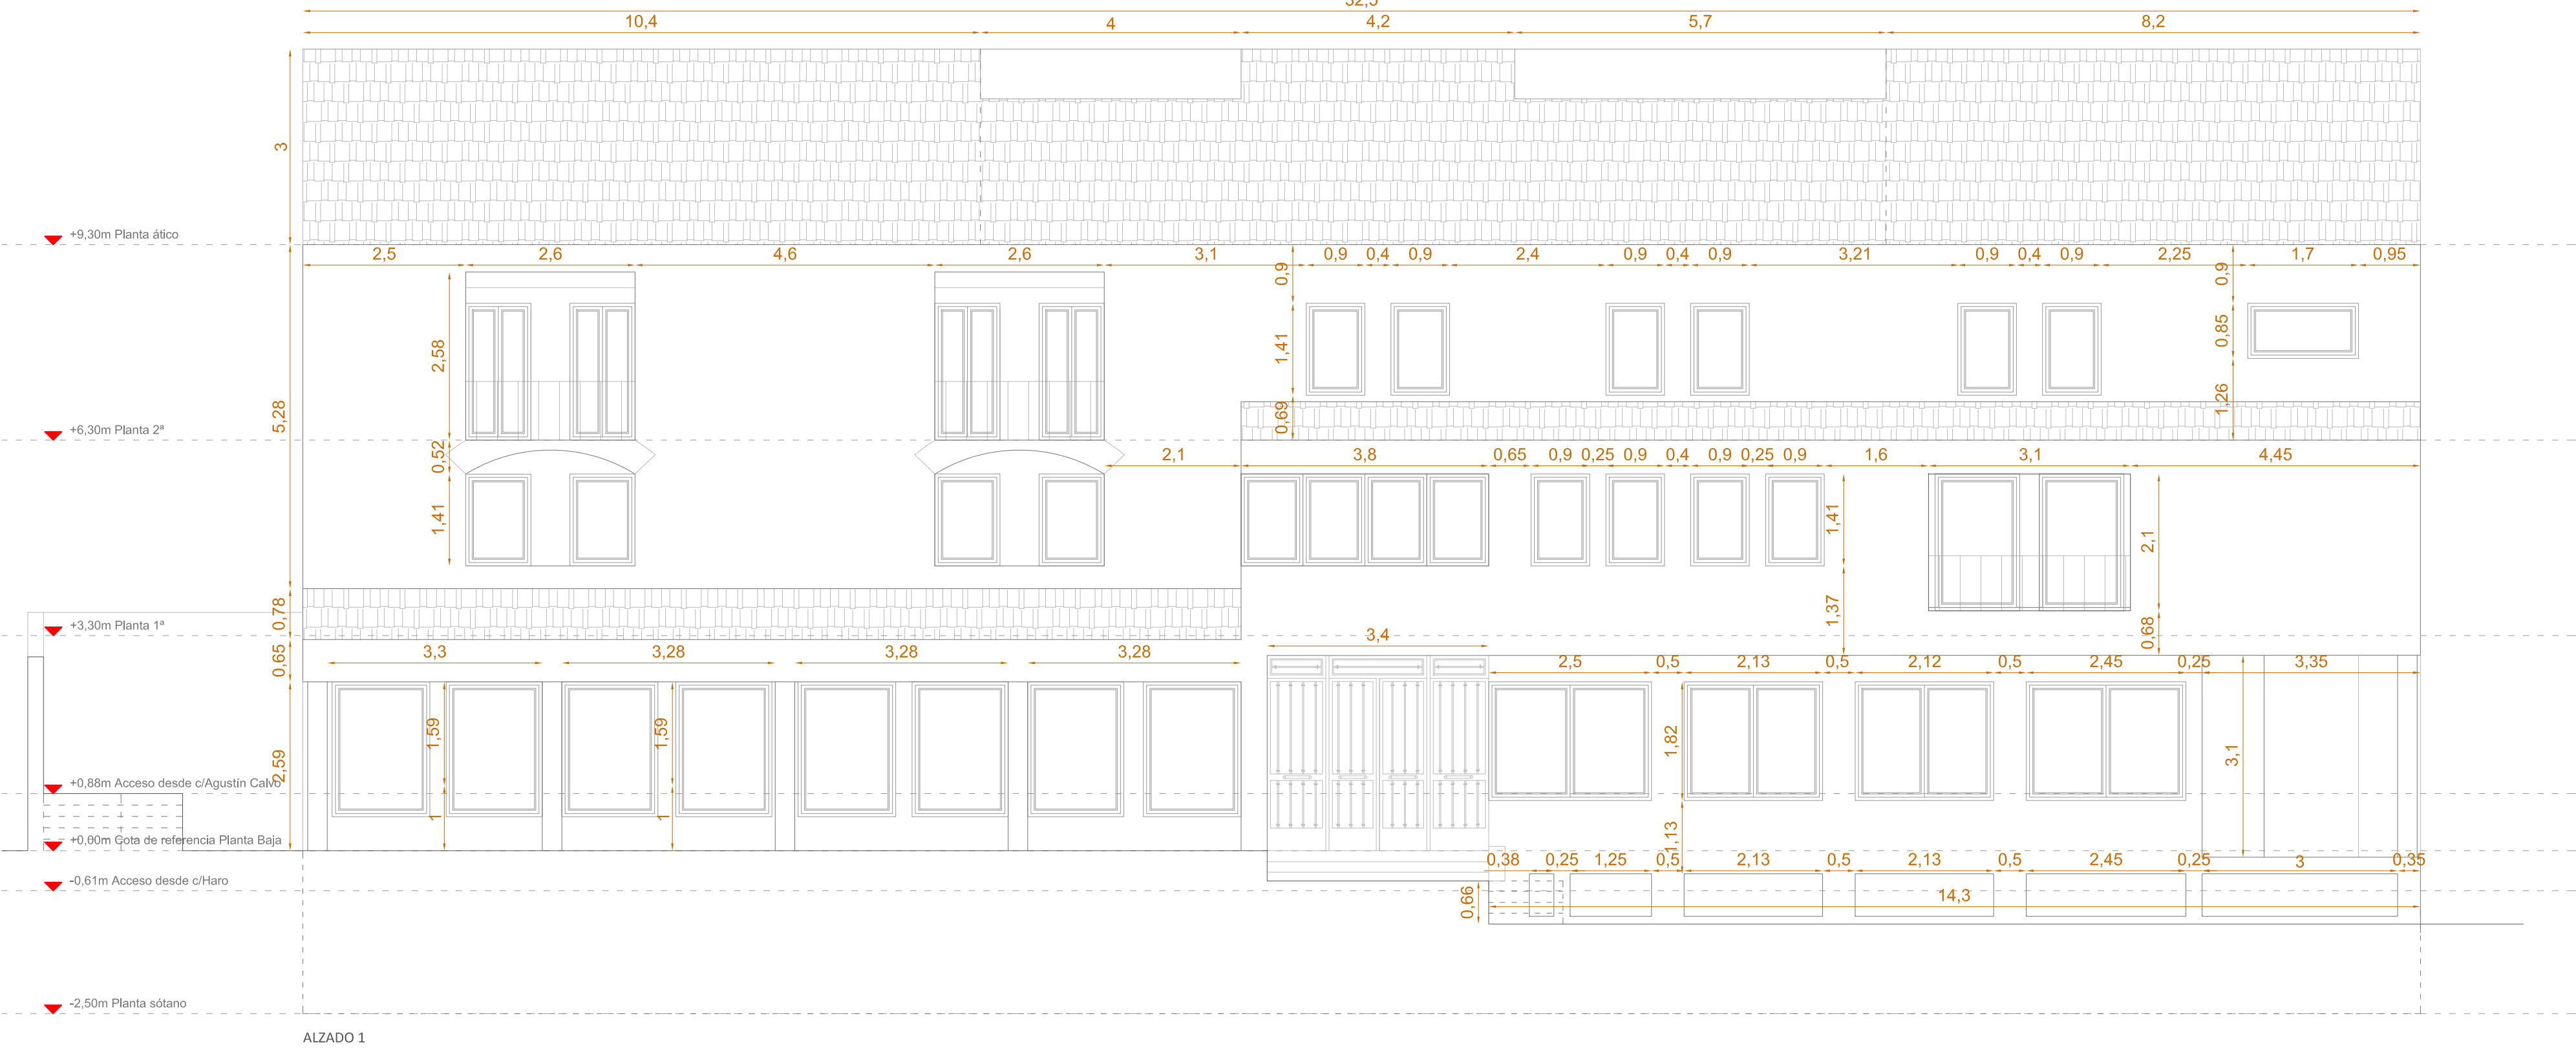

APUNTOARQUITECTURA
teléfono: 649612449
www.apuntoarquitectura.com
oficina@apuntoarquitectura.com

PROYECTO
PROYECTO BÁSICO DE OBRAS PARA EL CAMBIO DE
USO DE EDIFICIO RESIDENCIAL A TERCARIO
HOSPEDAJE. LICENCIA DE ACTIVIDAD_
HOTEL DE 2 ESTRELLAS. Cl. Haro 5; 28043 Madrid
TITULAR
HARO 5 VENTURES S.L.
N.I.F.: B22599070
REPRESENTANTE
Rafael Garrido Rodrigo
D.N.I.: 00839470Q

TÉCNICO
Jorge Serrano de La Torre
COLEGIADO COAM 17.677


DESCRIPCIÓN

ARQUITECTURA: ALZADO 1

NÚMERO DE PLANO FECHA ESCALA

A06 17.04.2026 1:75

[Signature]

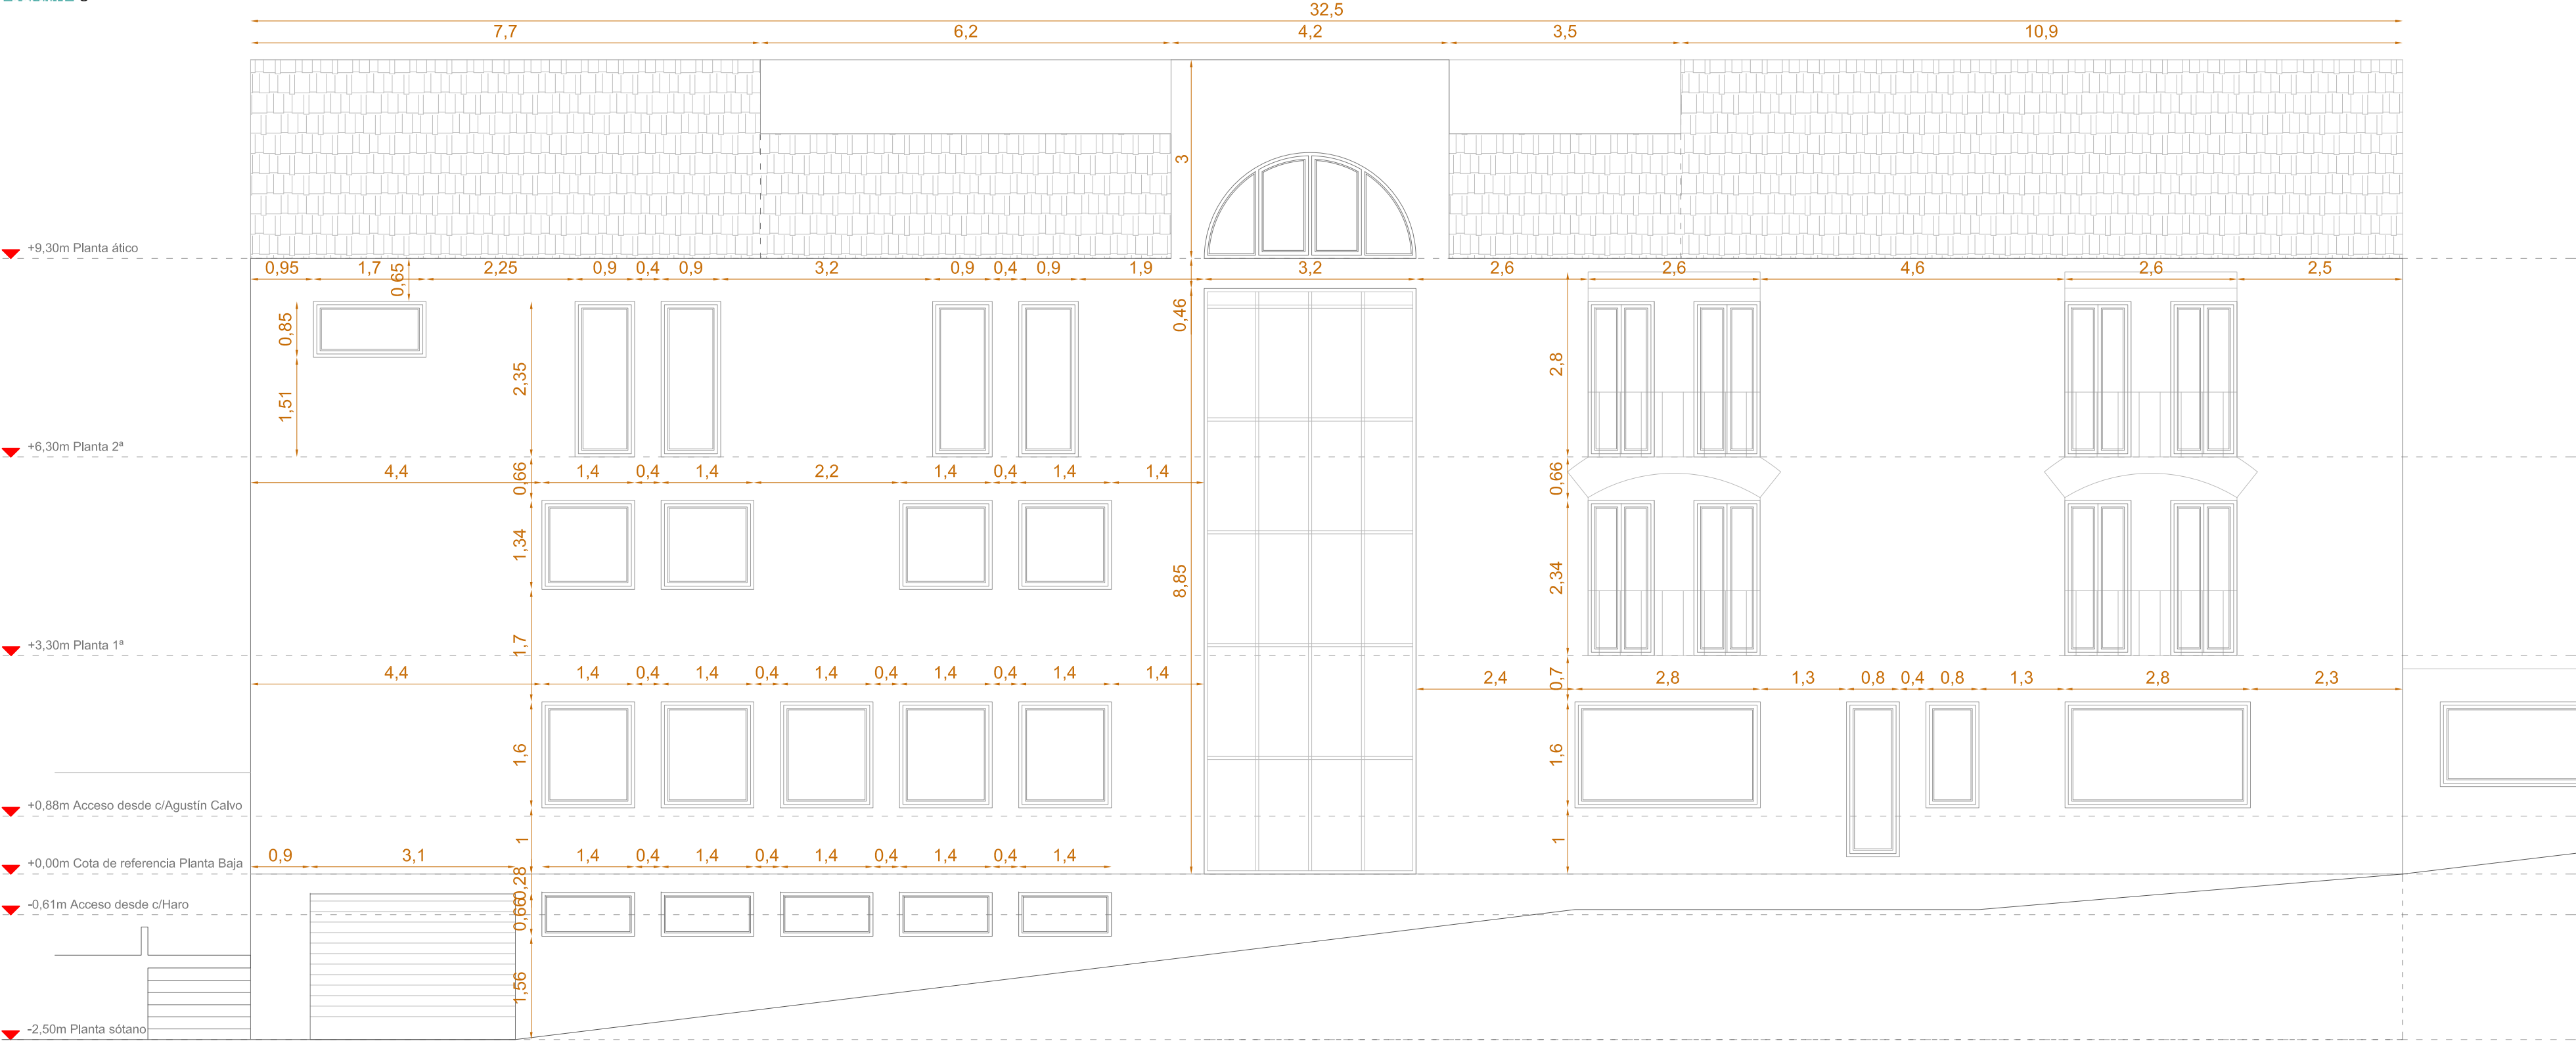

ALZADO 2



0 1 5m

APUNTOARQUITECTURA
teléfono: 649612449
www.apuntoarquitectura.com
oficina@apuntoarquitectura.com

PROYECTO
PROYECTO BÁSICO DE OBRAS PARA EL CAMBIO DE
USO DE EDIFICIO RESIDENCIAL A TERCIARIO
HOSPEDAJE. LICENCIA DE ACTIVIDAD_
HOTEL DE 2 ESTRELLAS. Cl. Haro 5; 28043 Madrid

TITULAR
HARO 5 VENTURES S.L.
N.I.F.: B22599070
REPRESENTANTE
Rafael Garrido Rodrigo
D.N.I.: 00839470Q

TÉCNICO
Jorge Serrano de La Torre
COLEGIADO COAM 17.677




DESCRIPCIÓN
ARQUITECTURA: ALZADO 2

NÚMERO DE PLANO FECHA ESCALA

A07 17.04.2026 1:75



QR validation

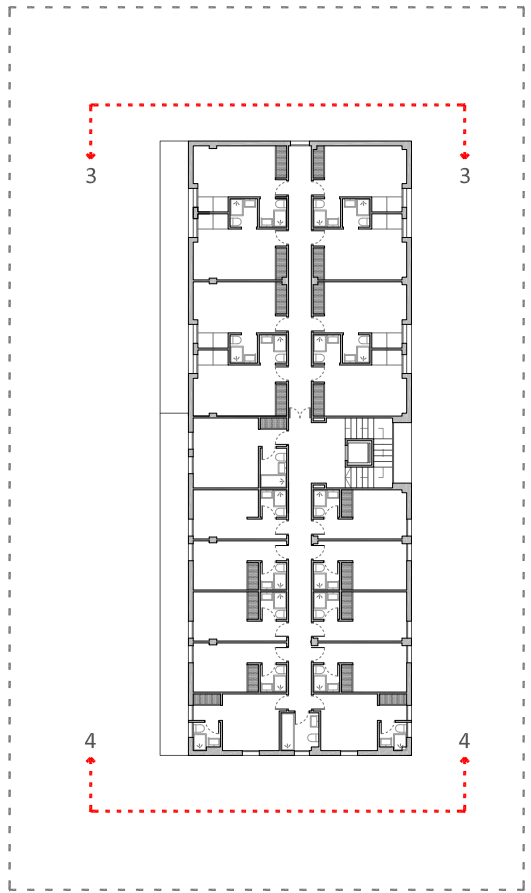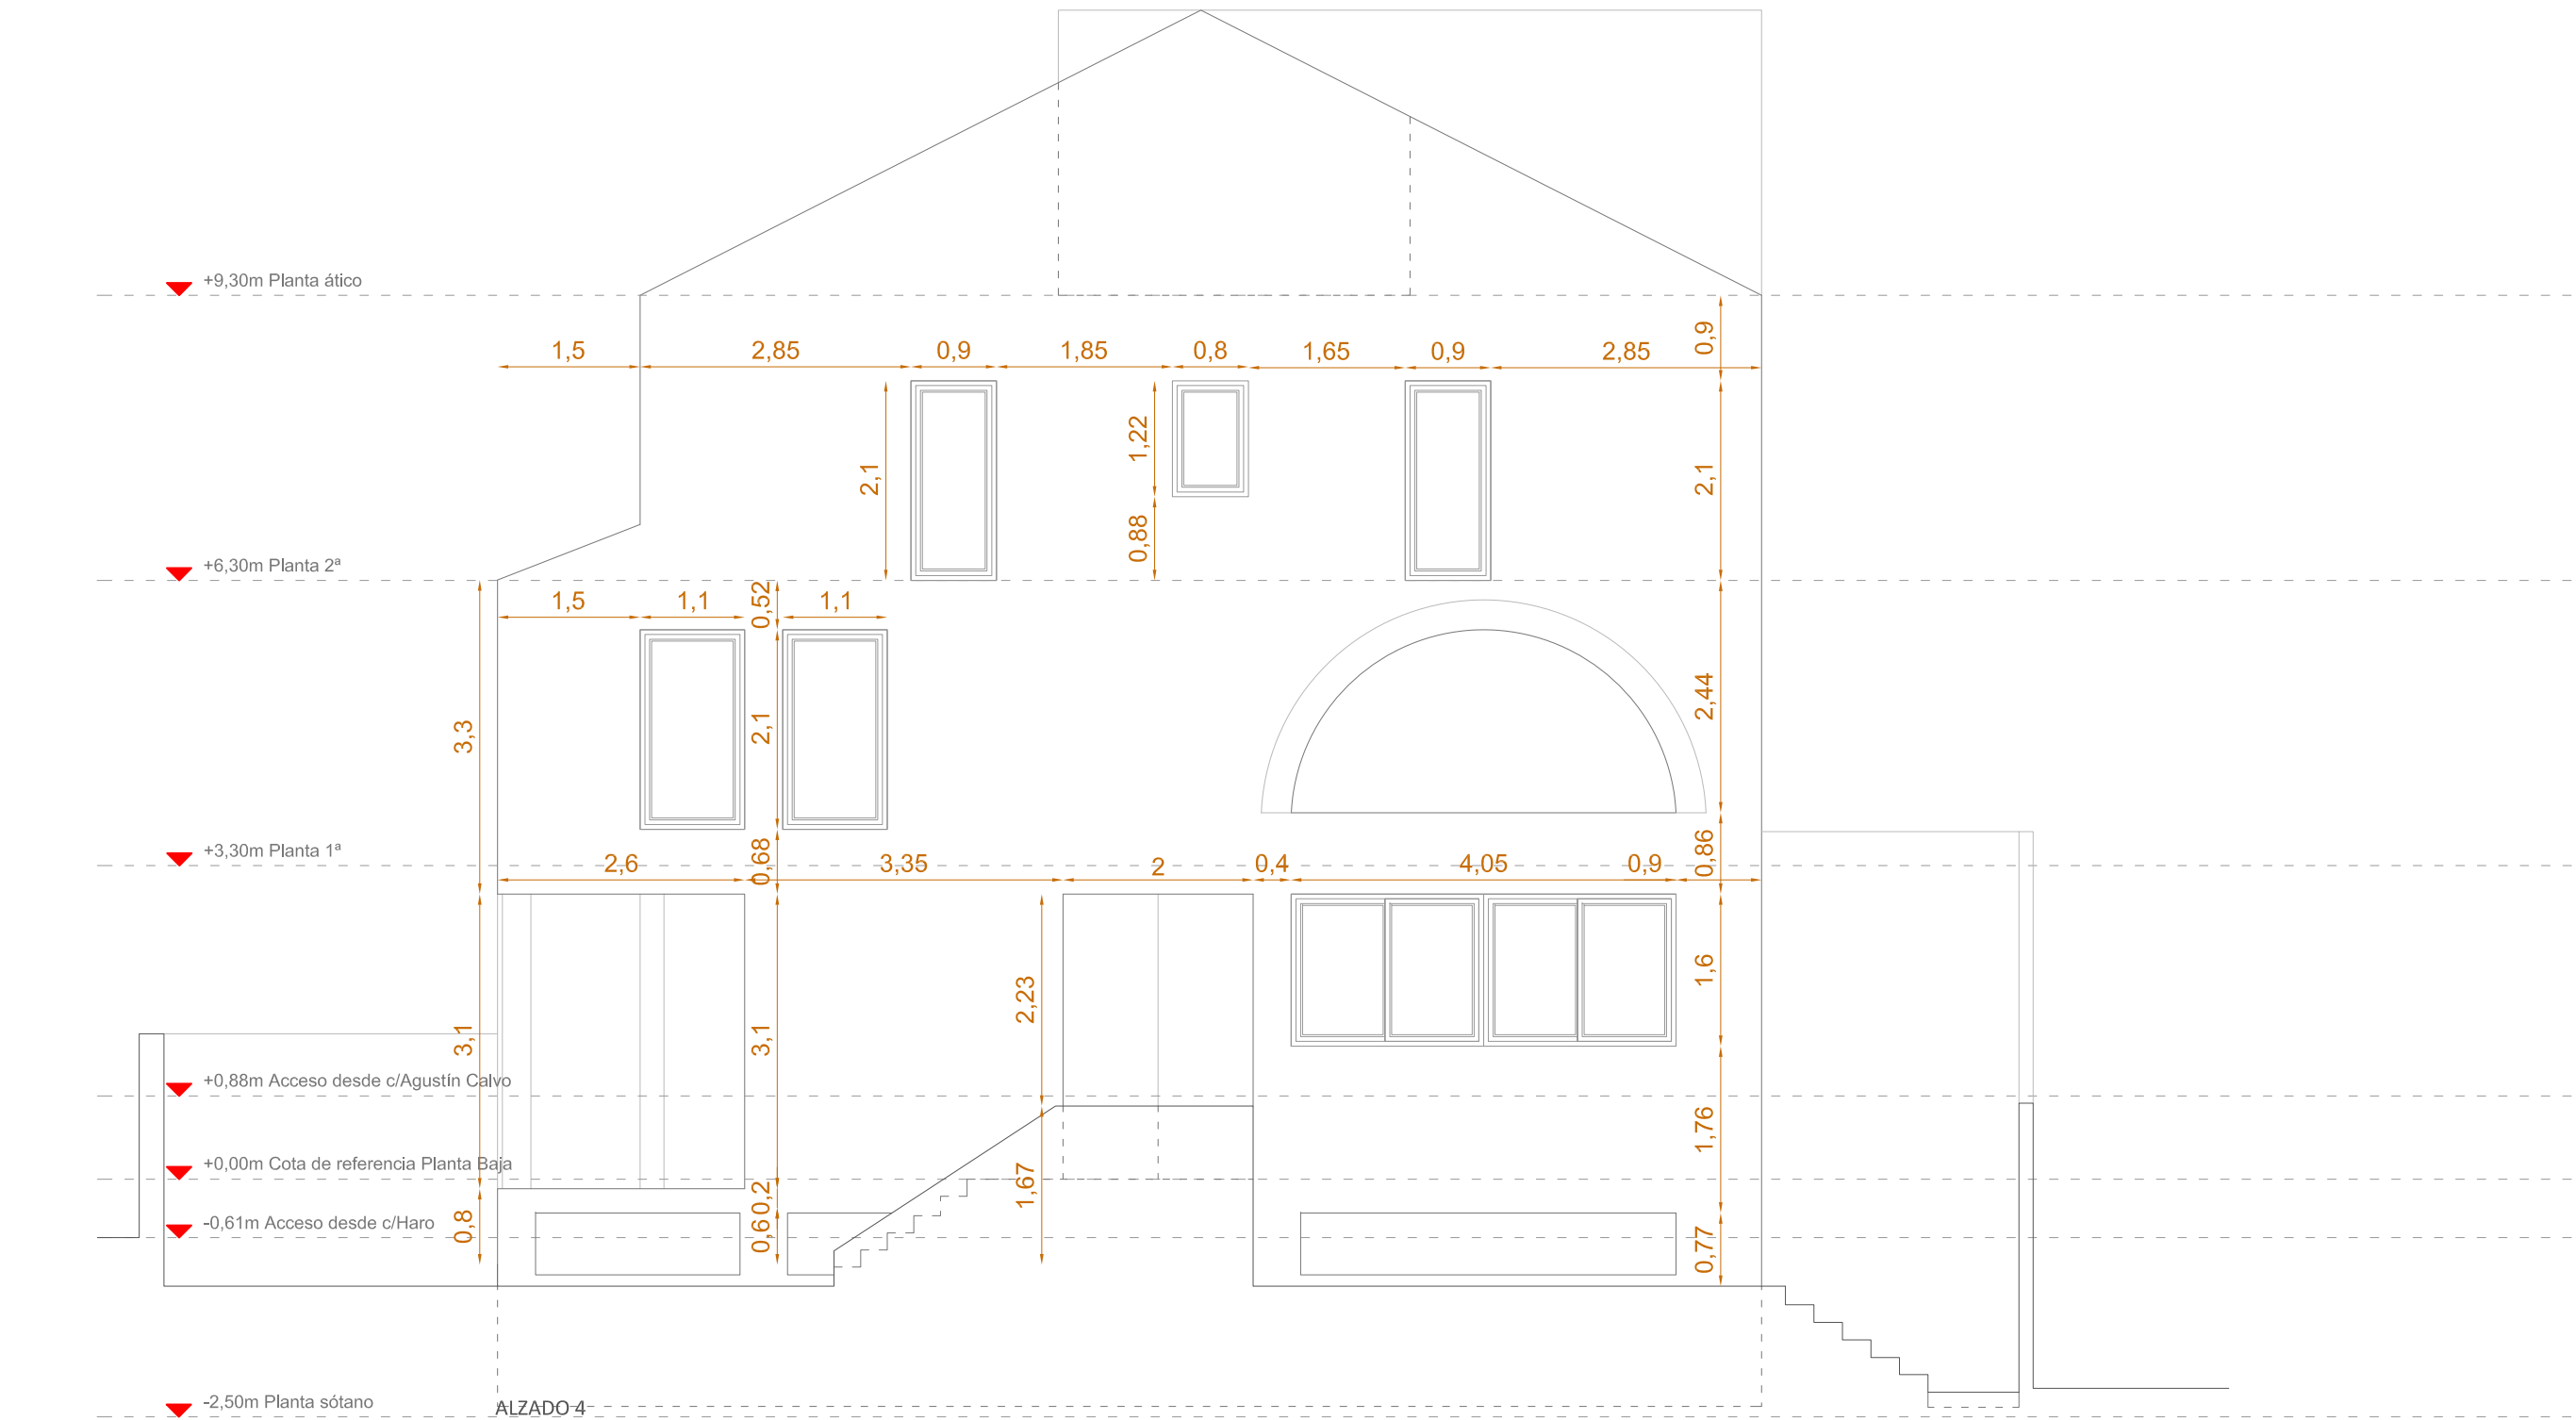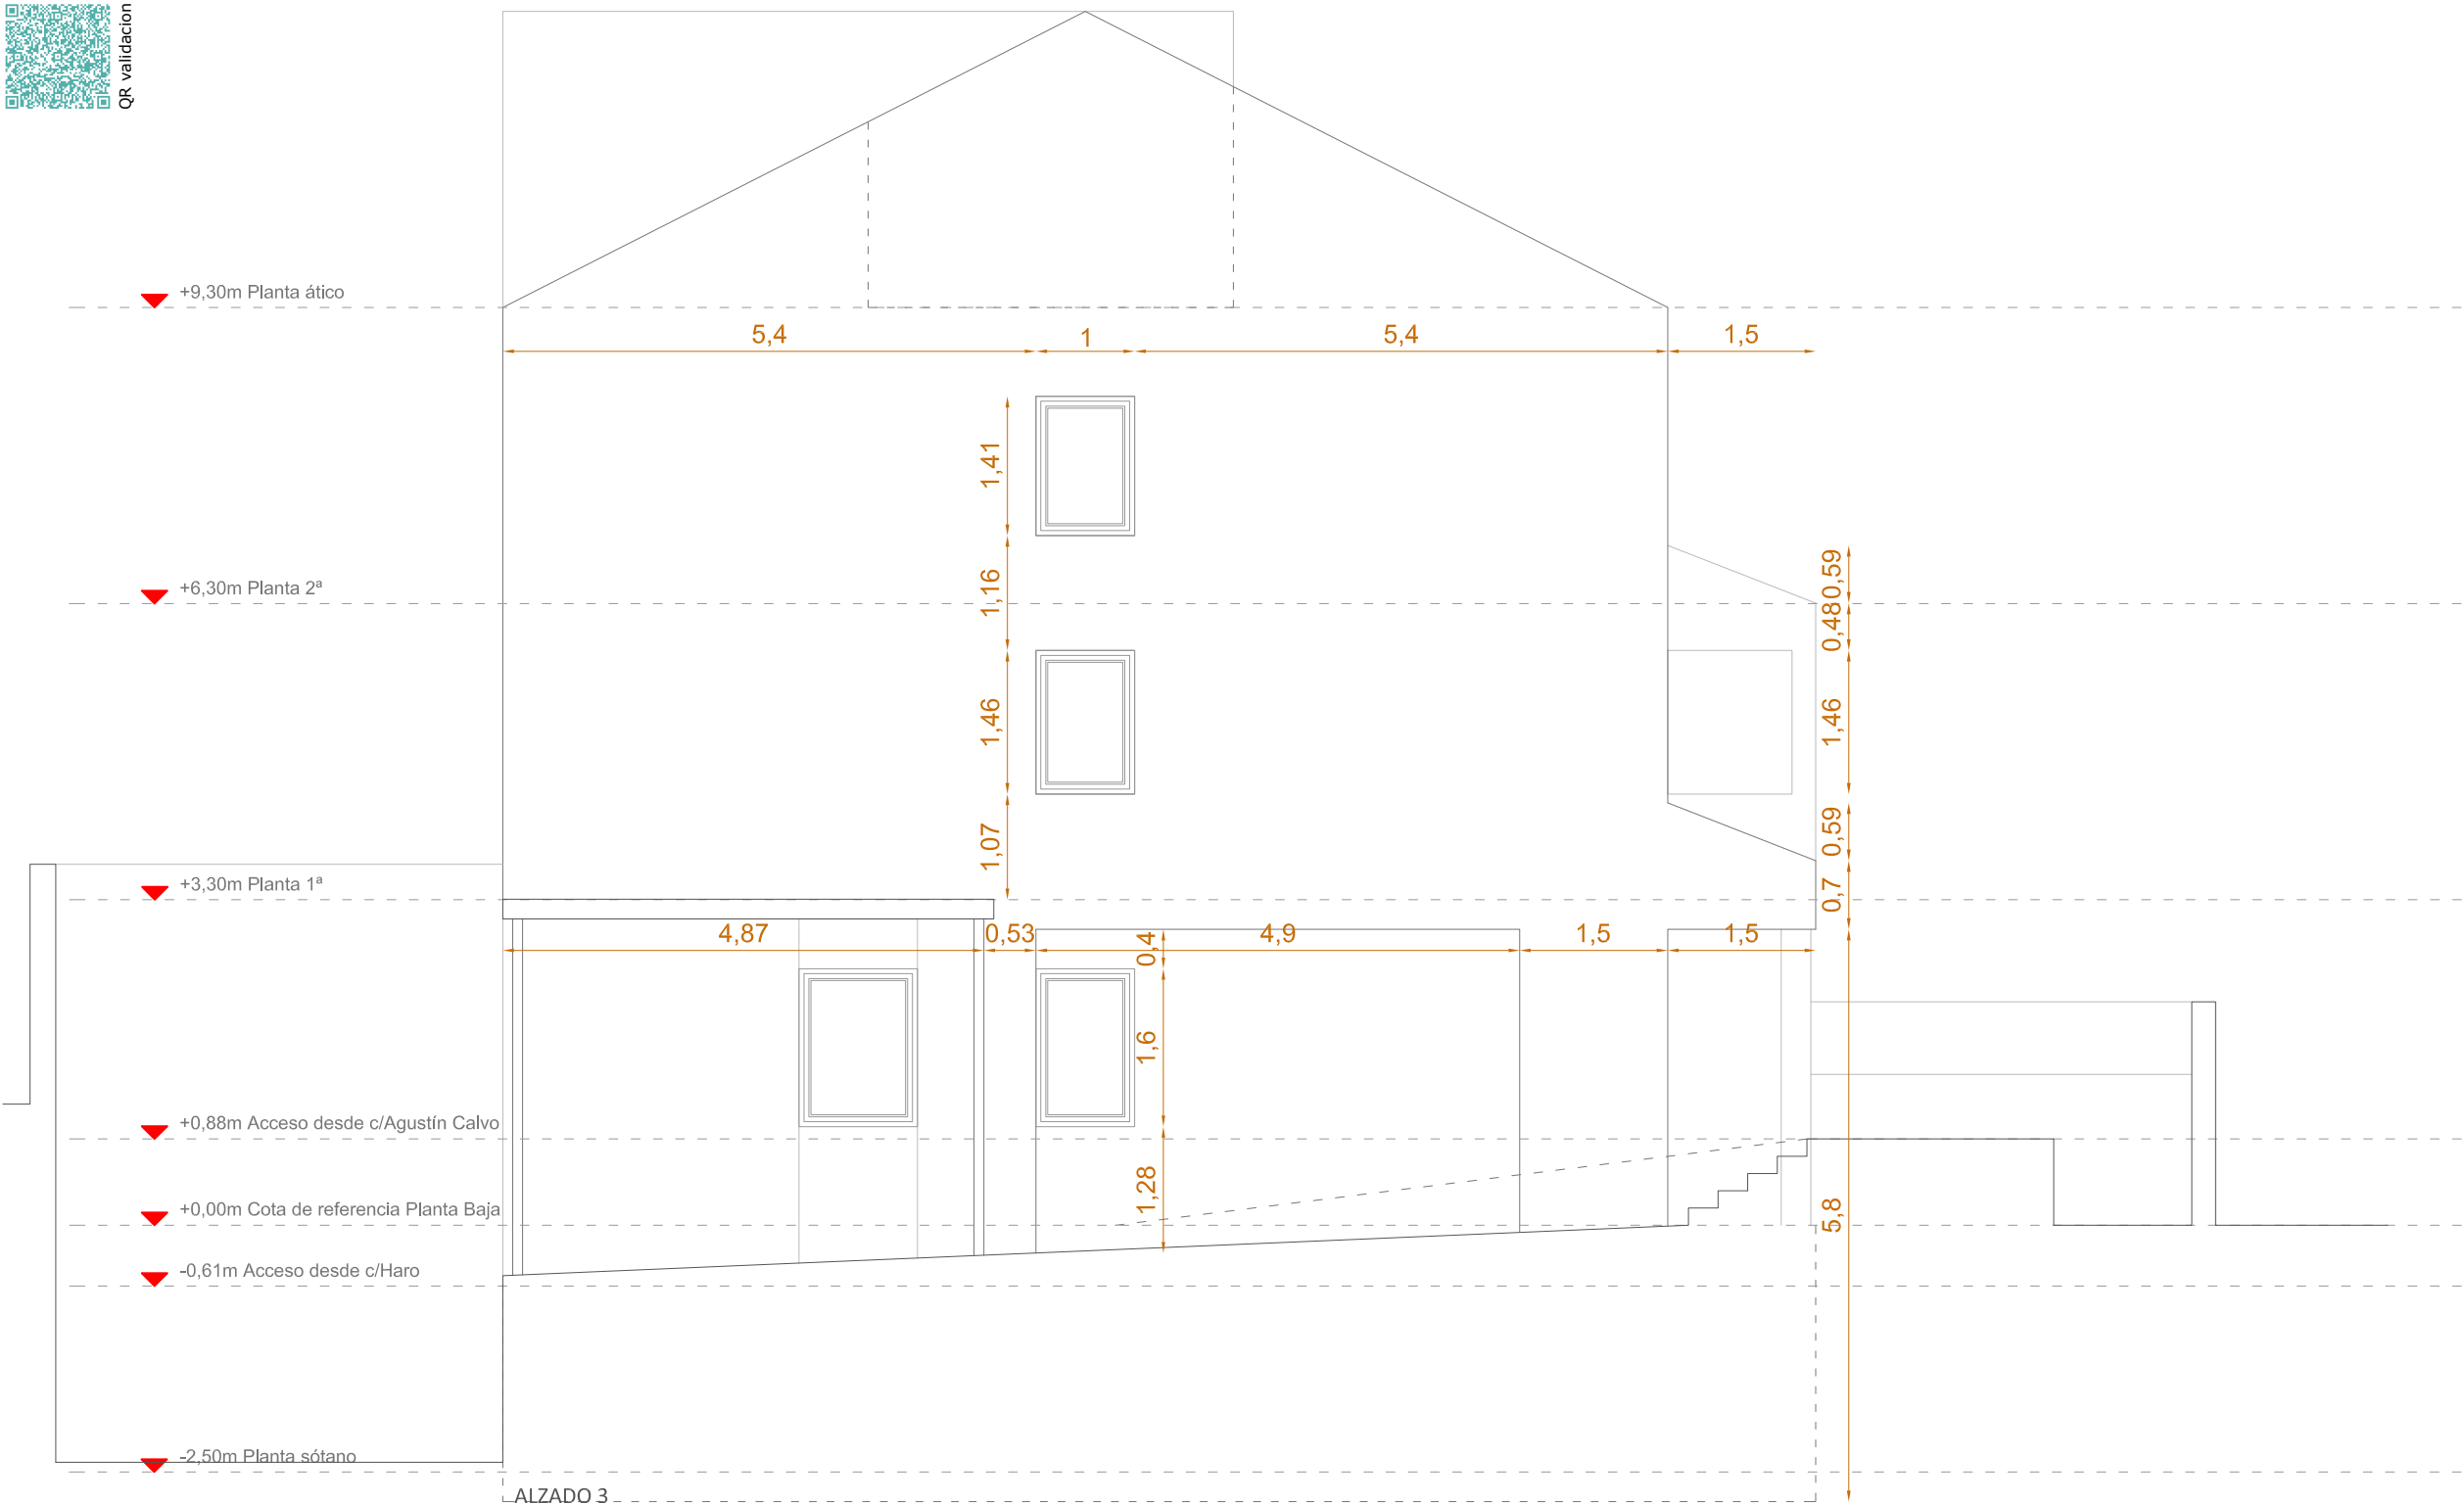

APUNTOARQUITECTURA
teléfono: 6 4 9 6 1 2 4 4 9
www.apuntoarquitectura.com
oficina@apuntoarquitectura.com

PROYECTO
PROYECTO BÁSICO DE OBRAS PARA EL CAMBIO DE
USO DE EDIFICIO RESIDENCIAL A TERCARIO
HOSPEDAJE. LICENCIA DE ACTIVIDAD_
HOTEL DE 2 ESTRELLAS. CI. Haro 5; 28043 Madrid
TITULAR
HARO 5 VENTURES S.L.
N.I.F.: B22599070
REPRESENTANTE
Rafael Garrido Rodrigo
D.N.I.: 00839470Q

TÉCNICO
Jorge Serrano de La Torre
COLEGIADO COAM 17.677

DESCRIPCIÓN
ARQUITECTURA: ALZADOS LATERALES

NÚMERO DE PLANO FECHA ESCALA

A08 17.04.2026 1:75



APUNTOARQUITECTURA
teléfono: 6 49 6 1 2 4 4 9
www.apuntoarquitectura.com
oficina@apuntoarquitectura.com



PROYECTO
PROYECTO BÁSICO DE OBRAS PARA EL CAMBIO DE
USO DE EDIFICIO RESIDENCIAL A TERCARIO
HOSPEDAJE. LICENCIA DE ACTIVIDAD_
HOTEL DE 2 ESTRELLAS. Cl. Haro 5; 28043 Madrid
TITULAR
HARO 5 VENTURES S.L.
N.I.F.: B22599070
REPRESENTANTE
Rafael Garrido Rodrigo
D.N.I.: 00839470Q

TÉCNICO
Jorge Serrano de La Torre
COLEGIADO COAM 17.677
DESCRIPCIÓN
EMPLAZAMIENTO REFORMADO


NÚMERO DE PLANO
A09
FECHA
17.04.2026
ESCALA
1:100



QR validacion

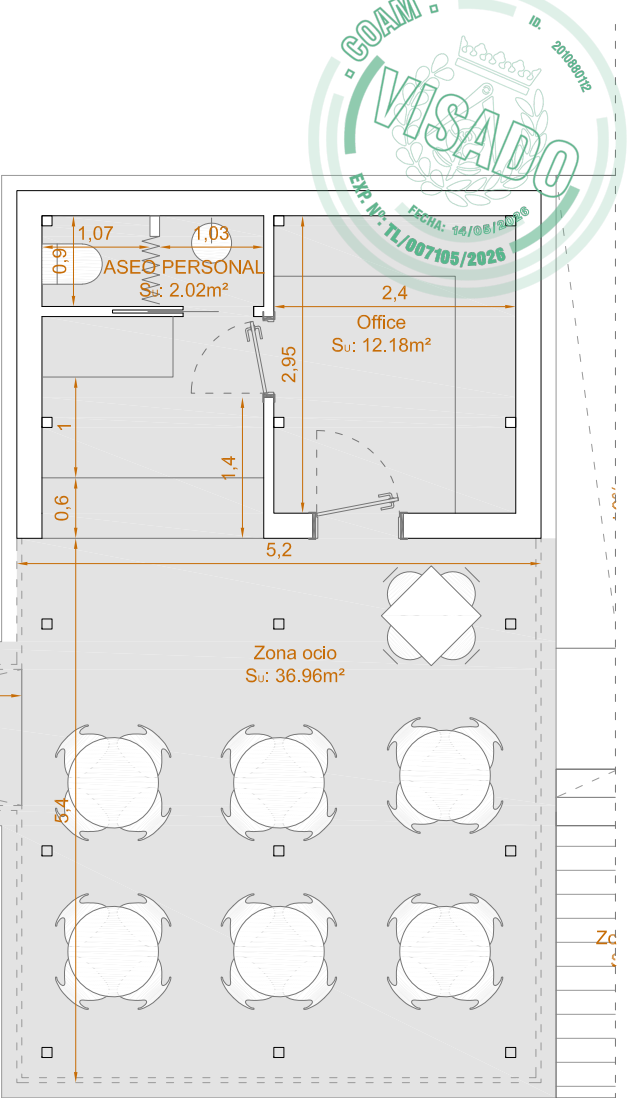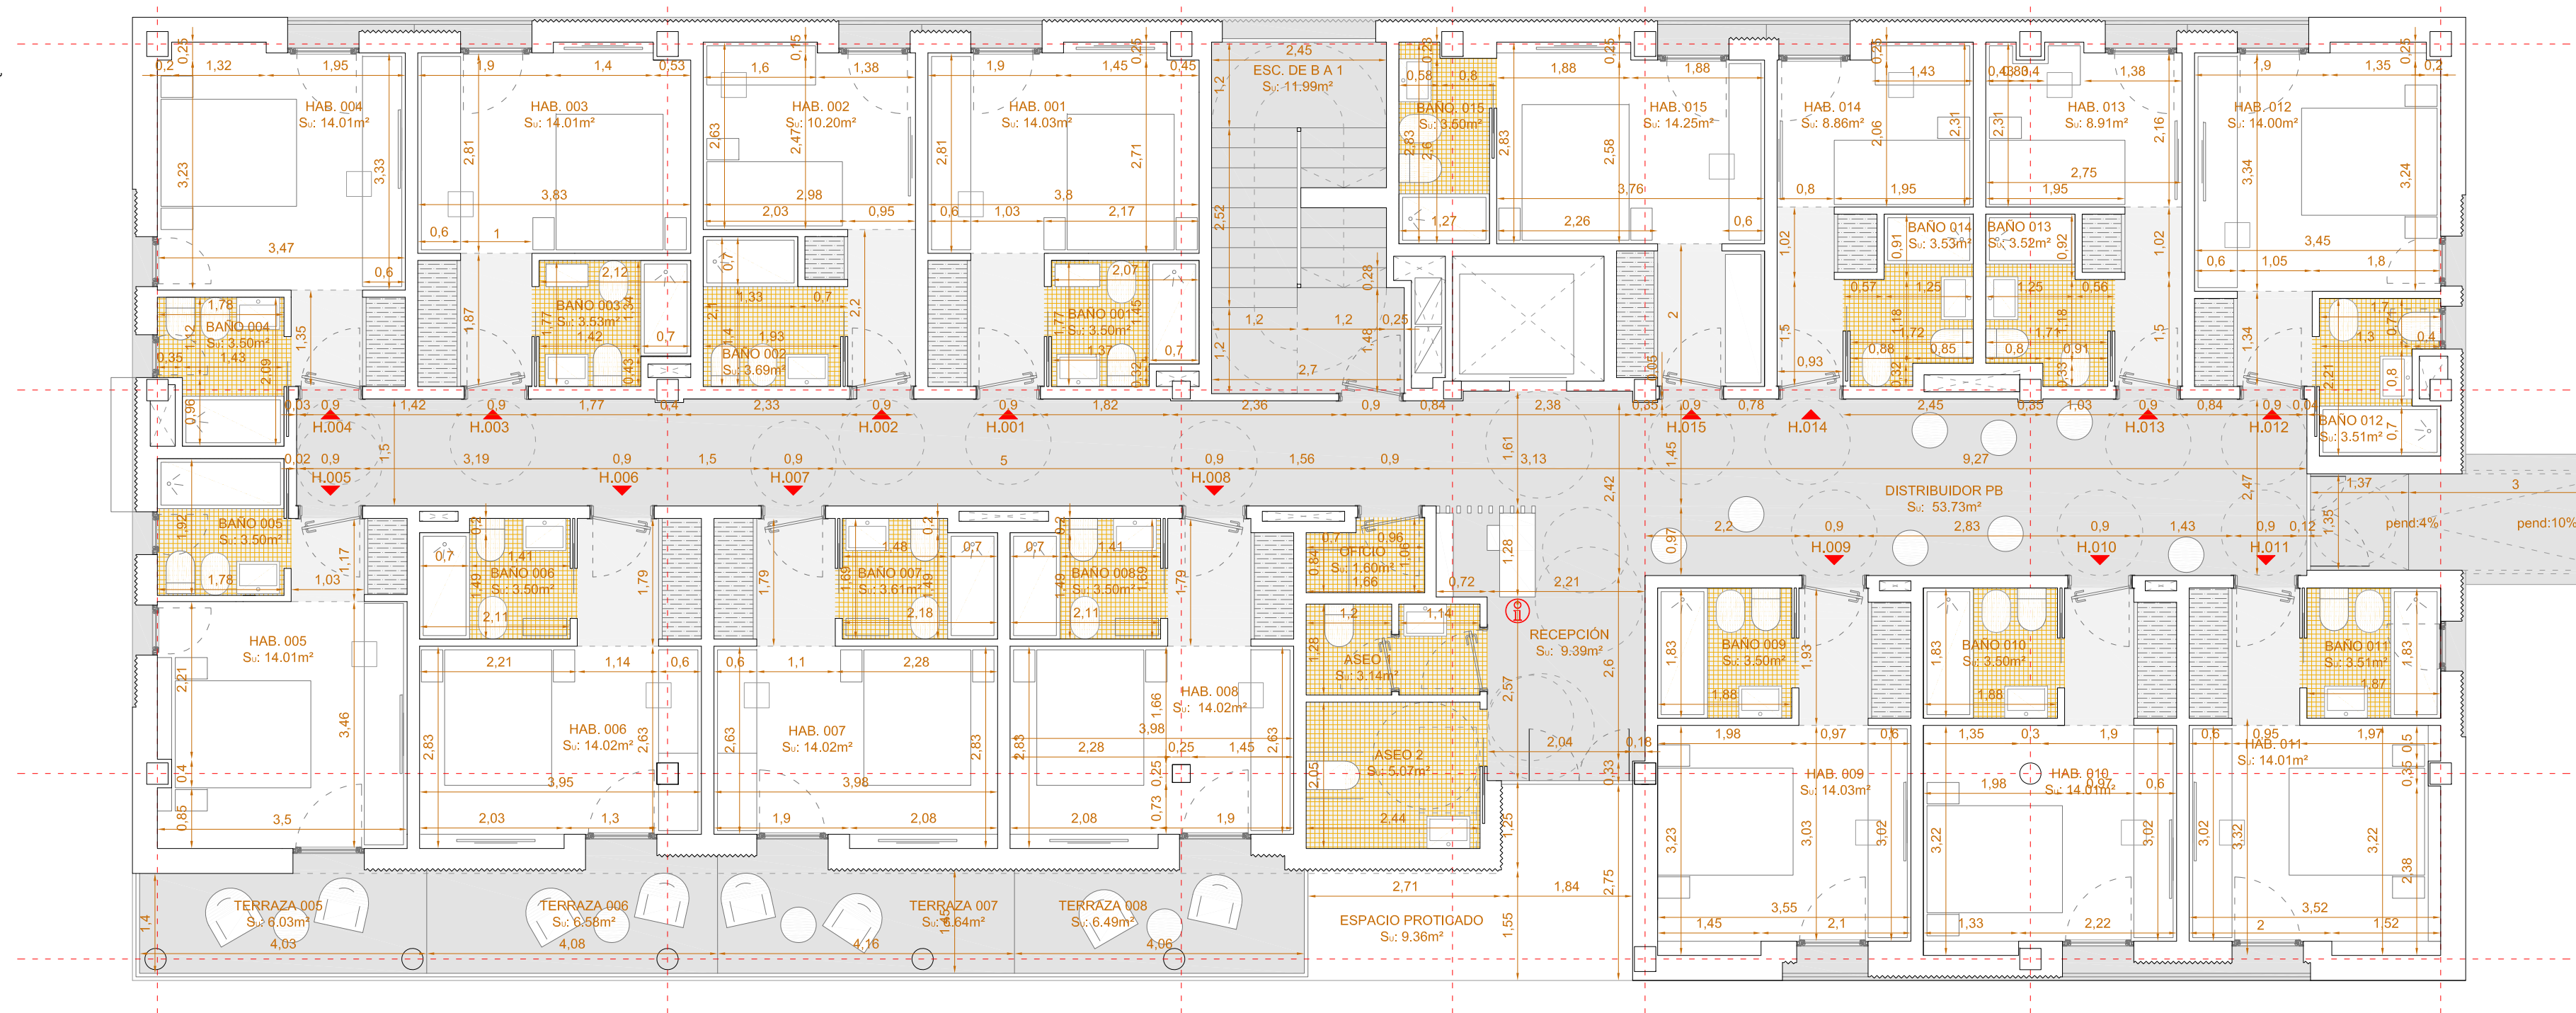

PLANTA BAJA

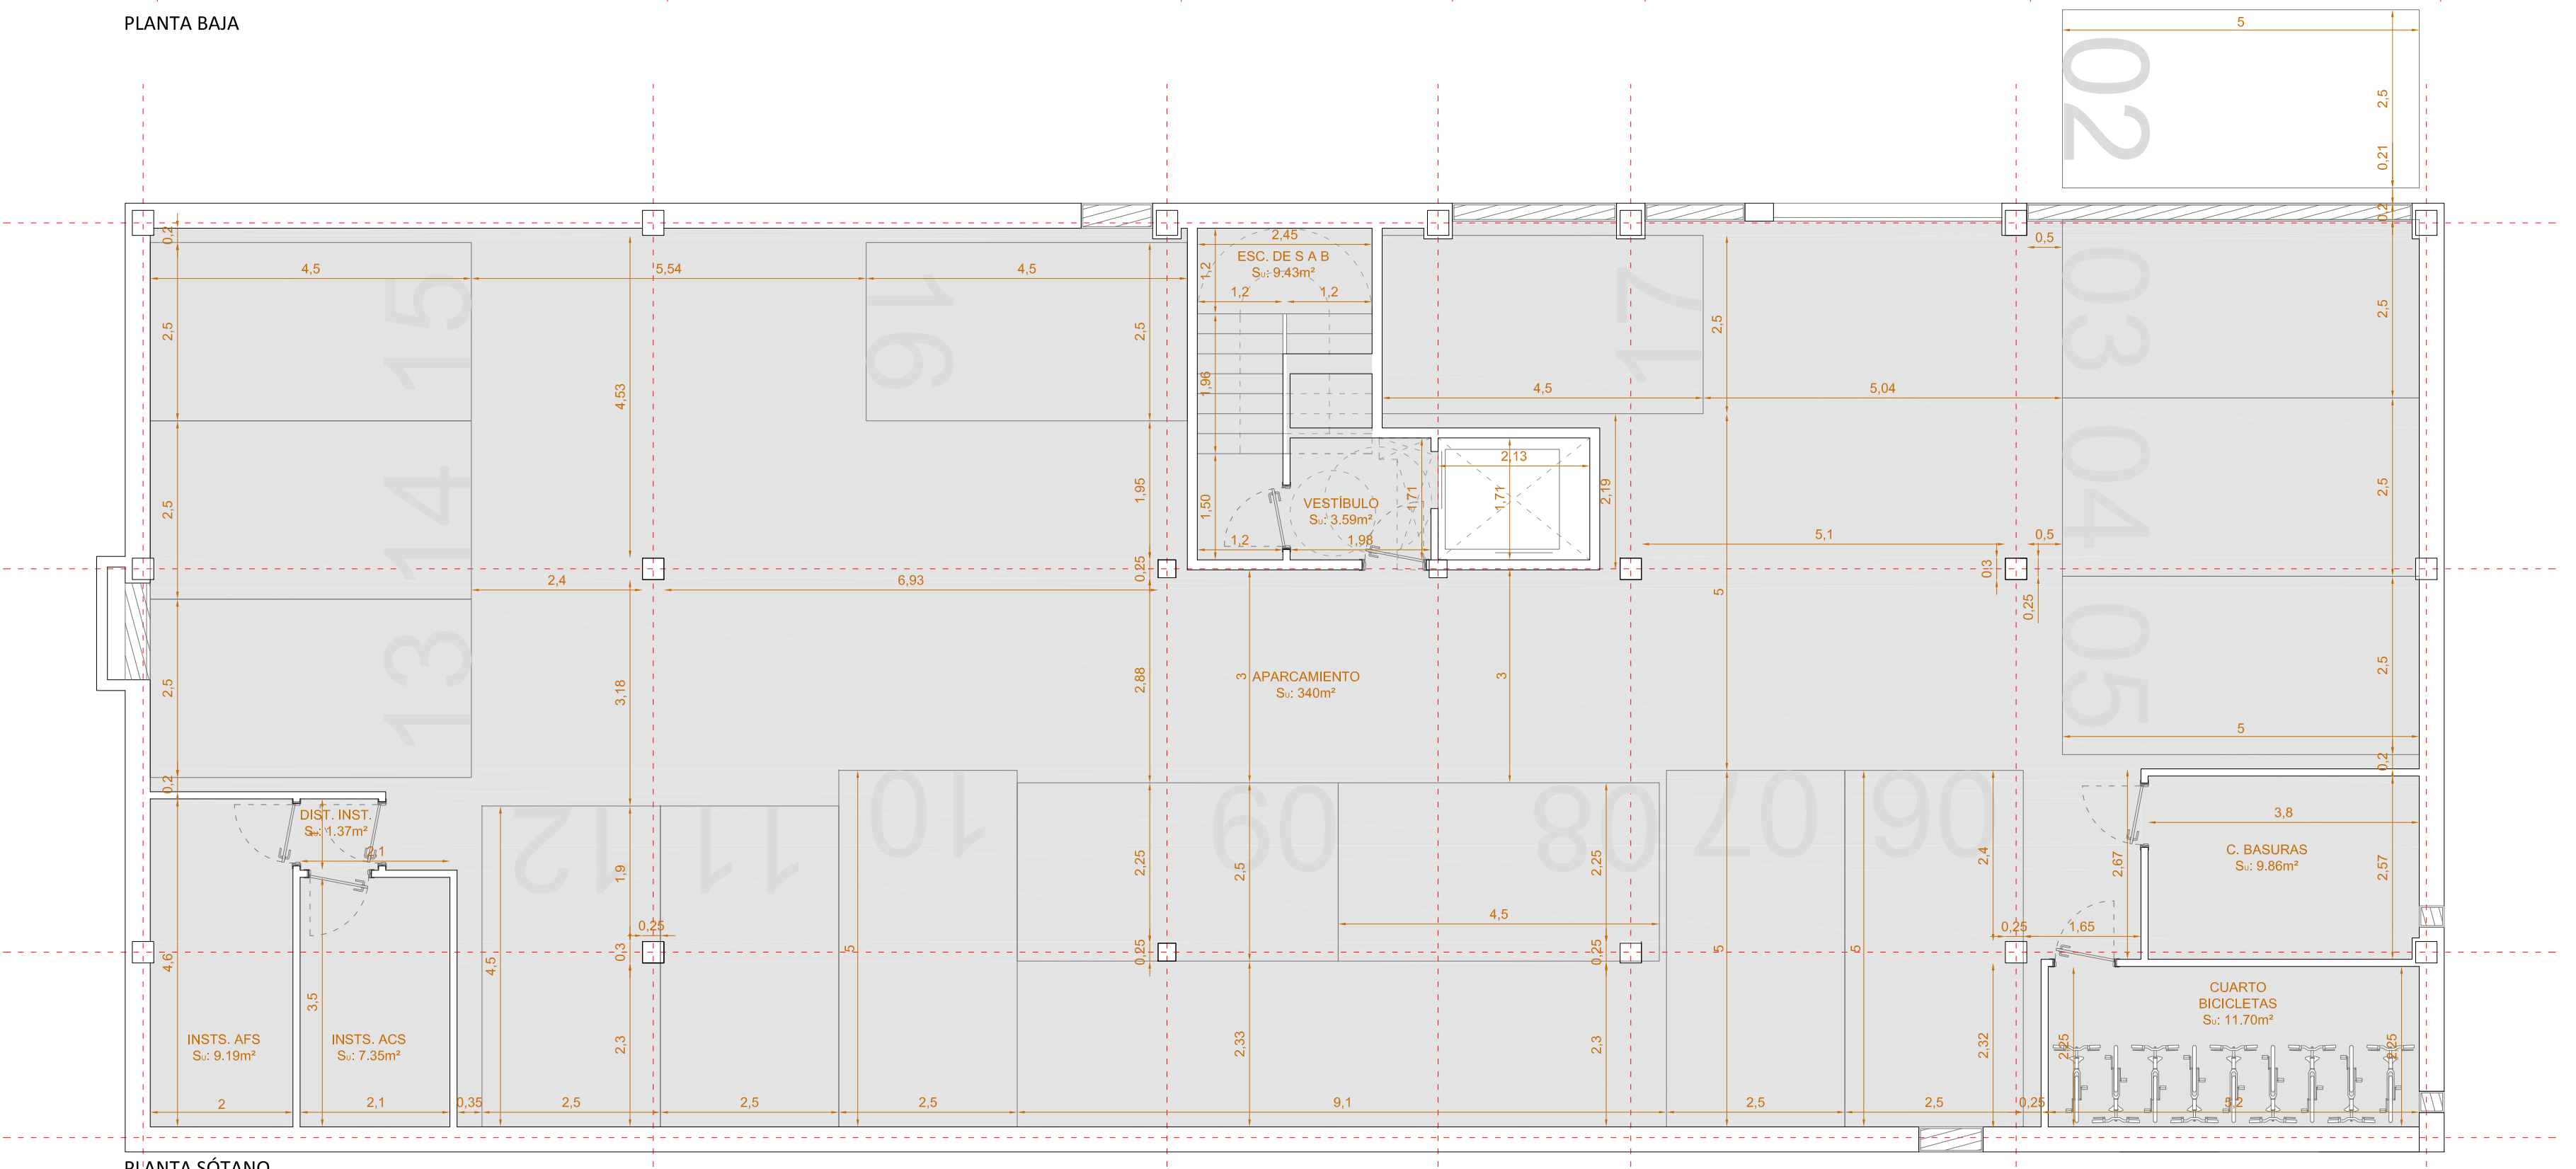

PLANTA SÓTANO

0 1 5m

APUNTOARQUITECTURA
teléfono: 649612449
www.apuntoarquitectura.com
oficina@apuntoarquitectura.com

PROYECTO
PROYECTO BÁSICO DE OBRAS PARA EL CAMBIO DE
USO DE EDIFICIO RESIDENCIAL A TERCARIO
HOSPEDAJE. LICENCIA DE ACTIVIDAD
HOTEL DE 2 ESTRELLAS. CI. Haro 5; 28043 Madrid


TITULAR
HARO 5 VENTURES S.L.
N.I.F.: B22599070
REPRESENTANTE
Rafael Garrido Rodrigo
D.N.I.: 00839470Q

TÉCNICO
Jorge Serrano de La Torre
COLEGIADO COAM 17.677


DESCRIPCIÓN
ARQ. REFORMADO: PLANTA SÓTANO Y BAJA

NÚMERO DE PLANO FECHA ESCALA

A10 17.04.2026 1:75

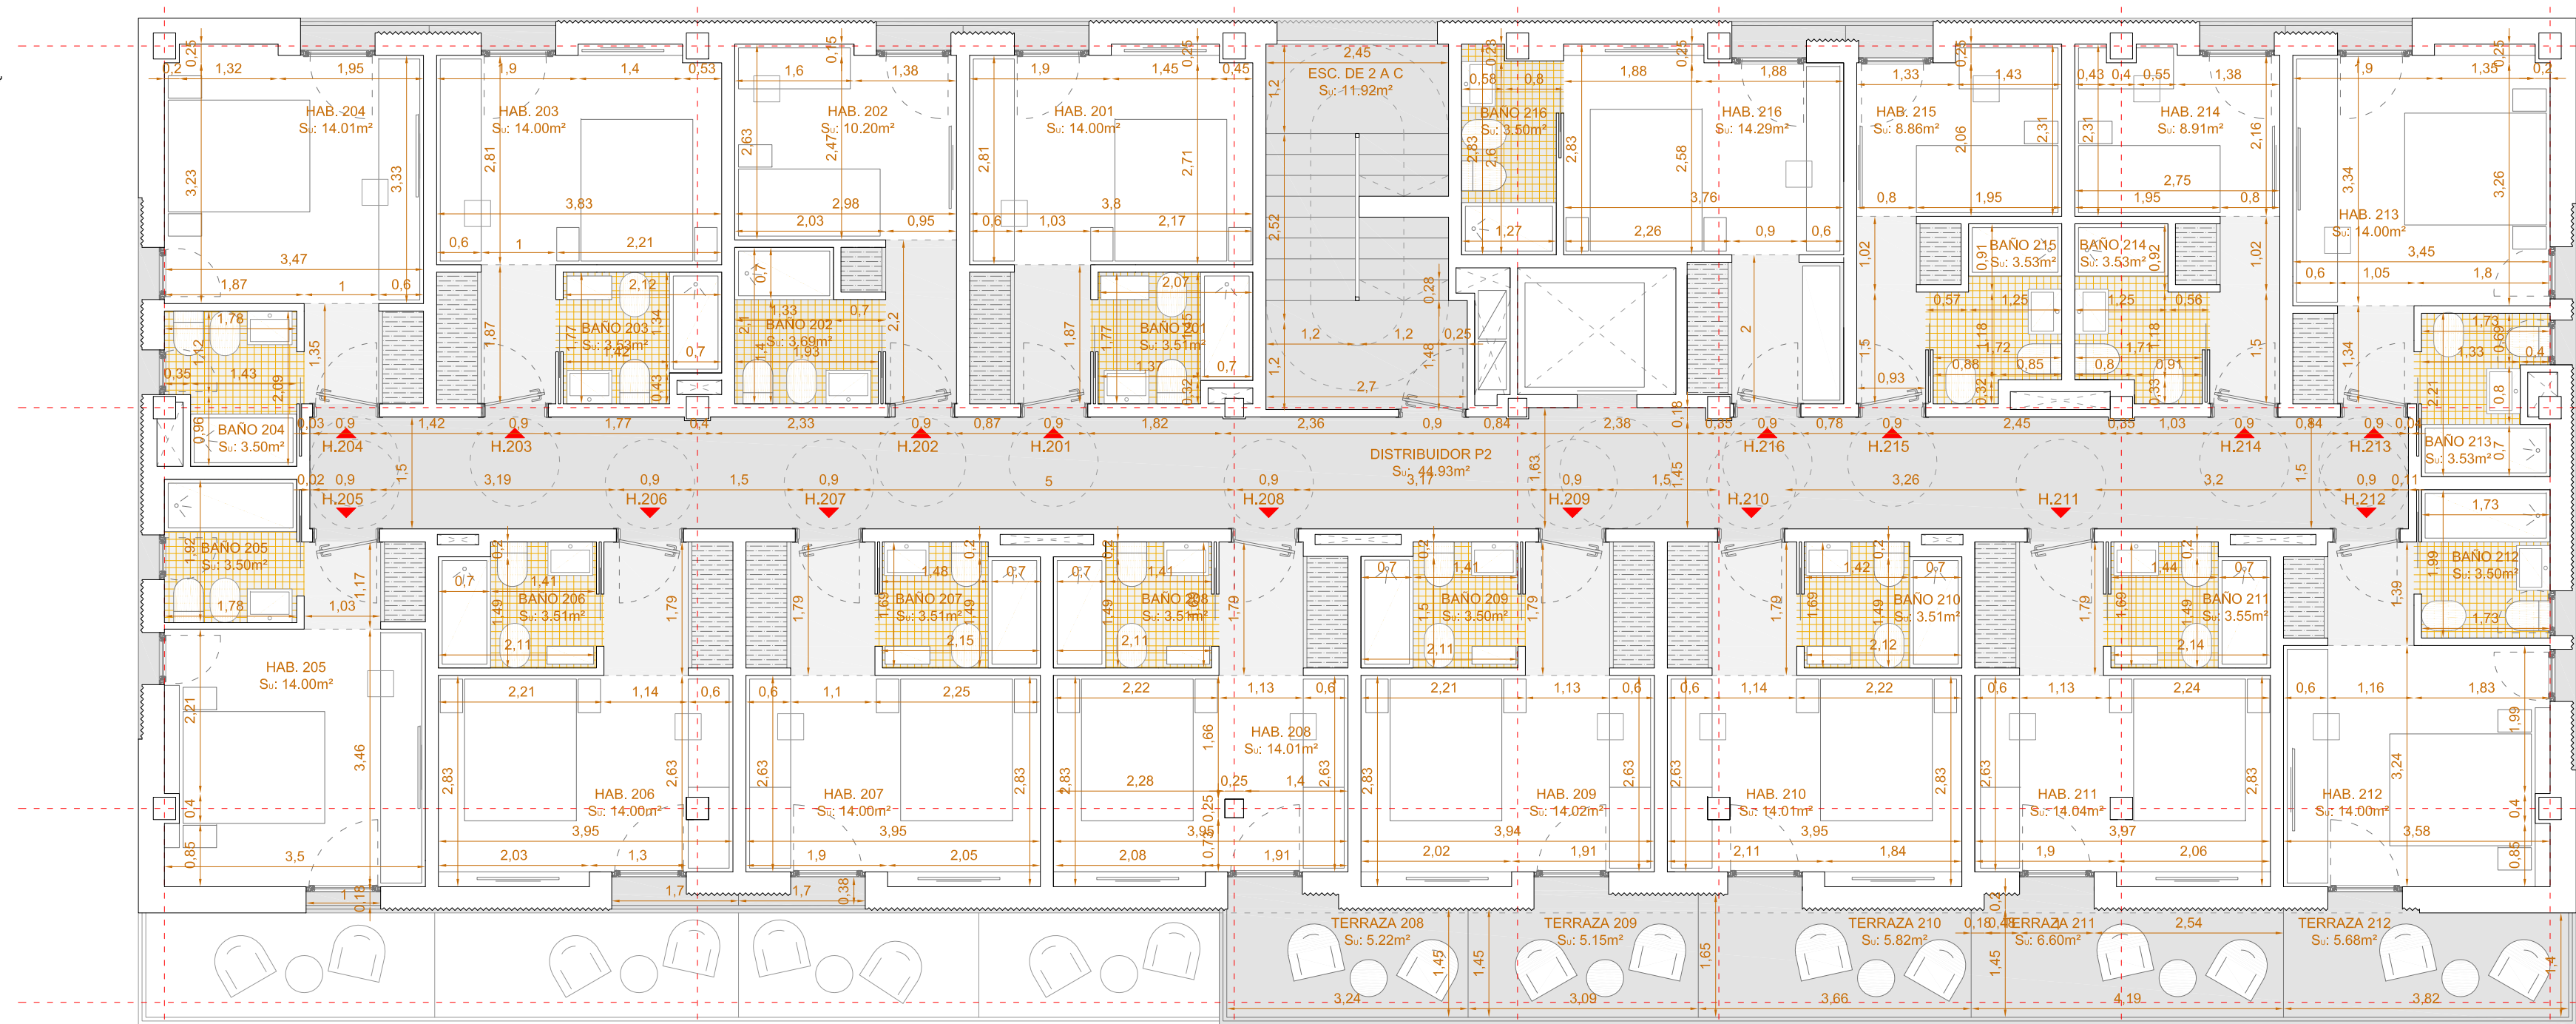

PLANTA SEGUNDA

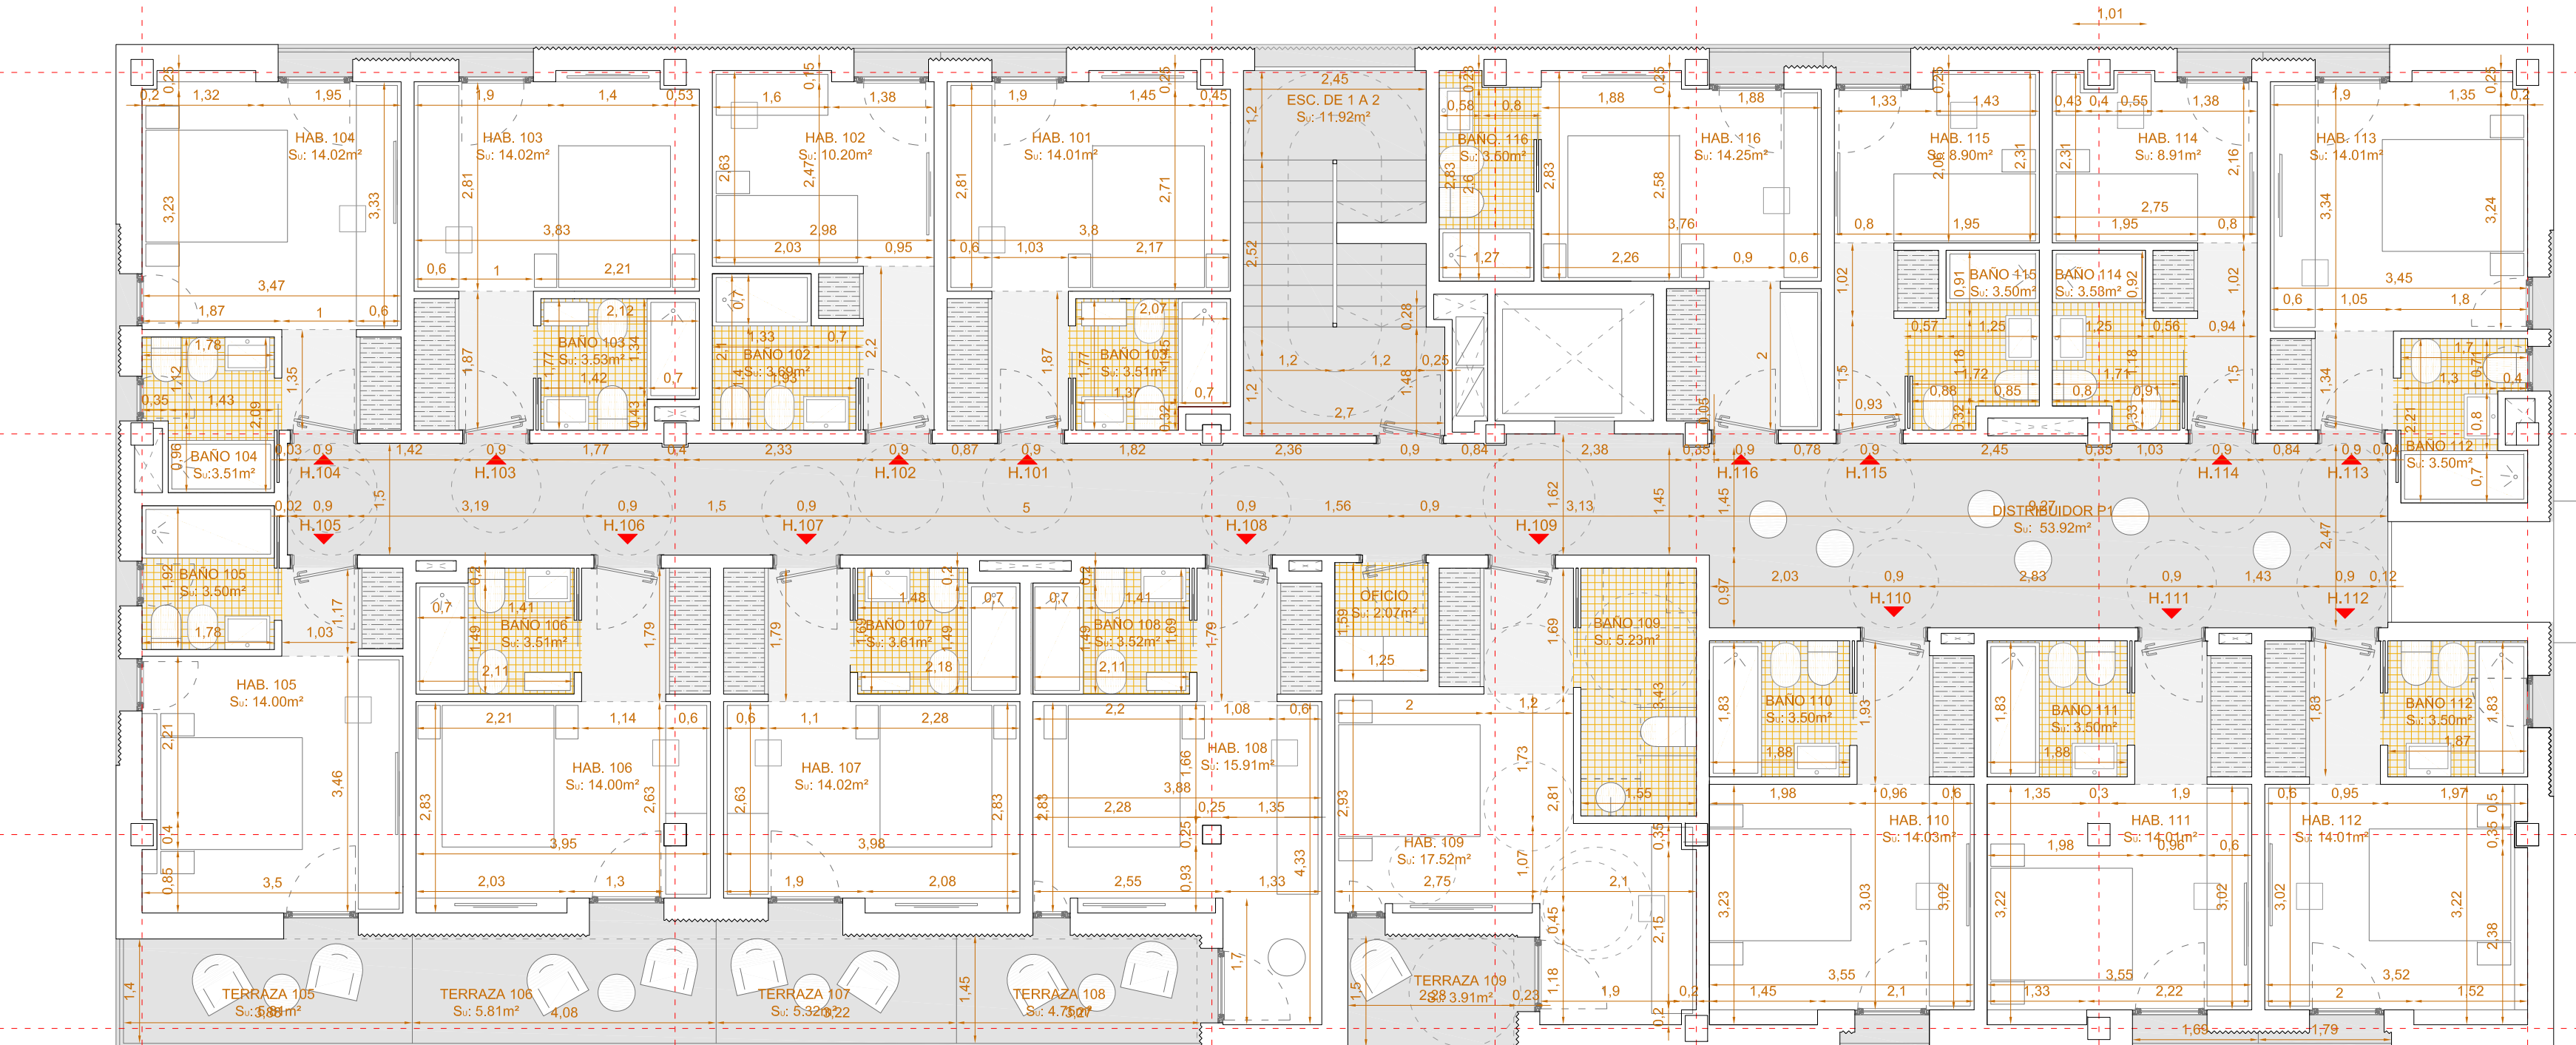

PLANTA PRIMERA

015m

APUNTOARQUITECTURA

teléfono: 649612449

www.apuntoarquitectura.com

oficina@apuntoarquitectura.com

PROYECTO

PROYECTO BÁSICO DE OBRAS PARA EL CAMBIO DE

USO DE EDIFICIO RESIDENCIAL A TERCIARIO

HOSPEDAJE. LICENCIA DE ACTIVIDAD

HOTEL DE 2 ESTRELLAS. CI. Haro 5; 28043 Madrid

TITULAR

HARO 5 VENTURES S.L.

N.I.F.: B22599070

REPRESENTANTE

Rafael Garrido Rodrigo

D.N.I.: 00839470Q

TÉCNICO

Jorge Serrano de La Torre

COLEGIADO COAM 17.677

DESCRIPCIÓN

ARQ. REFORMADO: PLANTA PRIMERA Y SEGUNDA

NÚMERO DE PLANO

FECHA

ESCALA


A11

17.04.2026


1:75



QR validation

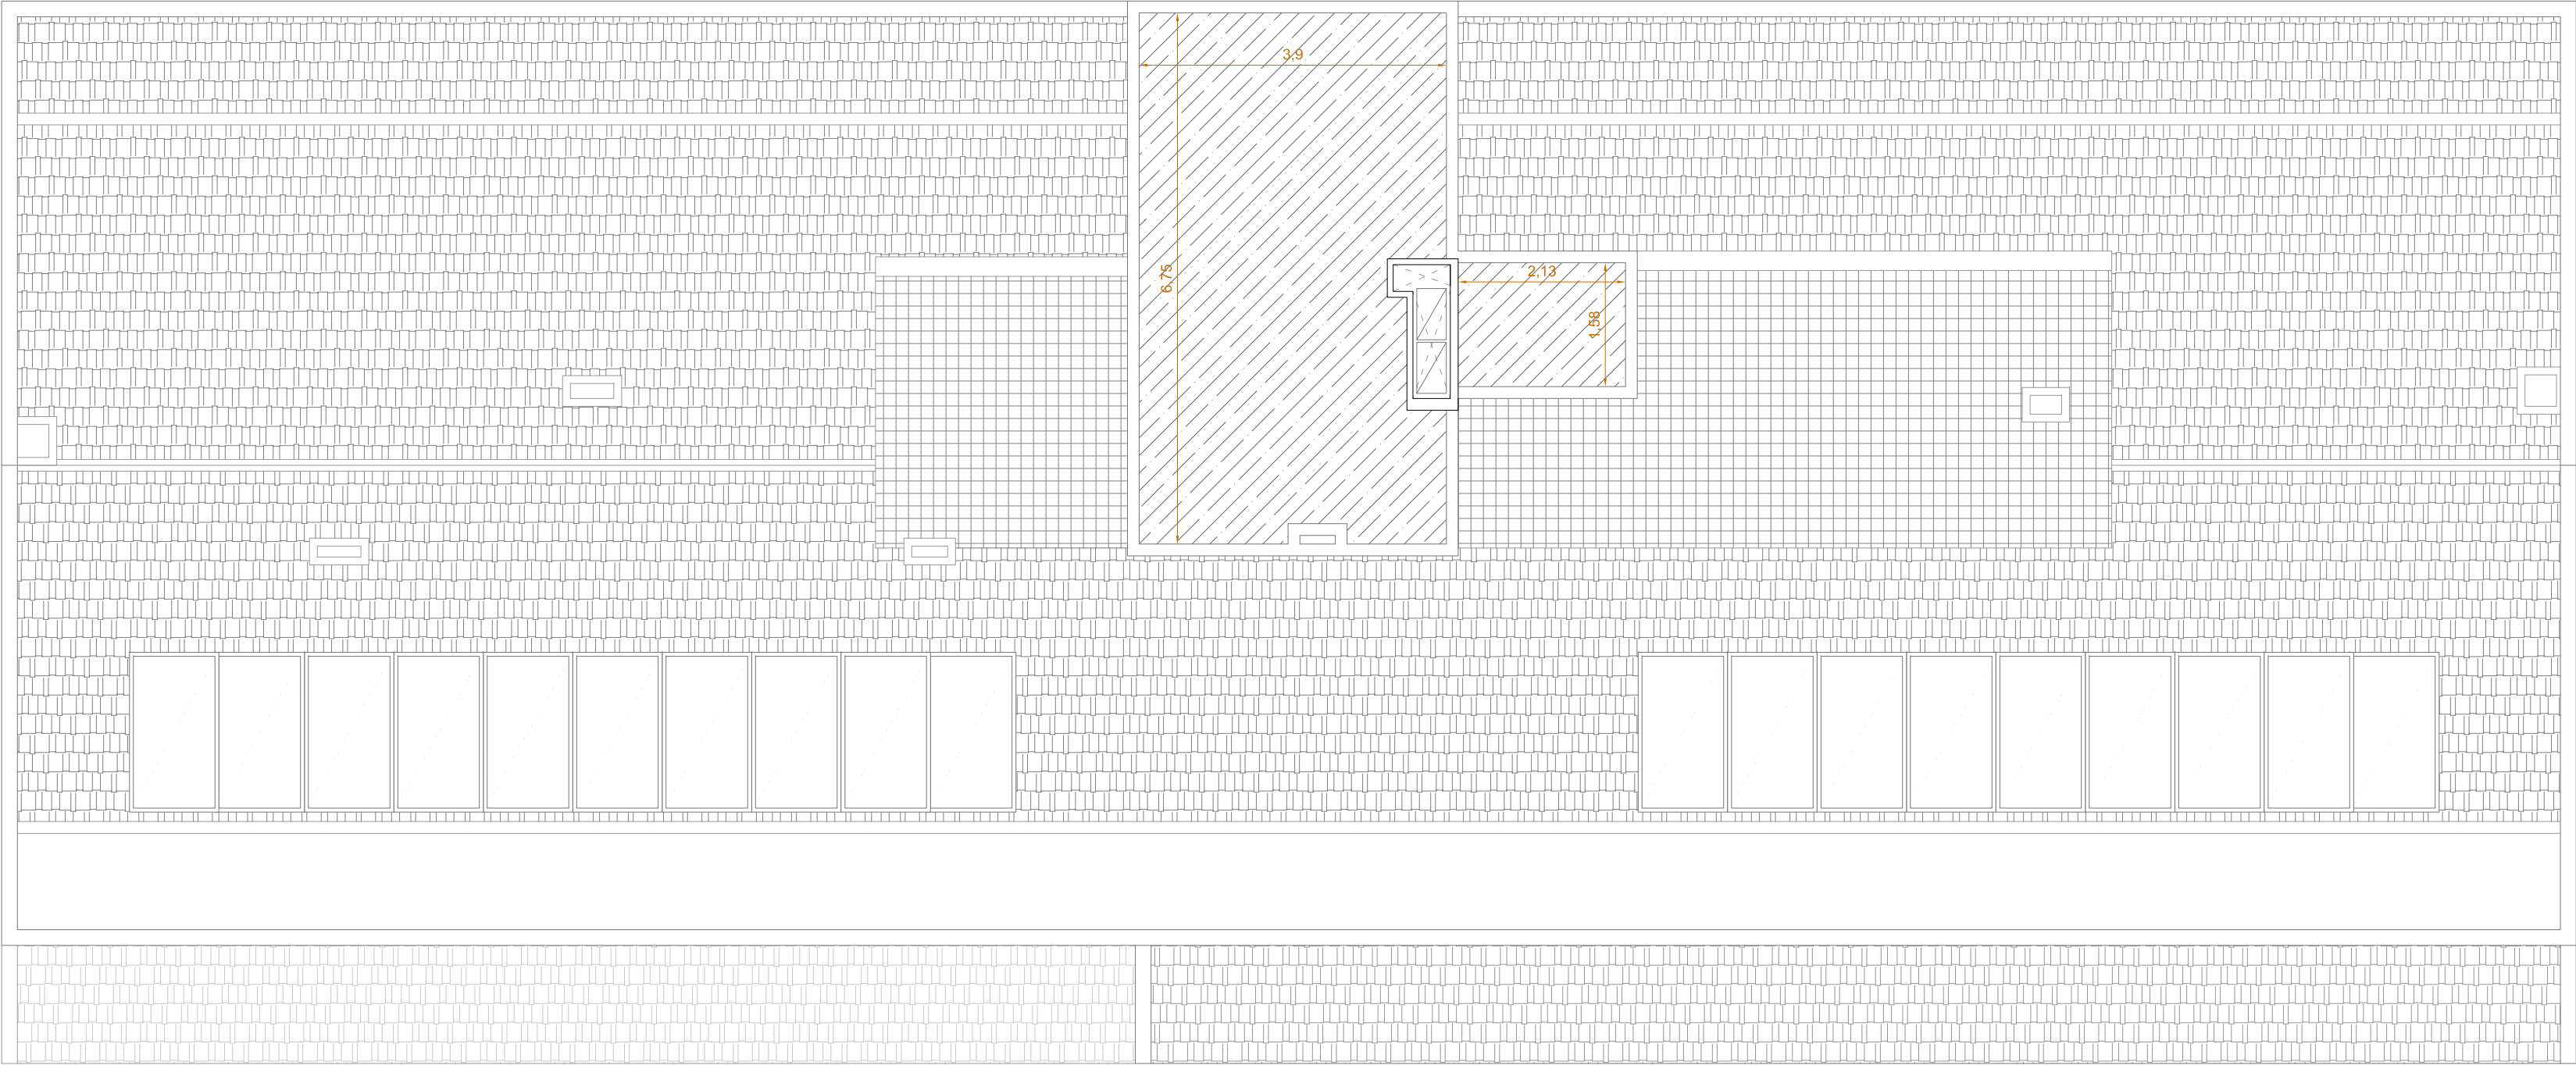

PLANTA CUBIERTA

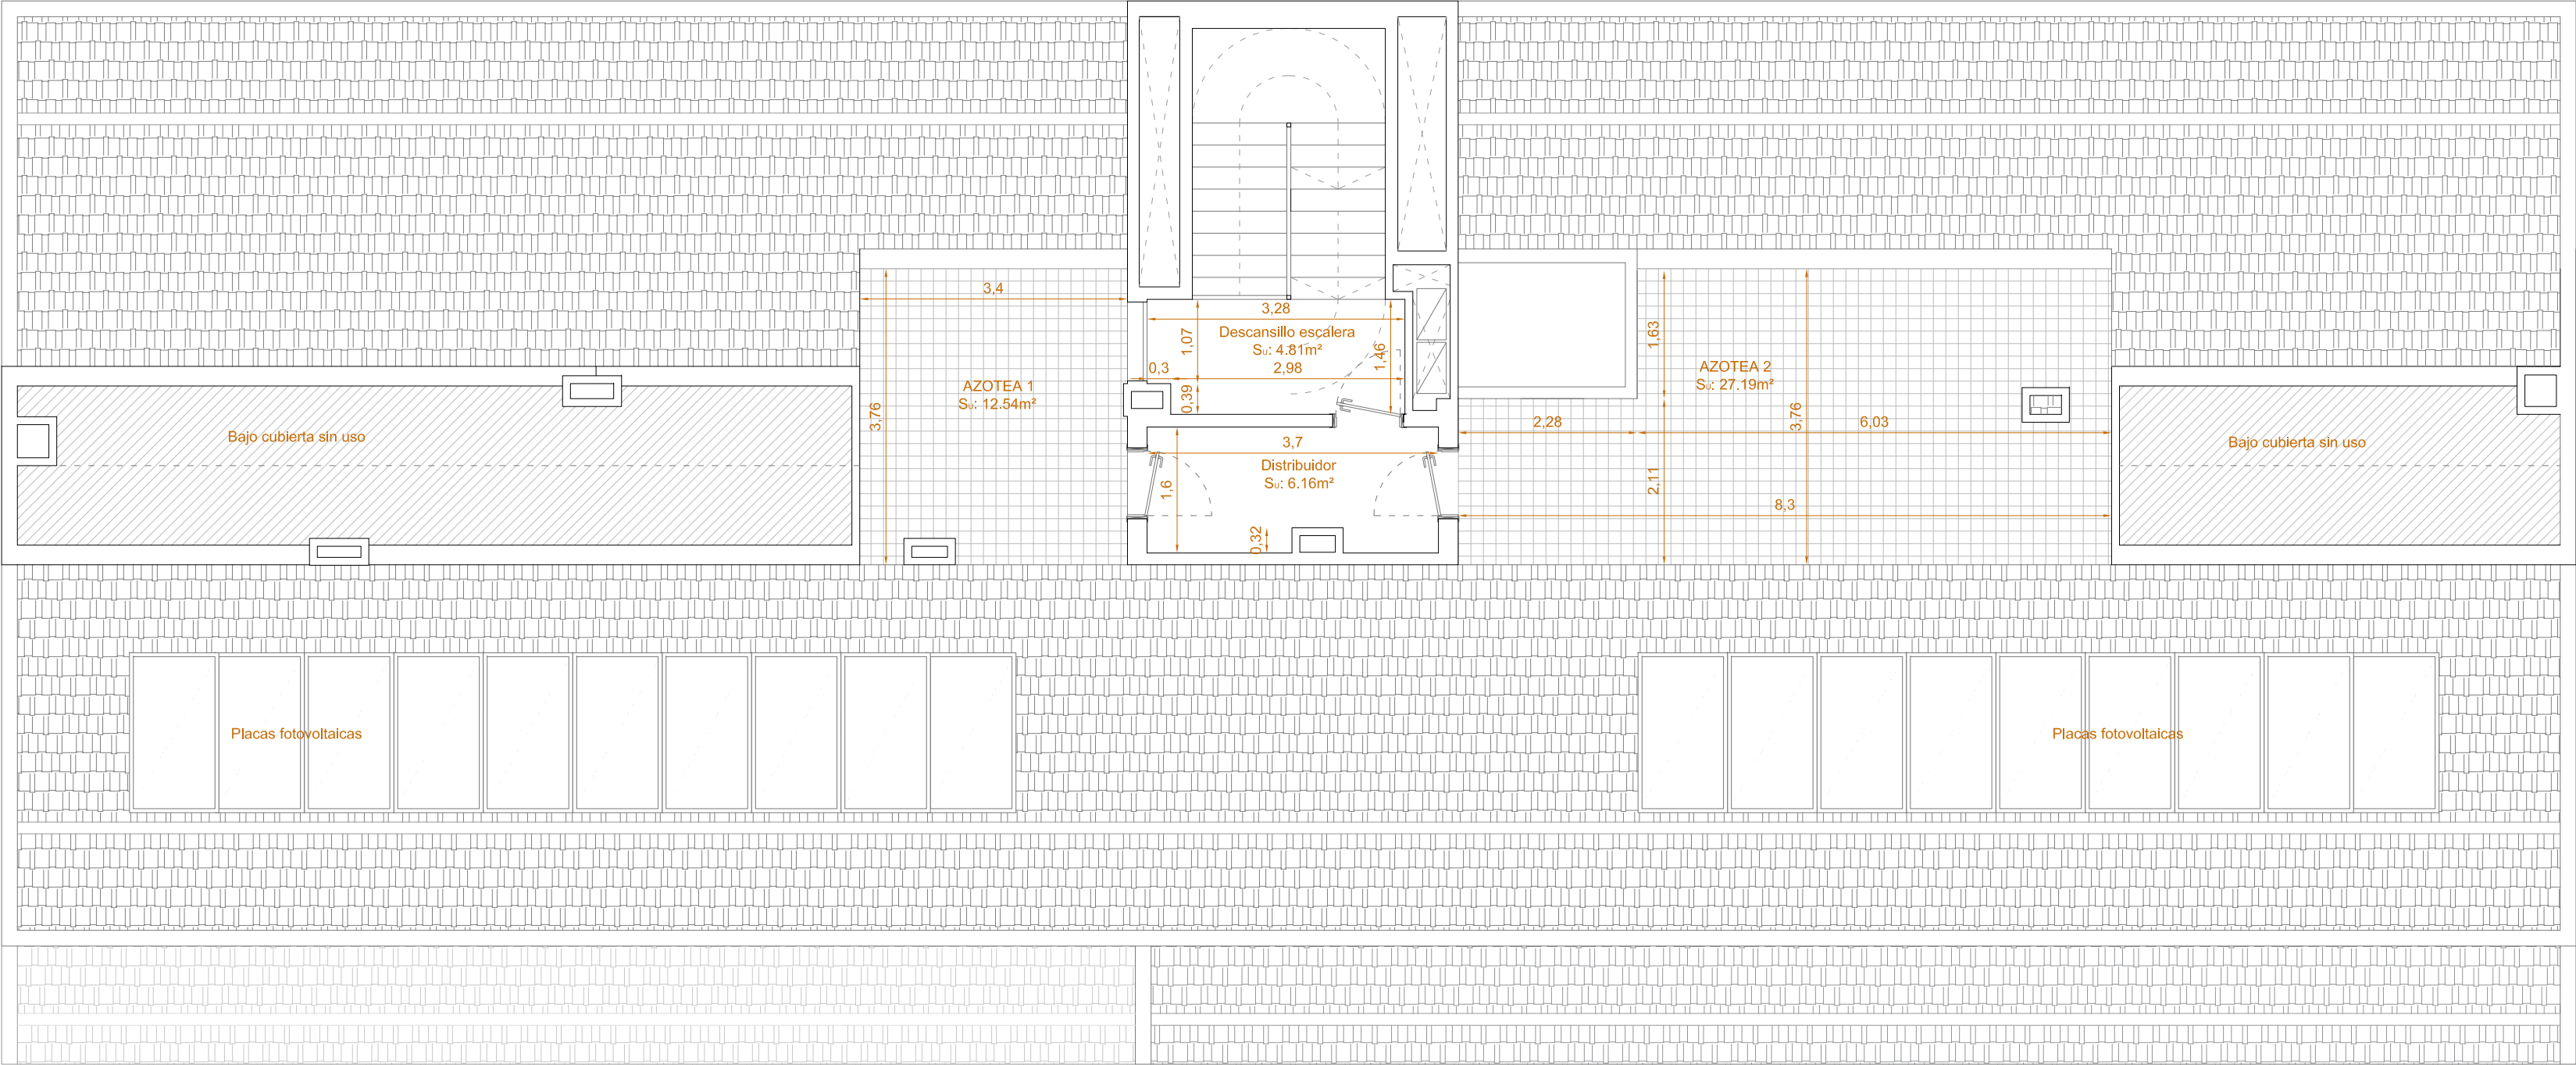

PLANTA BAJO CUBIERTA



APUNTOARQUITECTURA
teléfono: 6 4 9 6 1 2 4 4 9
www.apuntoarquitectura.com
oficina@apuntoarquitectura.com


PROYECTO
PROYECTO BÁSICO DE OBRAS PARA EL CAMBIO DE
USO DE EDIFICIO RESIDENCIAL A TERCIARIO
HOSPEDAJE. LICENCIA DE ACTIVIDAD.
HOTEL DE 2 ESTRELLAS. Cl. Haro 5; 28043 Madrid
TITULAR
HARO 5 VENTURES S.L.
N.I.F.: B22599070
REPRESENTANTE
Rafael Garrido Rodrigo
D.N.I.: 00839470Q

TÉCNICO
Jorge Serrano de La Torre
COLEGIADO COAM 17.677
DESCRIPCIÓN


ARQ. REFORMADO: PLANTA BAJO CUB Y CUBIERTA

NÚMERO DE PLANO FECHA ESCALA


A12 17.04.2026 1:75

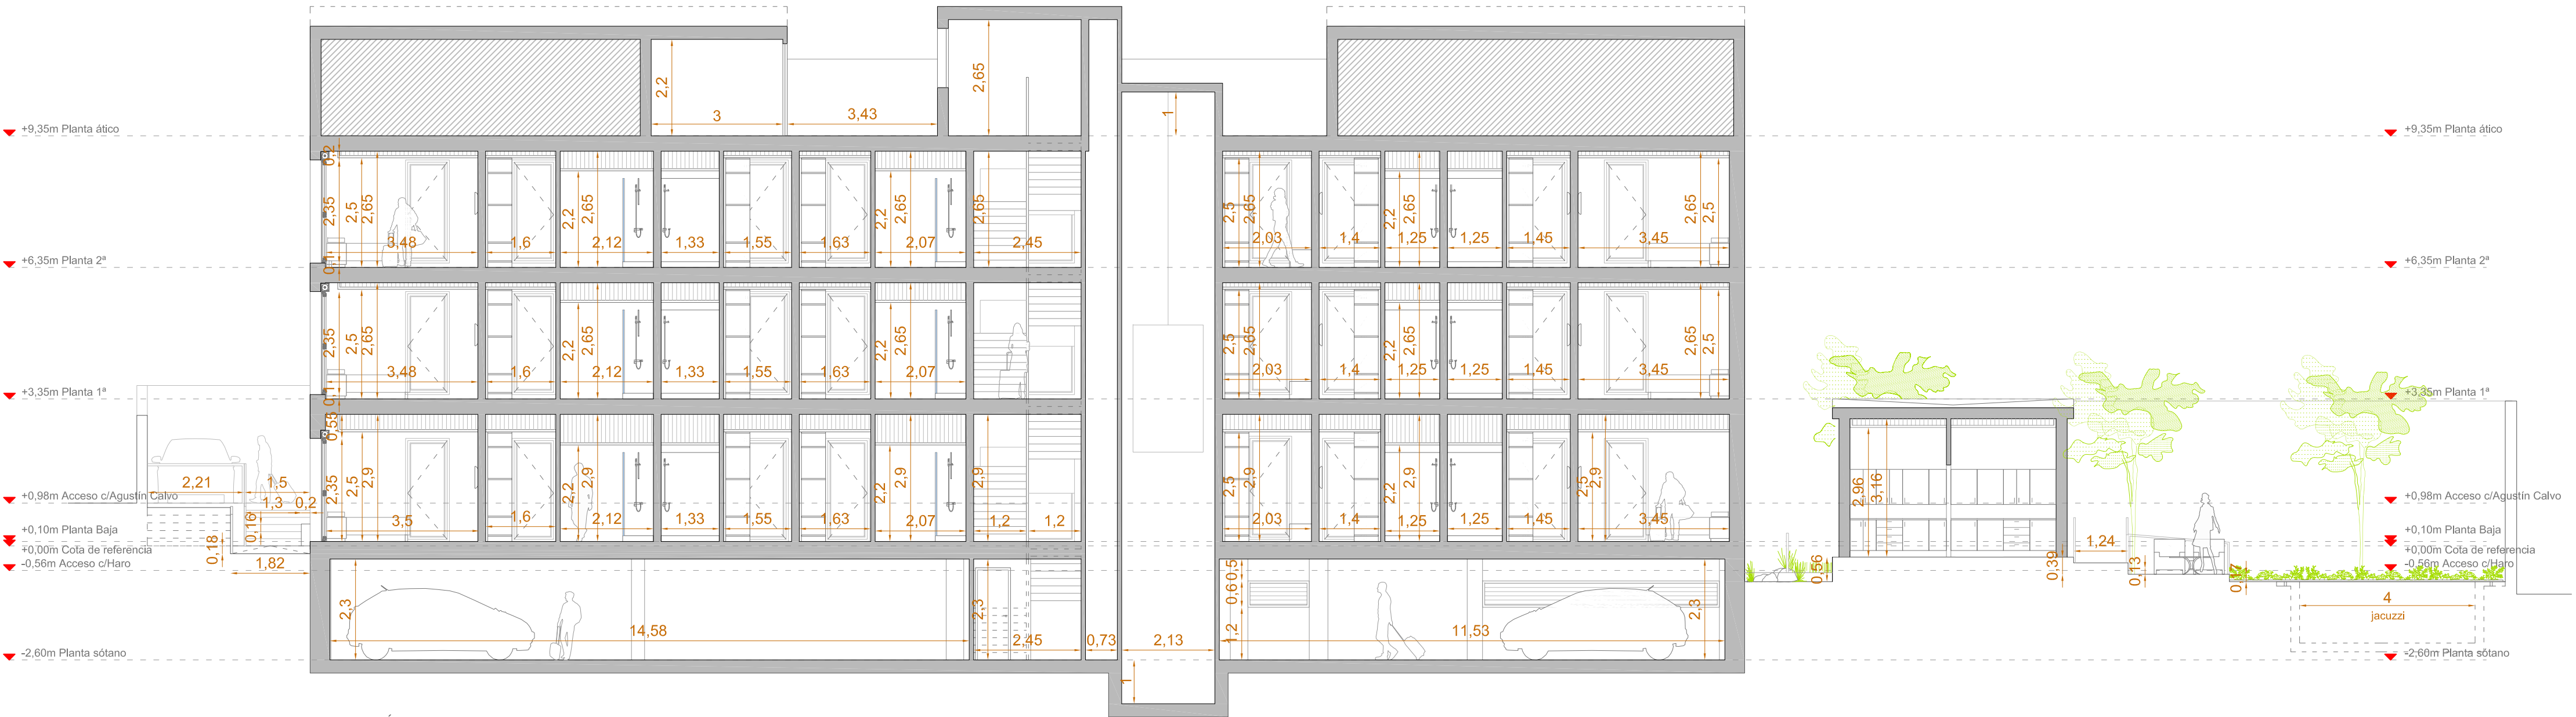

SECCIÓN 1

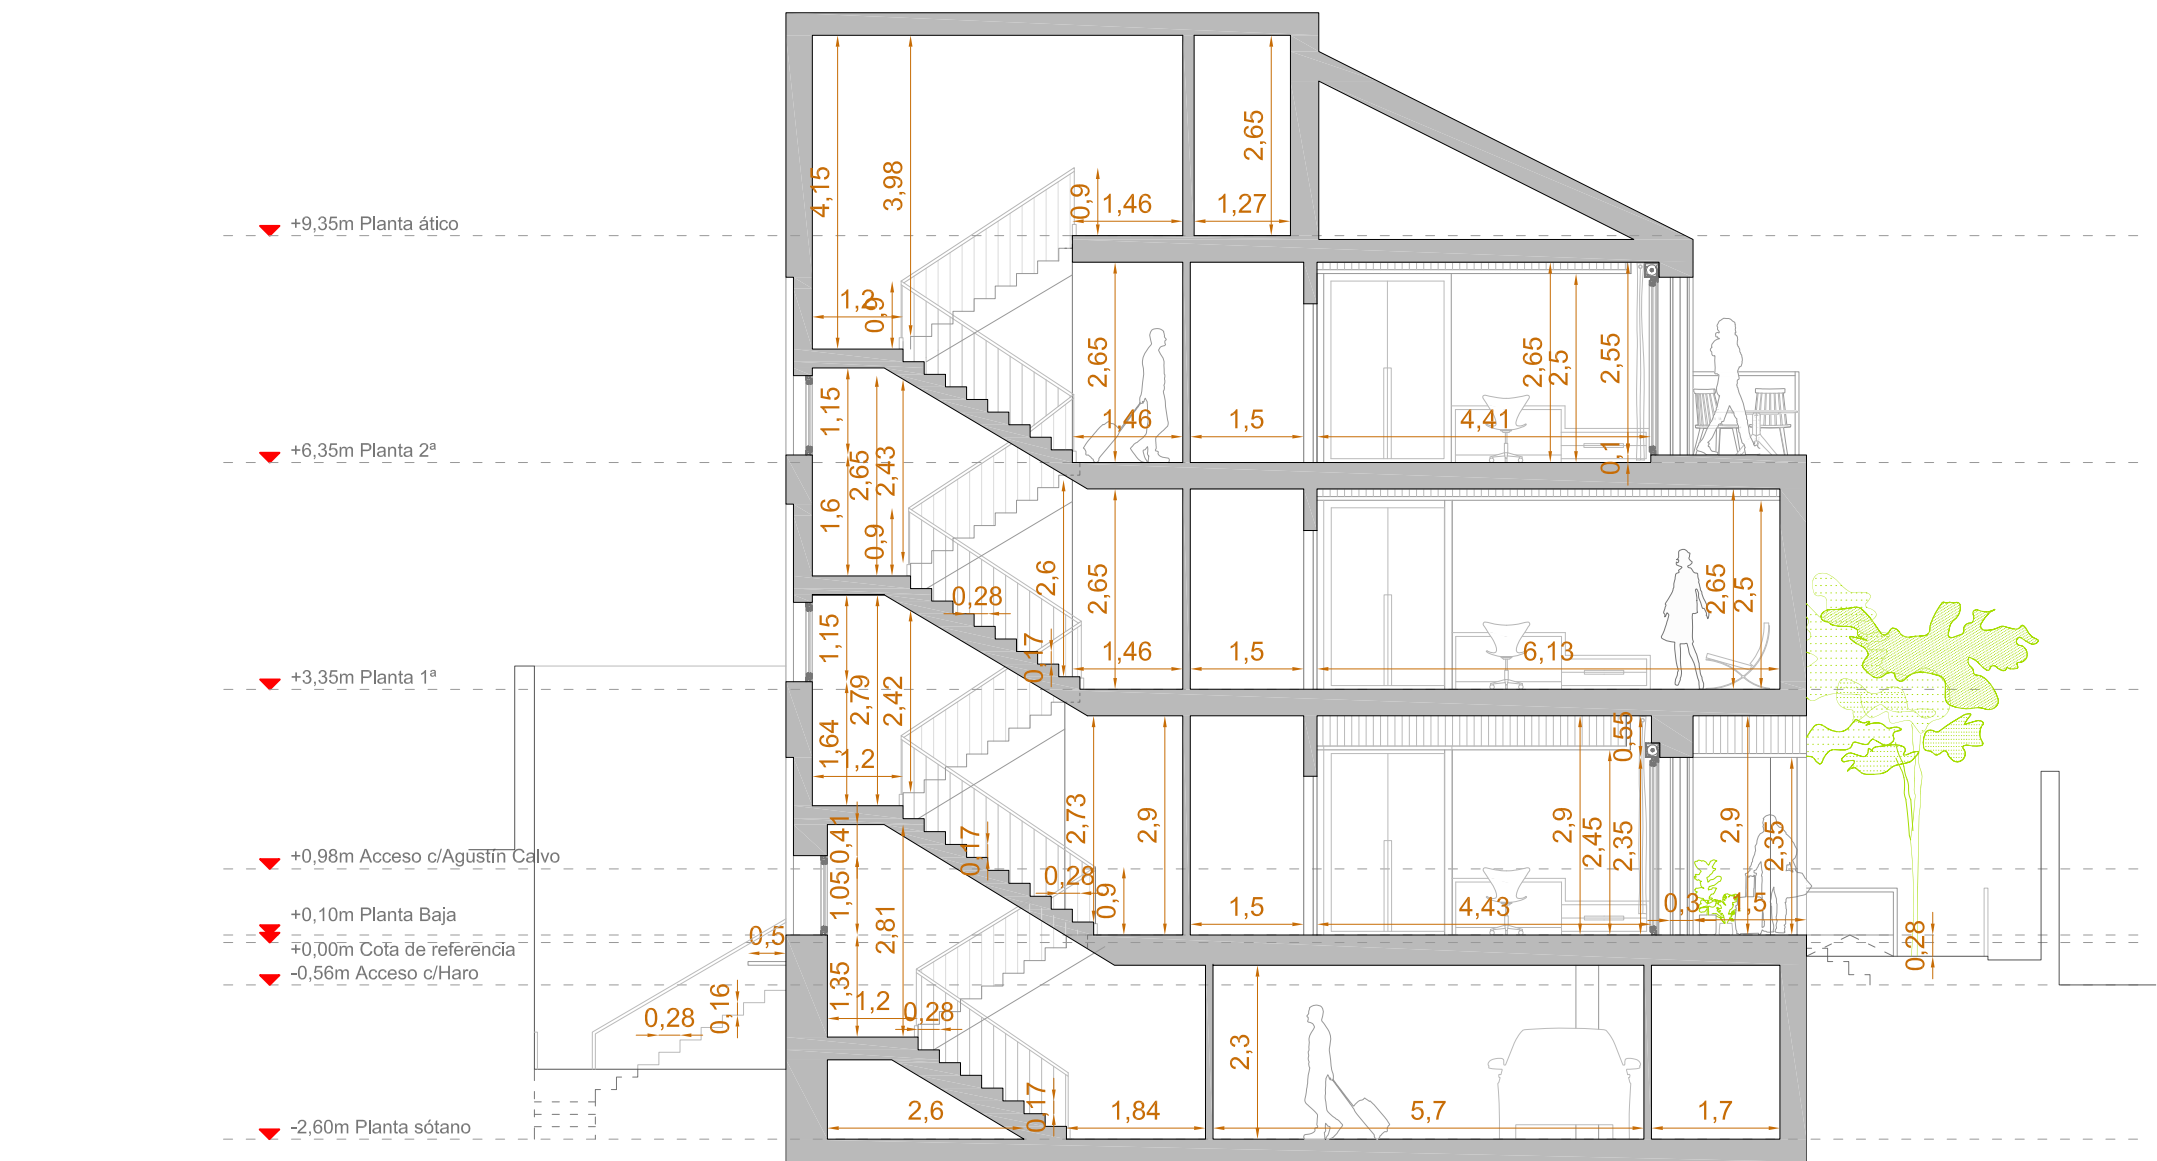

SECCIÓN 2

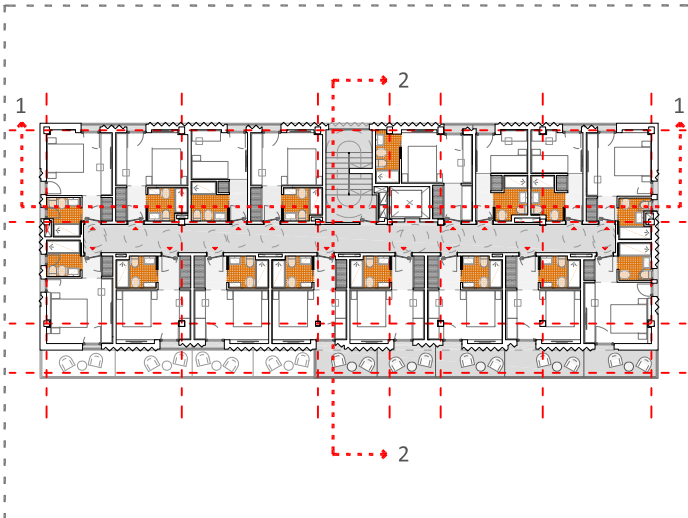

0 1 5m

APUNTOARQUITECTURA
teléfono: 649612449
www.apuntoarquitectura.com
oficina@apuntoarquitectura.com

PROYECTO
PROYECTO BÁSICO DE OBRAS PARA EL CAMBIO DE
USO DE EDIFICIO RESIDENCIAL A TERCIARIO
HOSPEDAJE. LICENCIA DE ACTIVIDAD_
HOTEL DE 2 ESTRELLAS. CI. Haro 5; 28043 Madrid

TITULAR
HARO 5 VENTURES S.L.
N.I.F.: B22599070
REPRESENTANTE
Rafael Garrido Rodrigo
D.N.I.: 00839470Q


TÉCNICO
Jorge Serrano de La Torre
COLEGIADO COAM 17.677

DESCRIPCIÓN
ARQUITECTURA REFORMADO: SECCIONES


NÚMERO DE PLANO	FECHA	ESCALA
A13	17.04.2026	1:100




QR validacion

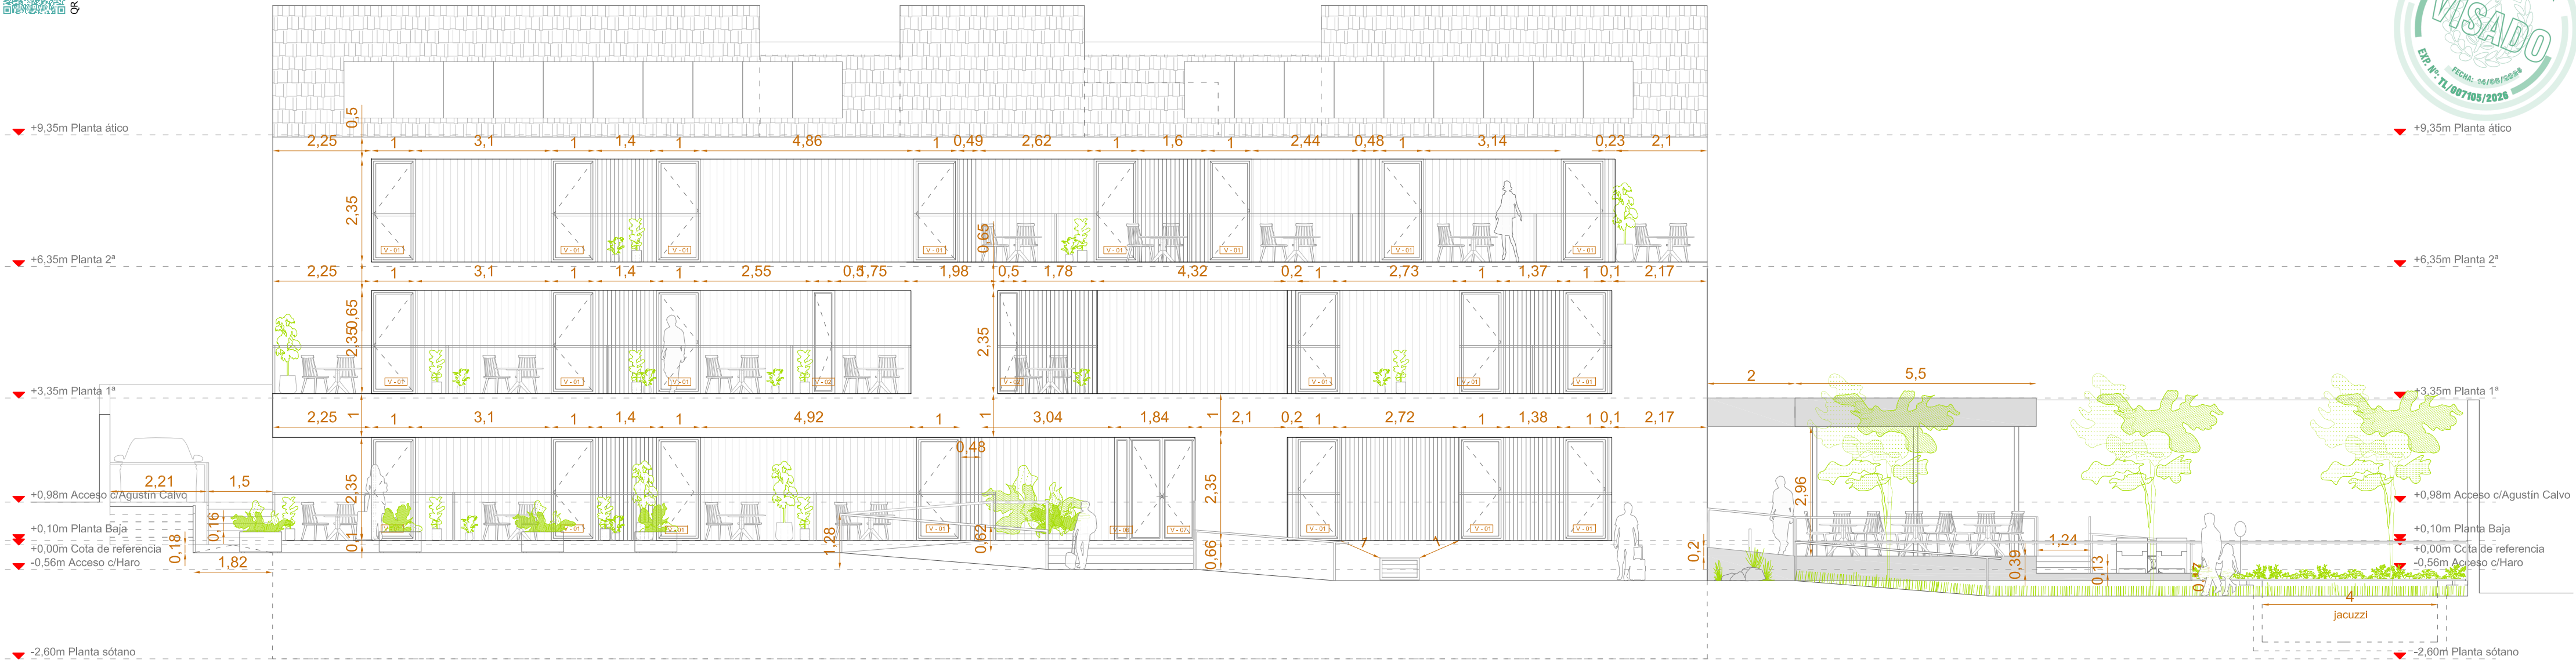

ALZADO 1

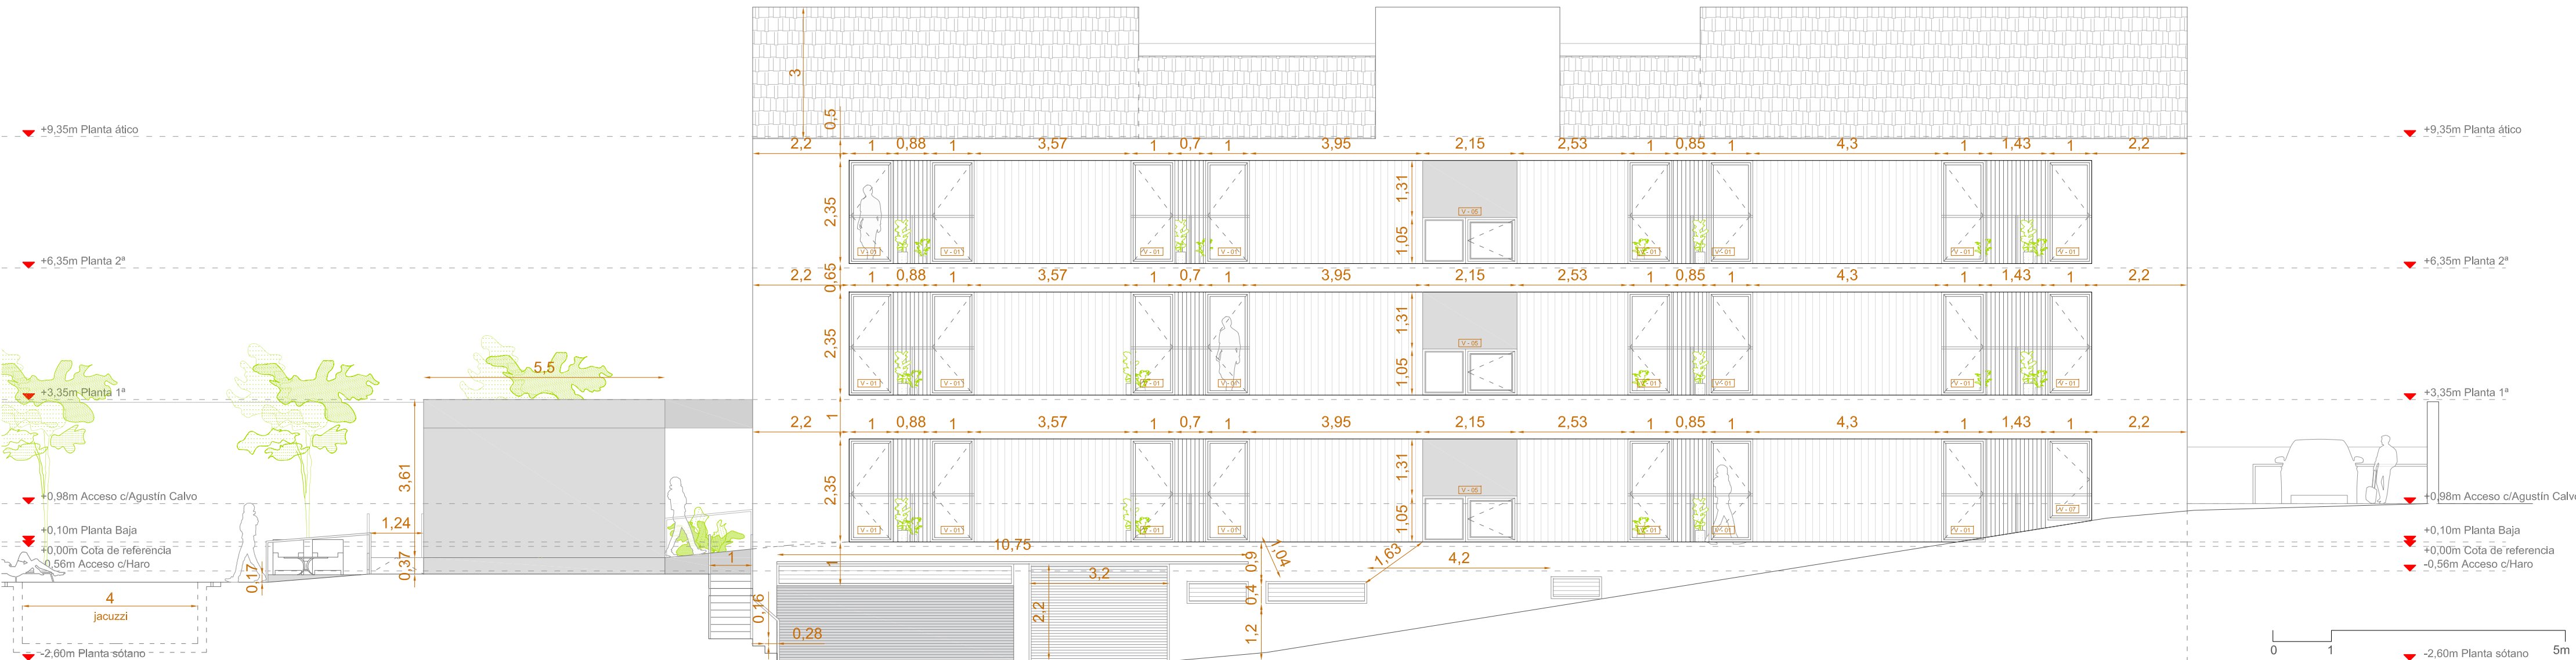

ALZADO 2

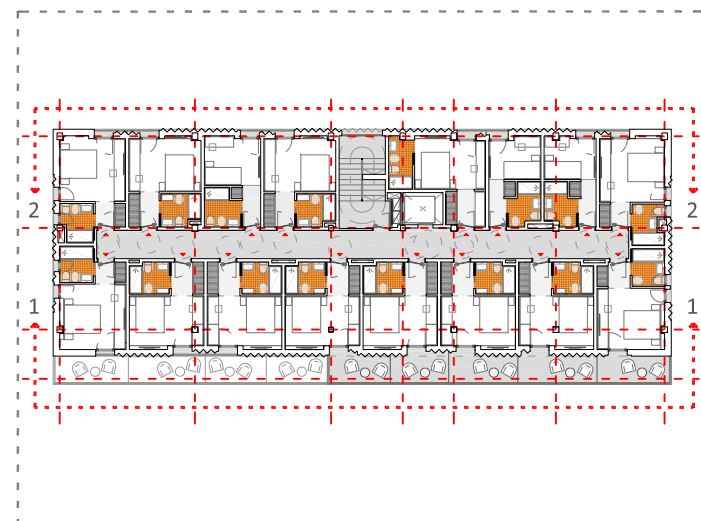

APUNTOARQUITECTURA
teléfono: 6 4 9 6 1 2 4 4 9
www.apuntoarquitectura.com
oficina@apuntoarquitectura.com


PROYECTO
PROYECTO BÁSICO DE OBRAS PARA EL CAMBIO DE
USO DE EDIFICIO RESIDENCIAL A TERCARIO
HOSPEDAJE. LICENCIA DE ACTIVIDAD_
HOTEL DE 2 ESTRELLAS. CI. Haro 5; 28043 Madrid
TITULAR
HARO 5 VENTURES S.L.
N.I.F.: B22599070
REPRESENTANTE
Rafael Garrido Rodrigo
D.N.I.: 00839470Q
TÉCNICO
Jorge Serrano de La Torre
COLEGIADO COAM 17.677
DESCRIPCIÓN
ARQUITECTURA REFORMADO: ALZADOS
NÚMERO DE PLANO ESCALA
A14 17.04.2026 1:75




QR validacion



ALZADO 3

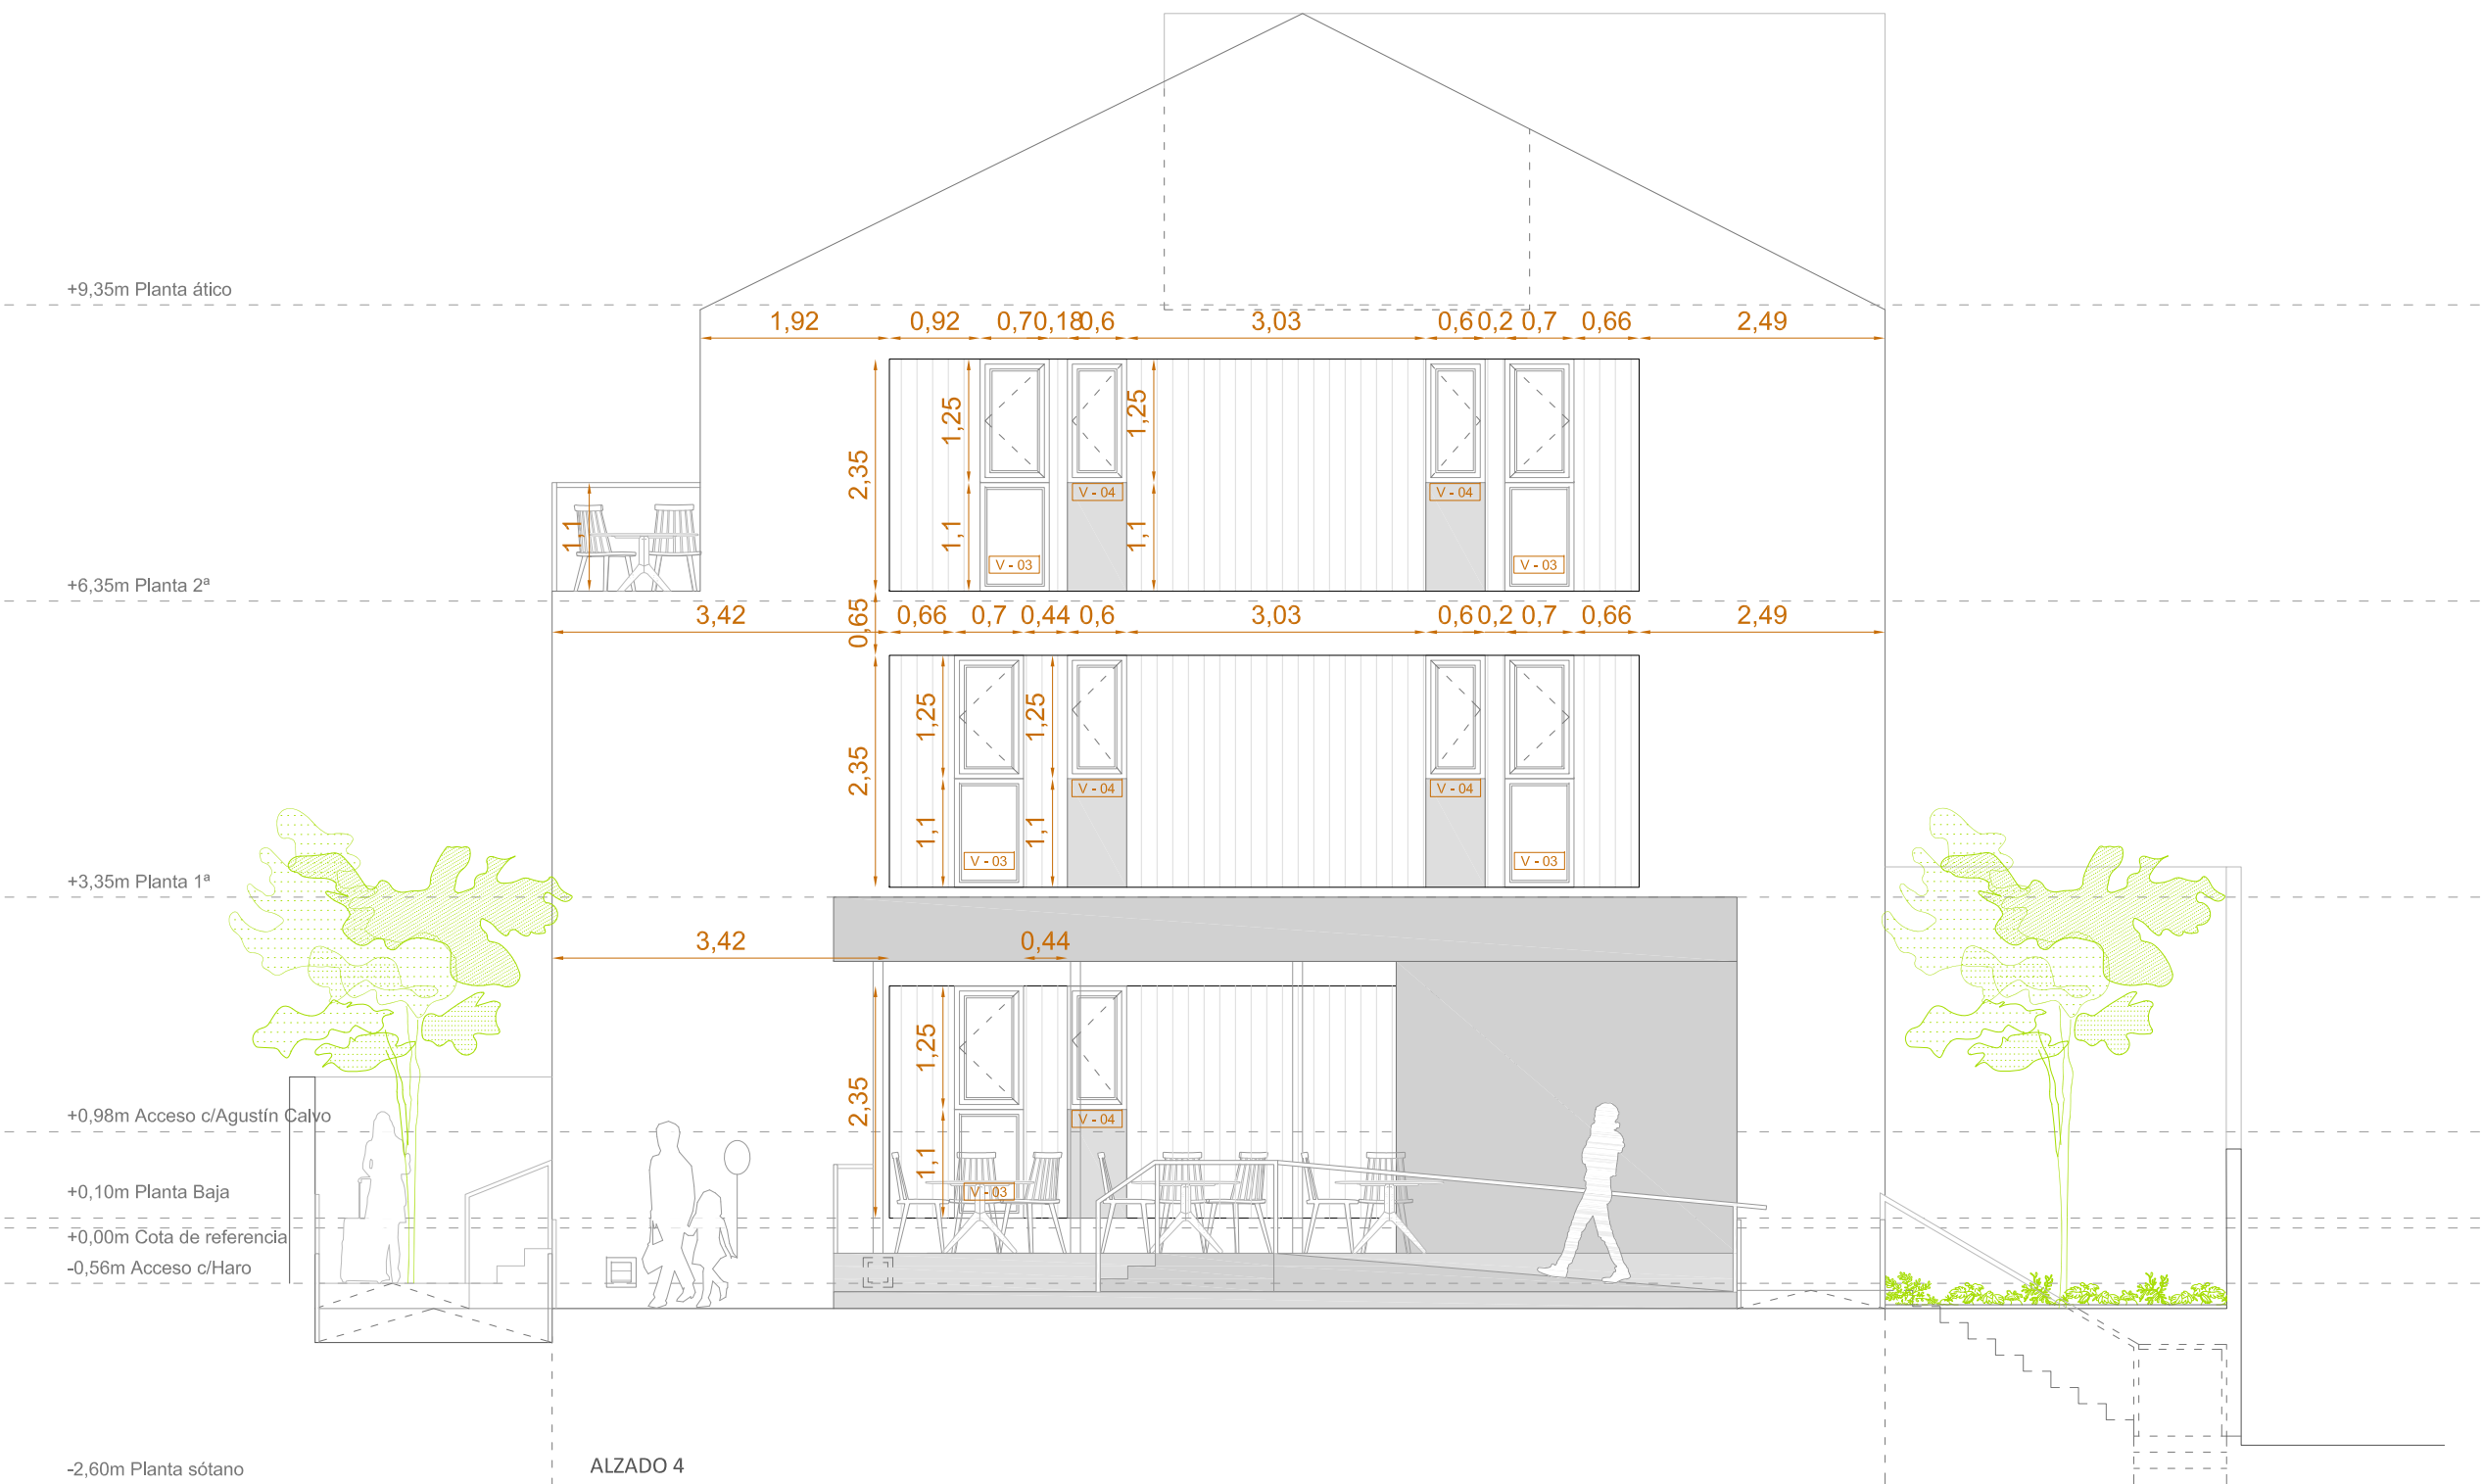

ALZADO 4

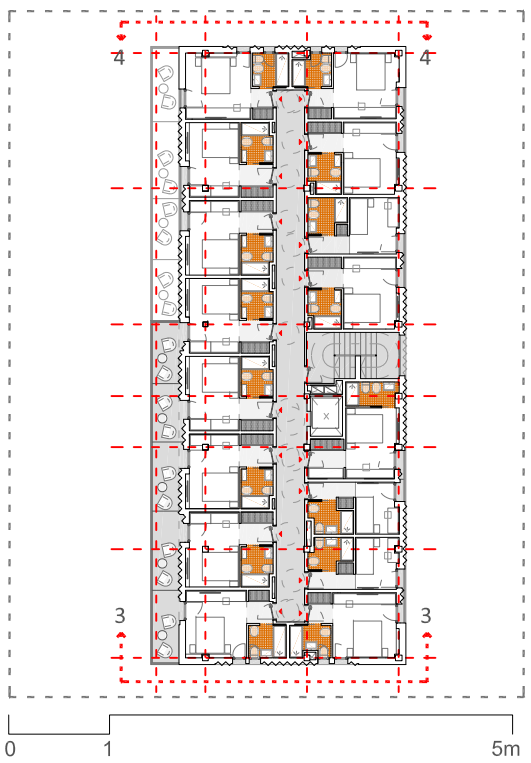

APUNTOARQUITECTURA
teléfono: 6 4 9 6 1 2 4 4 9
www.apuntoarquitectura.com
oficina@apuntoarquitectura.com

PROYECTO
PROYECTO BÁSICO DE OBRAS PARA EL CAMBIO DE
USO DE EDIFICIO RESIDENCIAL A TERCARIO
HOSPEDAJE. LICENCIA DE ACTIVIDAD_
HOTEL DE 2 ESTRELLAS. Cl. Haro 5; 28043 Madrid
TITULAR
HARO 5 VENTURES S.L.
N.I.F.: B22599070
REPRESENTANTE
Rafael Garrido Rodrigo
D.N.I.: 00839470Q

TÉCNICO
Jorge Serrano de La Torre
COLEGIADO COAM 17.677

DESCRIPCIÓN



ARQUITECTURA REFORMADO: ALZADOS LATERALES

NÚMERO DE PLANO FECHA ESCALA

A15 17.04.2026 1:75



QR validation

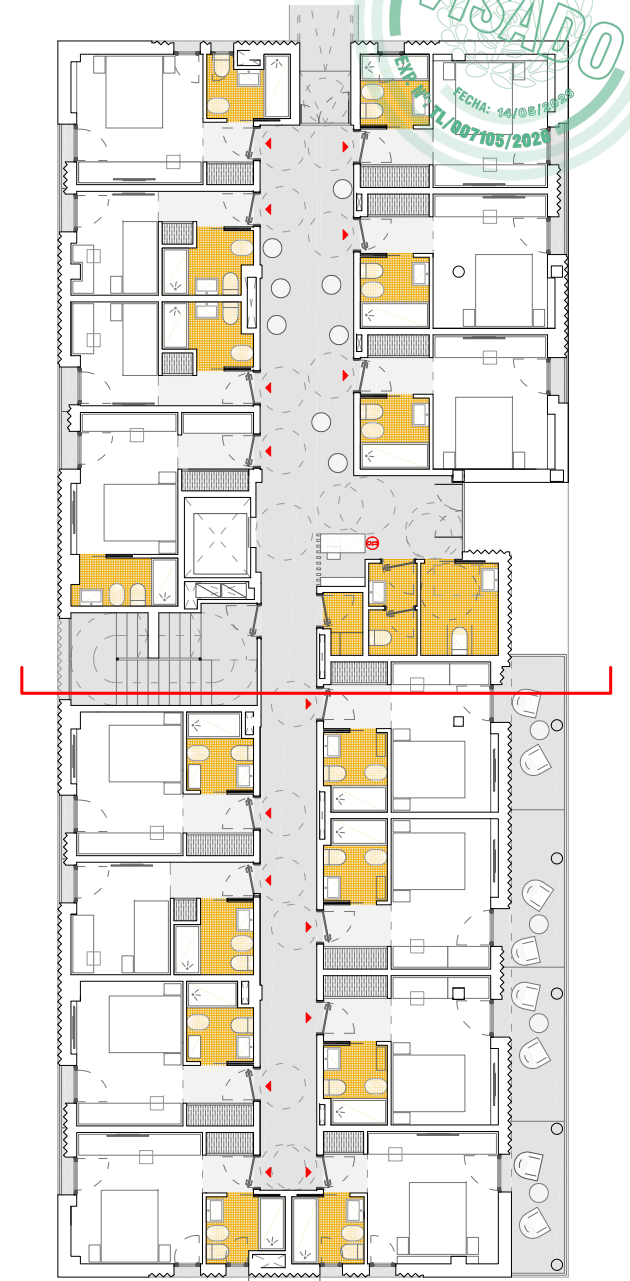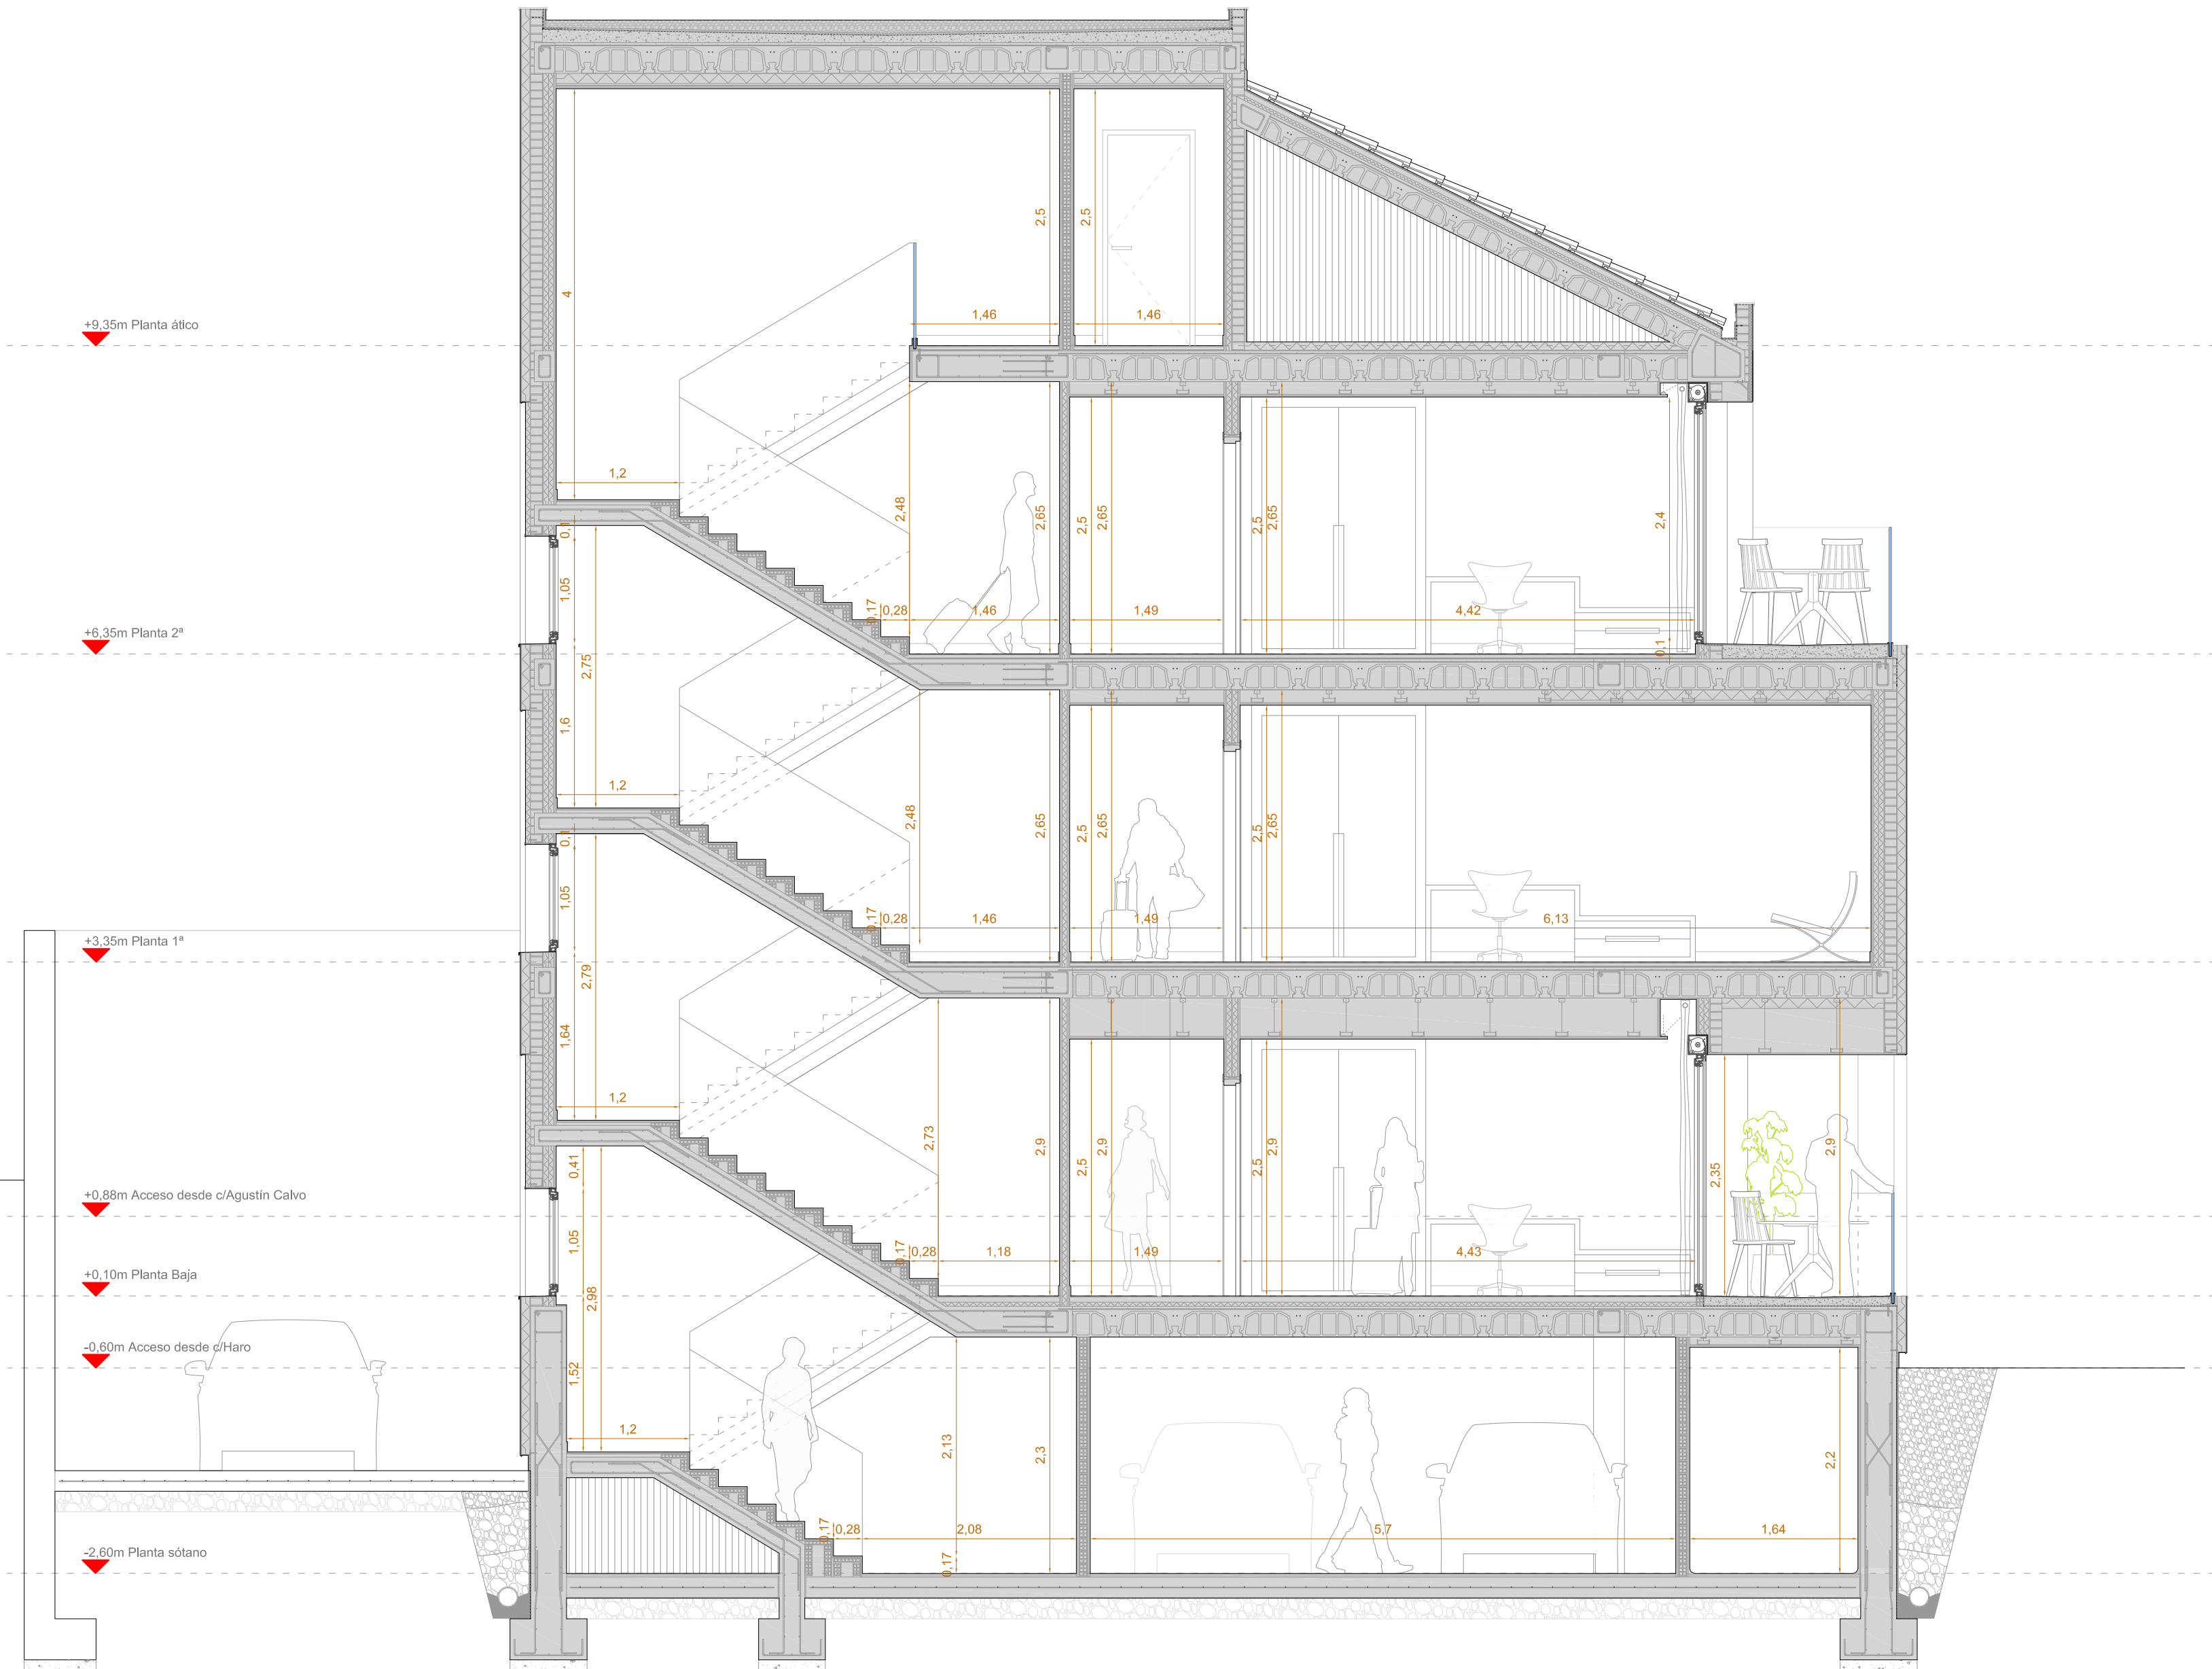






APUNTOARQUITECTURA
teléfono: 649612449
www.apuntoarquitectura.com
oficina@apuntoarquitectura.com

PROYECTO
PROYECTO BÁSICO DE OBRAS PARA EL CAMBIO DE
USO DE EDIFICIO RESIDENCIAL A TERCIARIO
HOSPEDAJE. LICENCIA DE ACTIVIDAD_
HOTEL DE 2 ESTRELLAS. Cl. Haro 5; 28043 Madrid
TITULAR
HARO 5 VENTURES S.L.
N.I.F.: B22599070
REPRESENTANTE
Rafael Garrido Rodrigo
D.N.I.: 00839470Q

TÉCNICO
Jorge Serrano de La Torre
COLEGIADO COAM 17.677
DESCRIPCIÓN
CONSTRUCCIÓN: SECCIÓN CONSTRUCTIVA

NÚMERO DE PLANO FECHA ESCALA

C01 17.04.2026 1:50

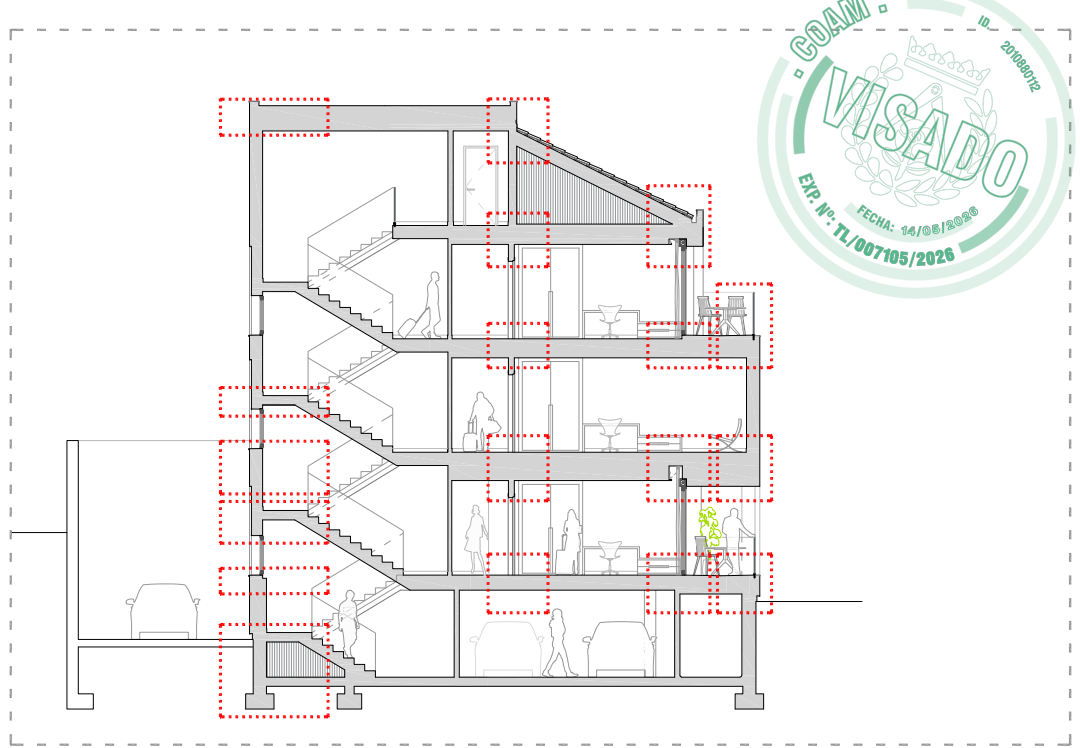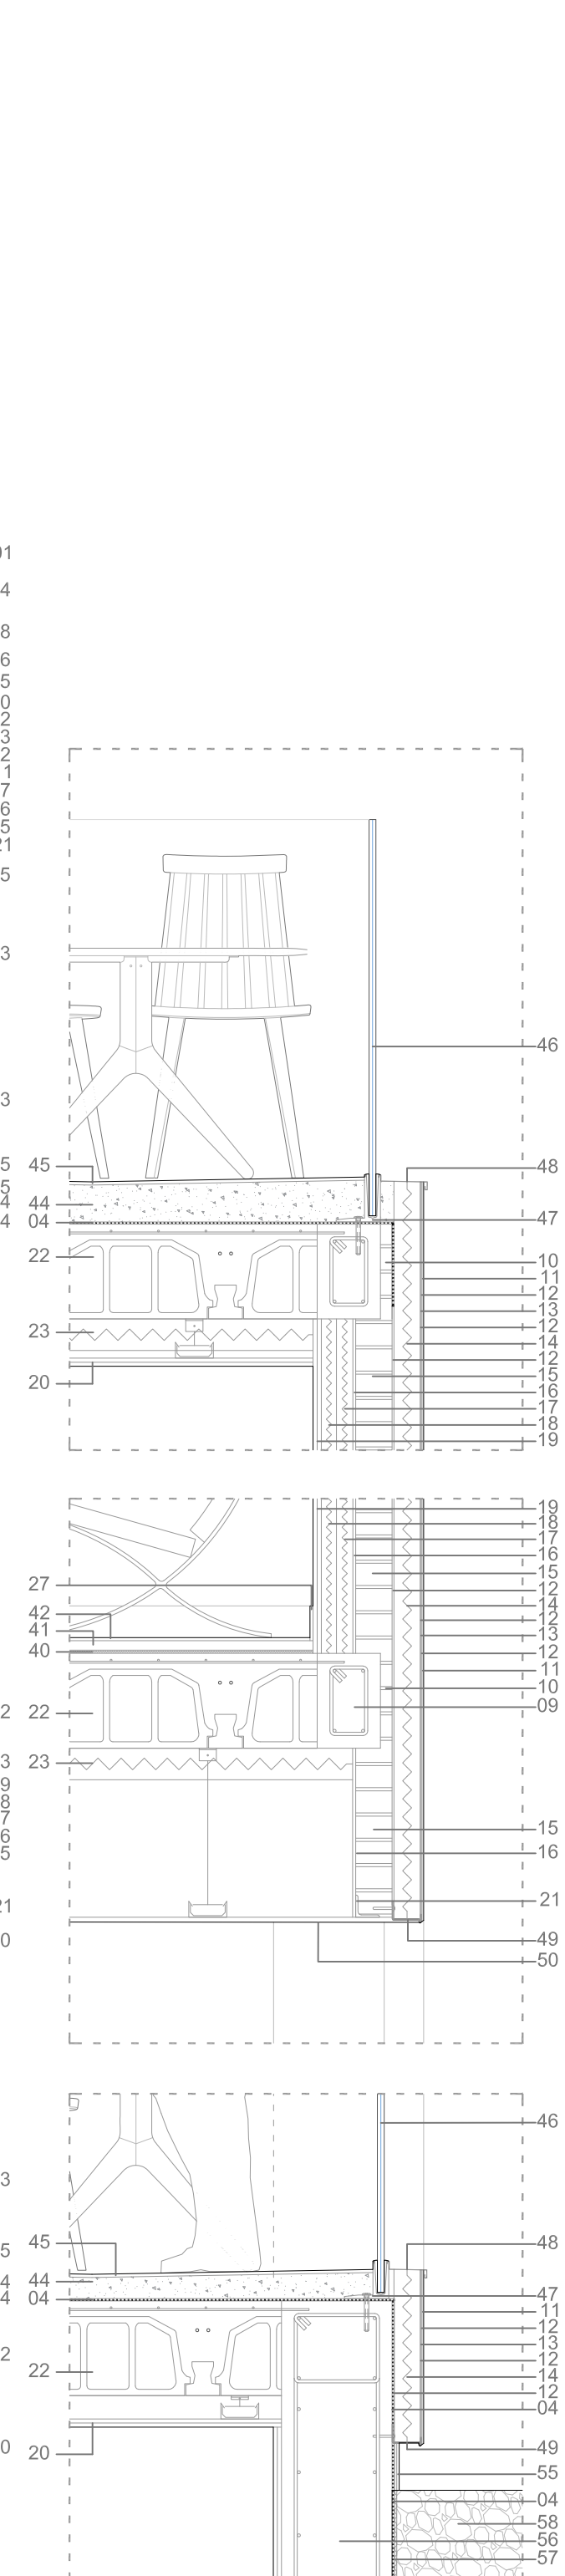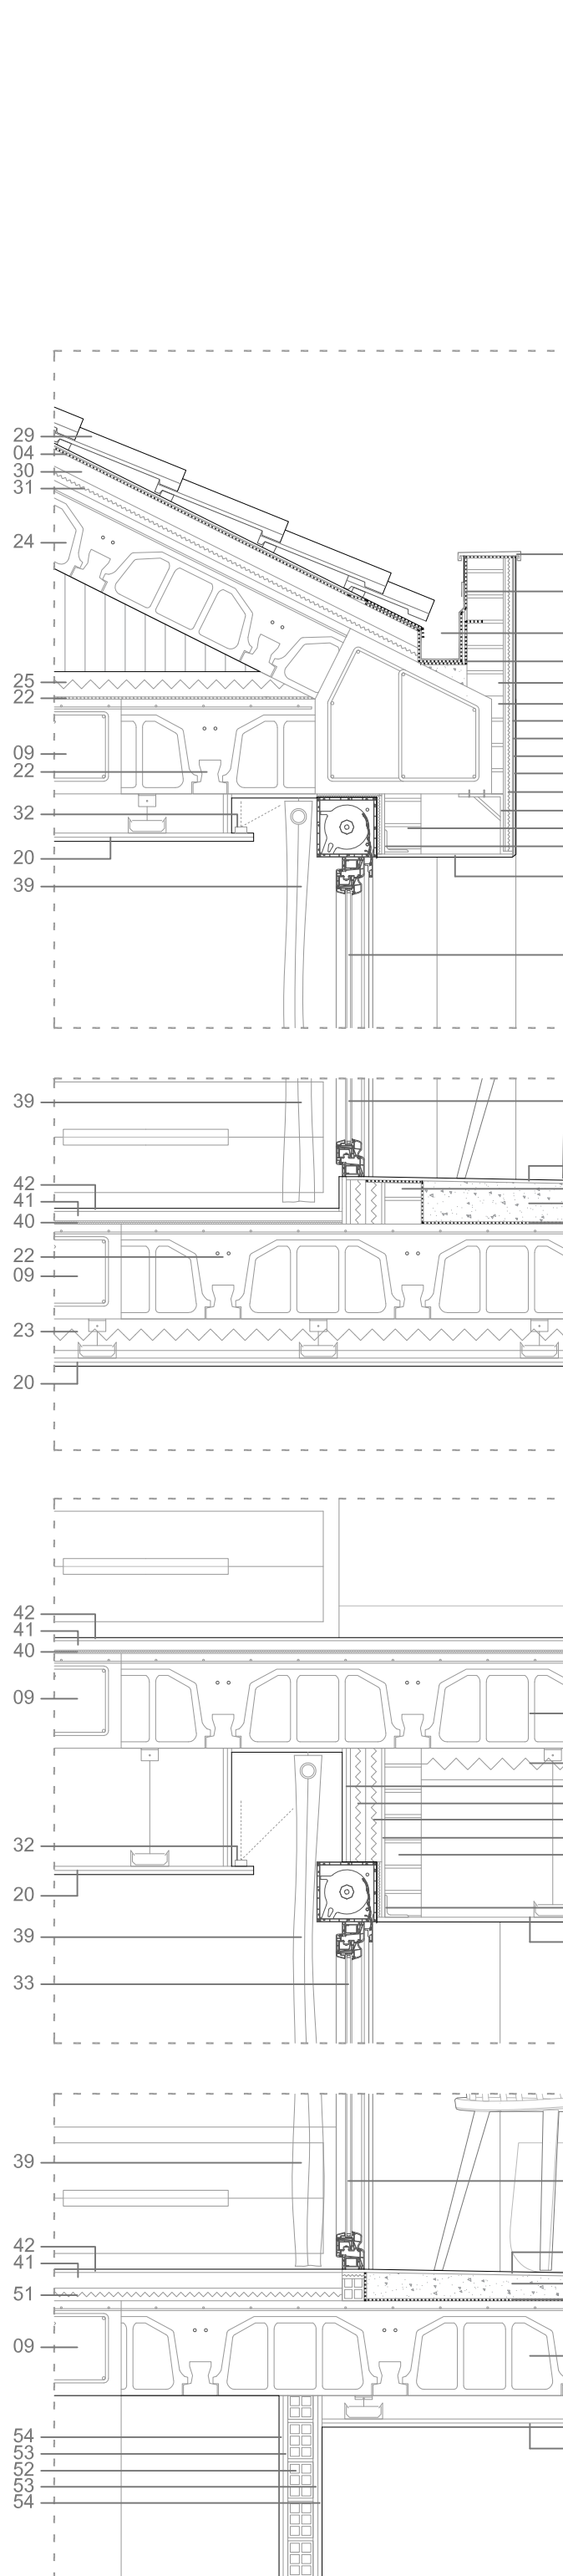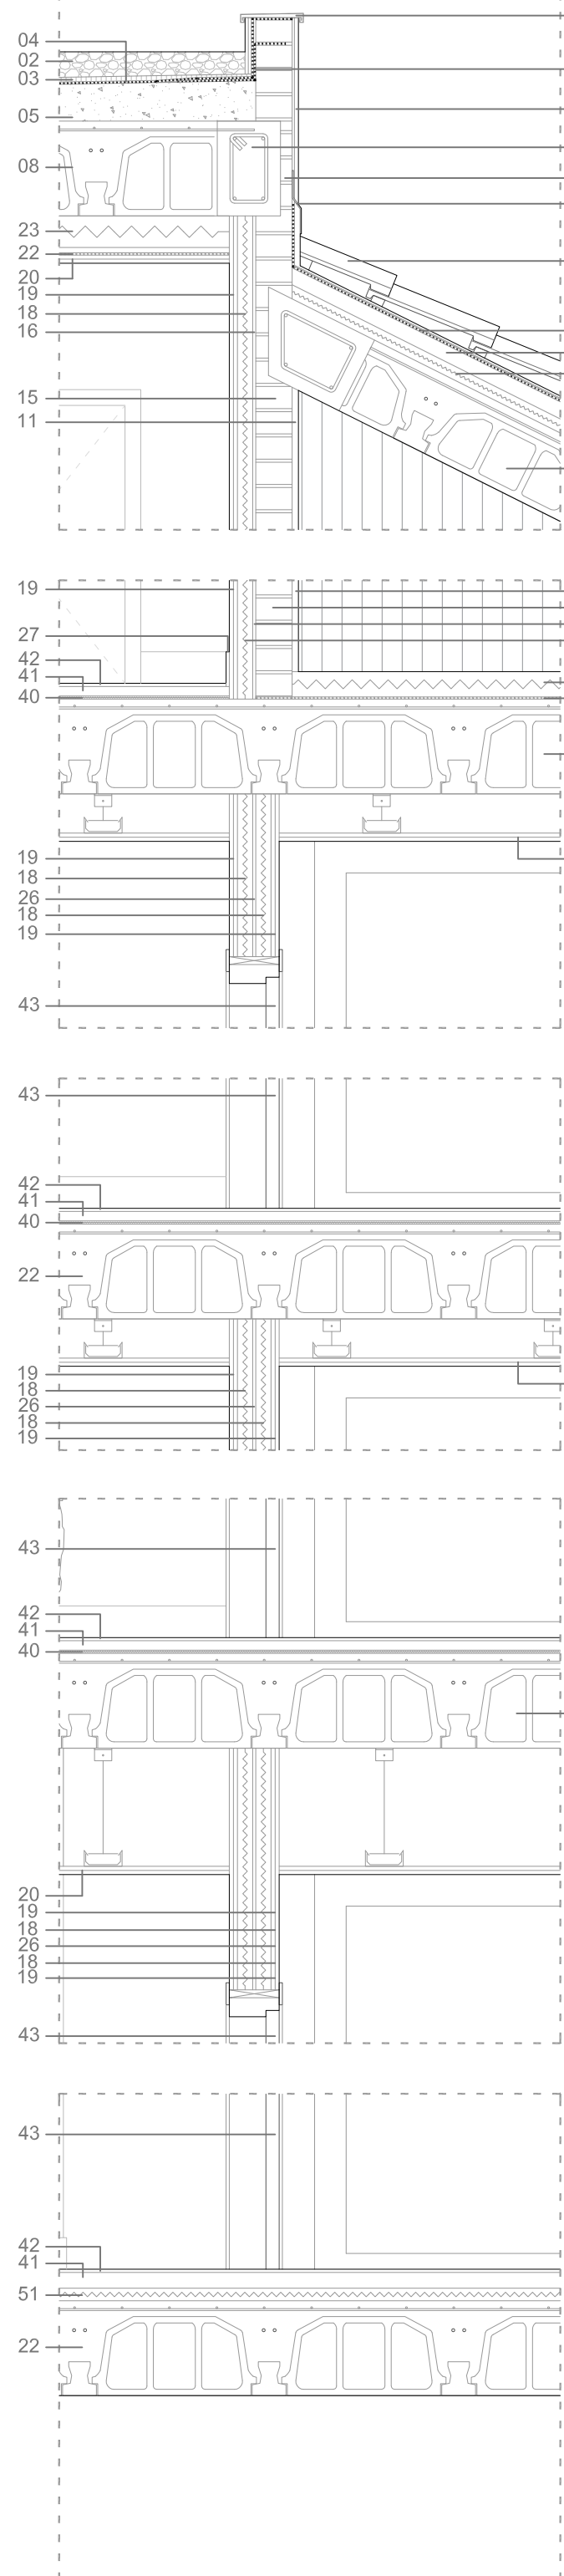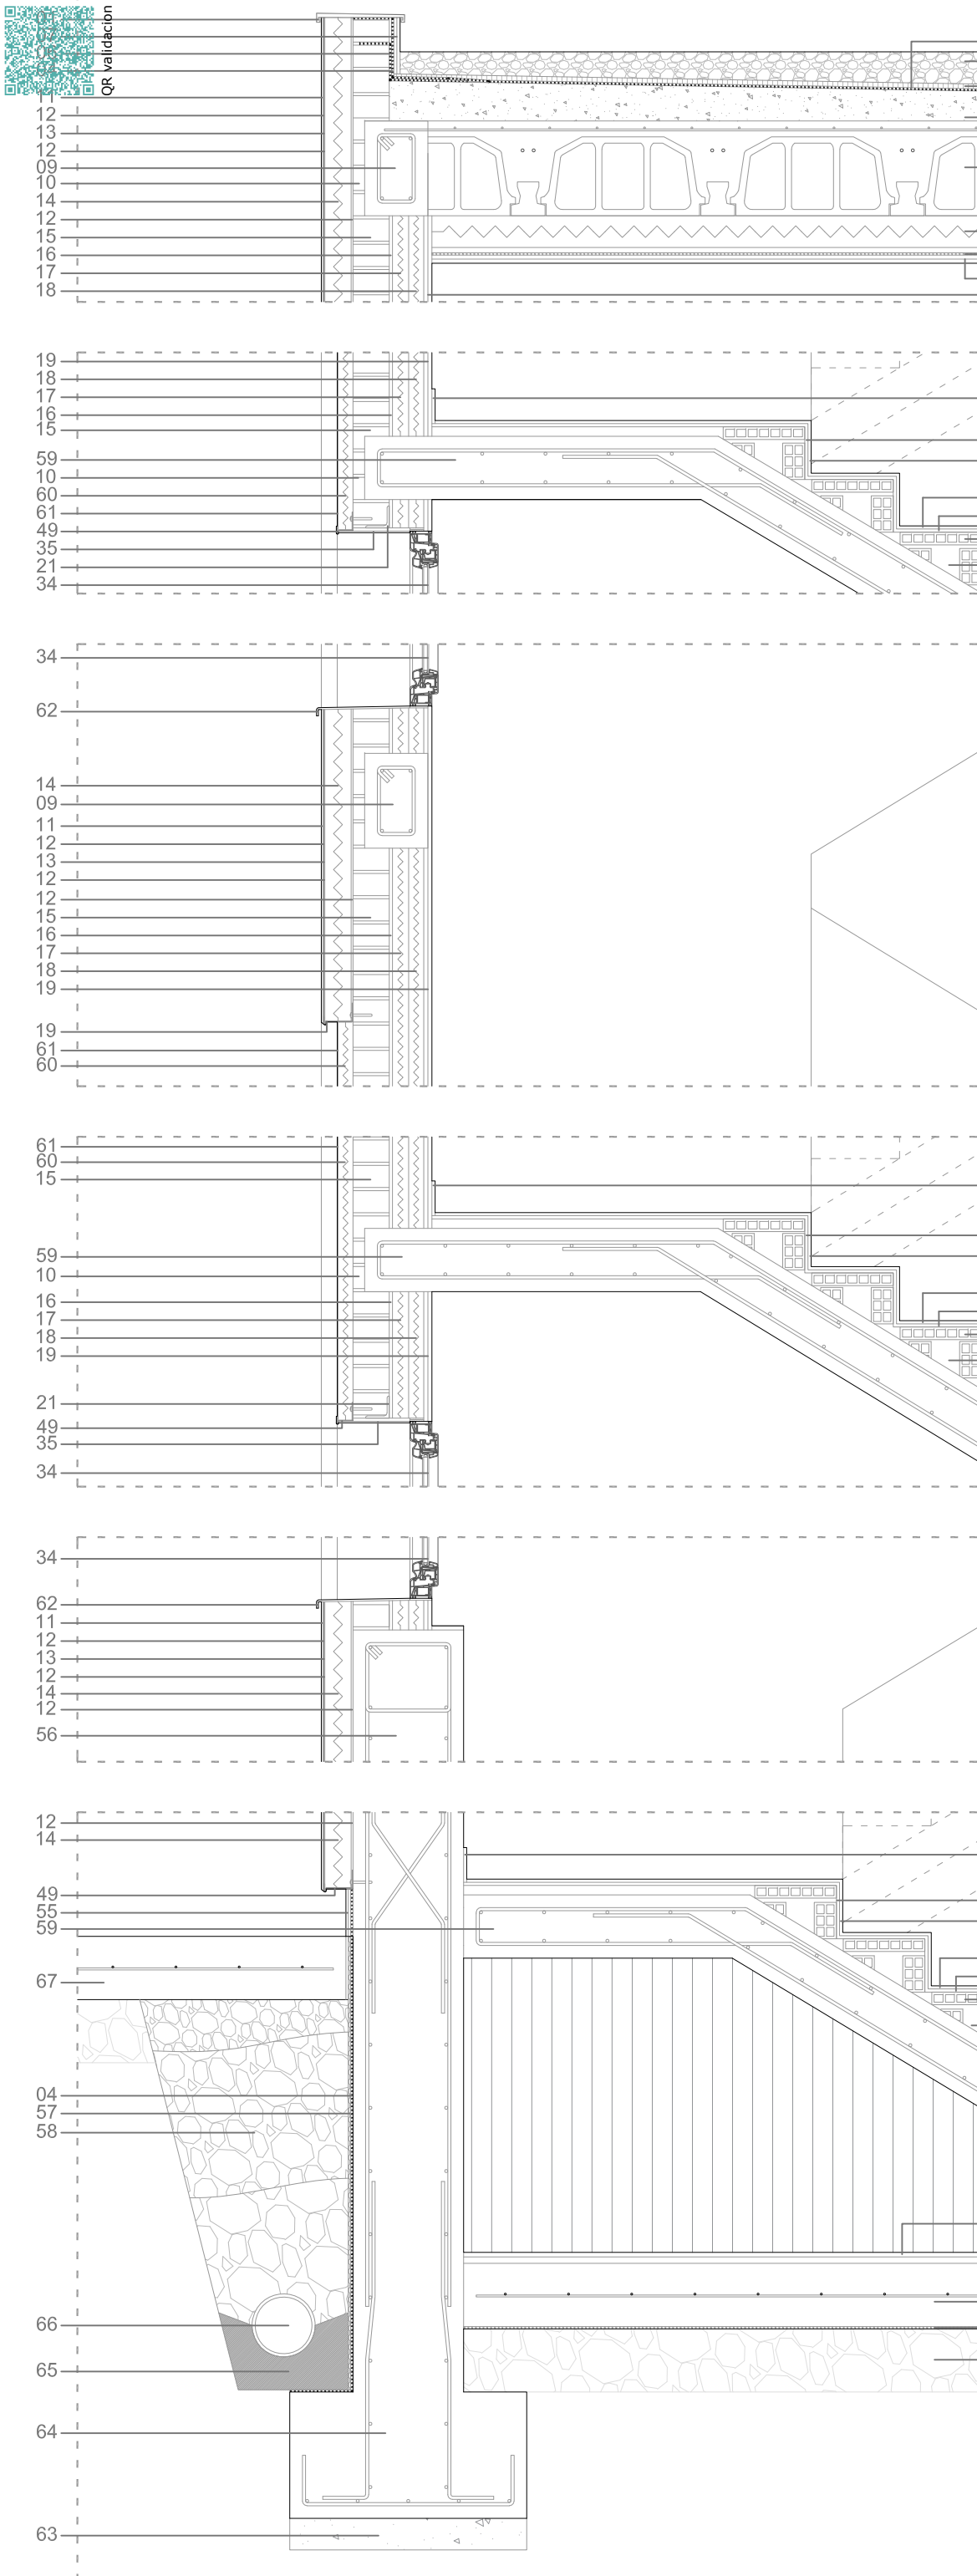

01- Albardilla de chapa de acero galvanizado con goterón.

02- Protección de grava.

03- Capa separadora bajo protección.

04- Impermeabilizante.

05- Hormigón de pendiente.

06- Refuerzo impermeabilizante.

07- Zócalo para protección de impermeabilizante en peto de cubierta plana no transitable, adherido con mortero.

08- Forjado unidireccional de bovedillas cerámicas y capa de compresión.

09- Zuncho o viga de hormigón armado.

10- Galleta de ladrillo cerámico para canto de forjado.

11- Mortero de acabado

12- Mortero de agarre y regularización.

13- Malla de fibra de vidrio

14- Aislamiento EPS, (e=10cm), con anclajes de polipropileno y taco expansivo.

15- 1/2 pie de ladrillo perforado.

16- Mortero hidrófugo.

17- Aislamiento XPS (e=5cm)

18- Aislamiento de lana de roca en estructura autoportante de pladur (e=4,8m).

19- Doble placa de yeso atornillada a su estructura. Acabado con pintura plástica o azulejo cerámico, a definir por ola D.F. (e_{total}=1,3cm + 1,3cm= 2,6cm).

20- Falso techo de pladur sobre perfilera metálica formada por doble placa de yeso (e=2,6cm).

21- Cargadero, perfil metálico en L.

22- Barrera de vapor.

23- Aislamiento XPS bajo el forjado (e=10cm).

24- Forjado unidireccional de bovedillas cerámicas para cubierta inclinada.

25- Aislamiento sobre forjado XPS (e=8cm).

26- Separación de 1cm.

27- Rodapié cerámico a definir por la D.F.

28- Babero de chapa de acero.

29- Teja curva cerámica.

30- Capa de regularización de mortero

31- Aislamiento existente en cubierta.

32- Luz led en foseado de falso techo.

33- Ventana tipo monoblock con cajón de persiana incorporado, carpintería según plano de carpinterías.

34- Ventana sin cajón de persiana, según plano de carpinterías.

35- Remate superior de hueco de chapa.

36- Perfil metálico, atornillado al forjado, para sujección inferior de sate.

37- Aislamiento EPS, (e=3cm), con anclajes de polipropileno y taco expansivo.

38- Canalón de chapa oculto.

39- Cortina.

40- Aislamiento EEPS (e=1cm), para suelo flotante.

41- Mortero de protección

42- Pavimento cerámico adherido con cemento cola.

43- Puerta de madera según planos de carpinterías.

44- Hormigón de pendiente.

45- Pavimento cerámico para exterior.

46- Barandilla de vidrio anclada a forjado.

47- Anclaje de barandilla al forjado.

48- Remate de borde de terraza mediante perfil de chapa con goterón.

49- Perfil de arranque de sate de PVC.

50- Falso techo de chapa para exterior.

51- Aislamiento EEPS (e=4cm), para suelo flotante de planta baja.

52- Ladrillo hueco doble (e=8cm)

53- Guarnecido (e=1,5cm)

54- Placa de yeso (e=1,3cm).

55- Zócalo cerámico para protección de impermeabilizante.

56- Muro de sótano existente.

57- Membrana de drenado tipo Delta Drain.

58- Capa de grava filtrante.

59- Losa de hormigón para formación de zanca de escalera.

60- Aislamiento EPS, (e=5cm).

61- Acabado de chapa plegada.

62- Alféizar de chapa con goterón.

63- Hormigón de limpieza.

64- Zapata de hormigón armado.

65- Cama de arena.

66- Tubo de drenaje microperforado de PVC.

67- Solera de hormigón para rampa de garaje.

68- Encachado de piedra.

69- Solera de hormigón armado.

70- Lámina de polietileno.

71- Rasillón cerámico para formación de peldaños.

72- Formación de peldaños de escalera con ladrillo hueco doble.

73- Tabica cerámica para escalera.

74- Pavimento cerámico de escalera.

01

02

03

04

05

06

07

08

09

10

11

12

13

14

15

16

17

18

19

20

21

22

23

24

25

26

27

28

29

30

31

32

33

34

35

36

37

38

39

40

41

42

43

44

45

46

47

48

49

50

51

52

53

54

55

56

57

58

59

60

61

62

63

64

65

66

67

68

69

70

71

72

73

74

01

02

03

04

05

06

07

08

09

10

11

12

13

14

15

16

17

18

19

20

21

22

23

24

25

26

27

28

29

30

31

32

33

34

35

36

37

38

39

40

41

42

43

44

45

46

47

48

49

50

51

52

53

54

55

56

57

58

59

60

61

62

63

64

65

66

67

68

69

70

71

72

73

74

01

02

03

04

05

06

07

08

09

10

11

12

13

14

15

16

17

18

19

20

21

22

23

24

25

26

27

28

29

30

31

32

33

34

35

36

37

38

39

40

41

42

43

44

45

46

47

48

49

50

51

52

53

54

55

56

57

58

59

60

61

62

63

64

65

66

67

68

69

70

71

72

73

74

01

02

03

04

05

06

07

08

09

10

11

12

13

14

15

16

17

18

19

20

21

22

23

24

25

26

27

28

29

30

31

32

33

34

35

36

37

38

39

40

41

42

43

44

45

46

47

48

49

50

51

52

53

54

55

56

57

58

59

60

61

62

63

64

65

66

67

68

69

70

71

72

73

74

01

02

03

04

05

06

07

08

09

10

11

12

13

14

15

16

17

18

19

20

21

22

23

24

25

26

27

28

29

30

31

32

33

34

35

36

37

38

39

40

41

42

43

44

45

46

47

48

49

50

51

52

53

54

55

56

57

58

59

60

61

62

63

64

65

66

67

68

69

70

71

72

73

74

01

02

03

04

05

06

07

08

09

10

11

12

13

14

15

16

17

18

19

20

21

22

34

35

36

37

38

39

40

41

42

43

44

45

46

47

48

49

50

51

52

53

54

55

56

57

58

59

60

61

62

63

64

65

66

67

68

69

70

71

72

73

74

01

02

03

04

05

06

07

08

09

10

11

12

13

14

15

16

17

18

19

20

21

22

23

24

25

26

27

28

29

30

31

32

33

34

35

36

37

38

39

40

41

42

43

44

45

46

47

48

49

50

51

52

53

54

55

56

57

58

59

60

61

62

63

64

65

66

67

68

69

70

71

72

73

74

01

02

03

04

05

06

07

08

09

10

11

12

13

14

15

16

17

18

19

20

21

22

23

24

25

26

27

28

29

30

31

32

33

34

35

36

37

38

39

40

41

42

43

44

45

46


47

48


49

50


5

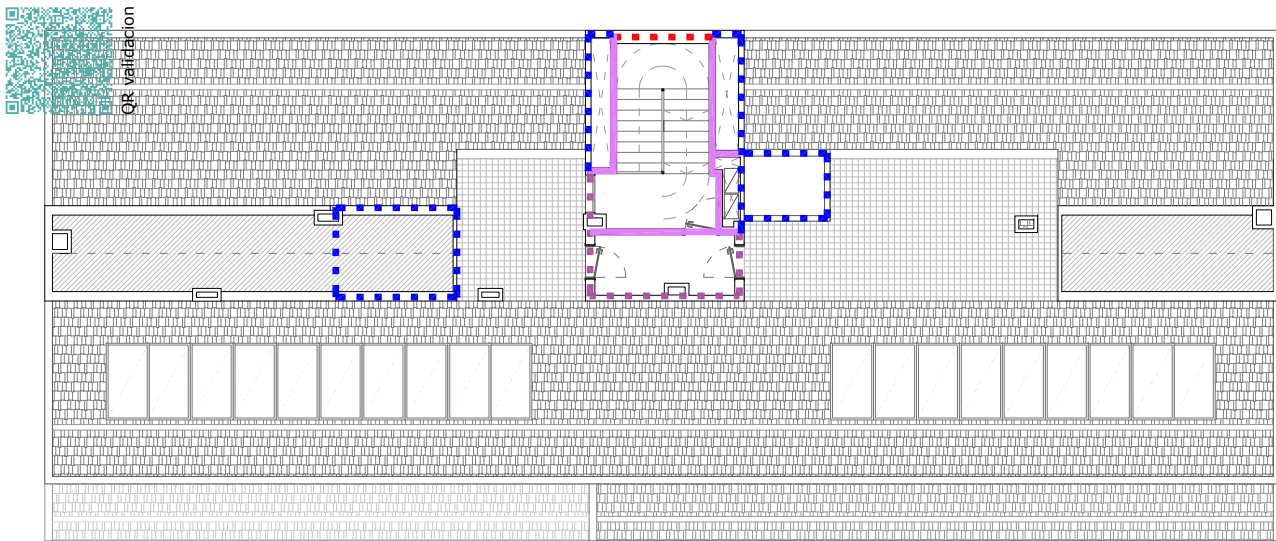


PLANTA BAJO-CUBIERTA

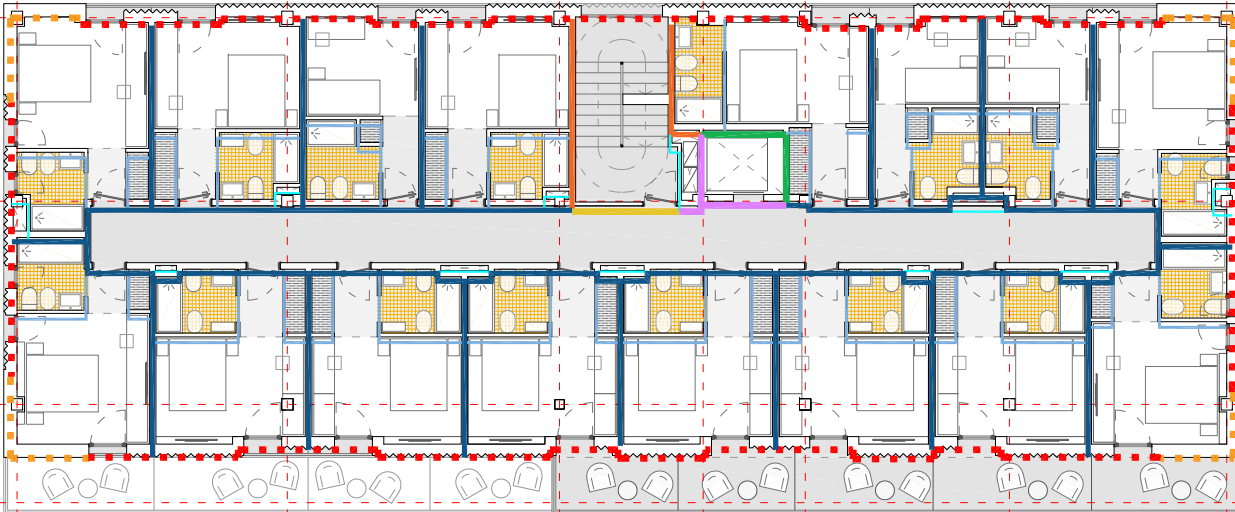


PLANTA 2ª

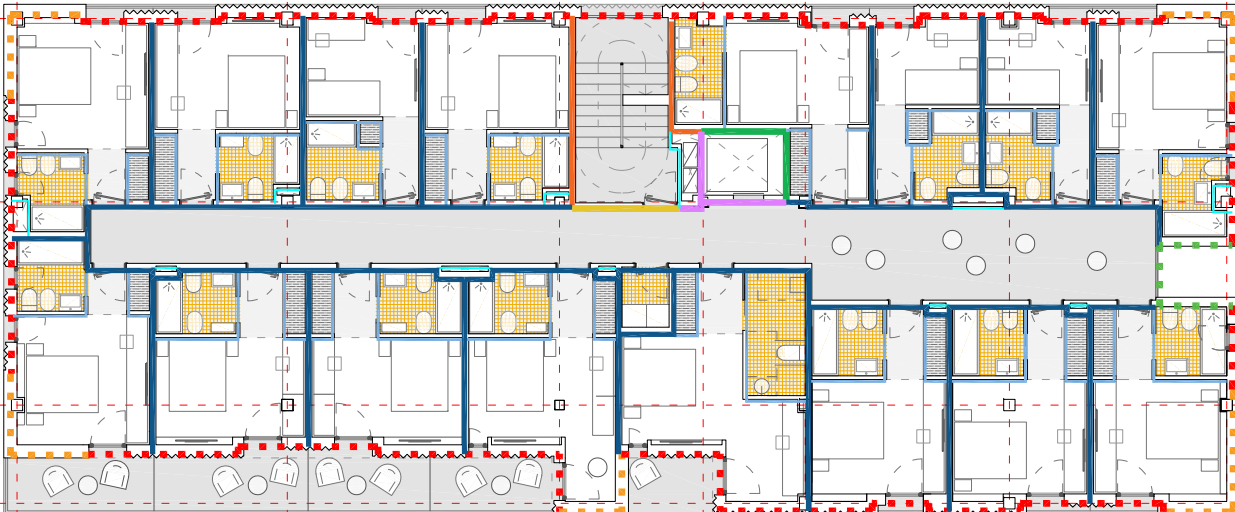


PLANTA 1ª

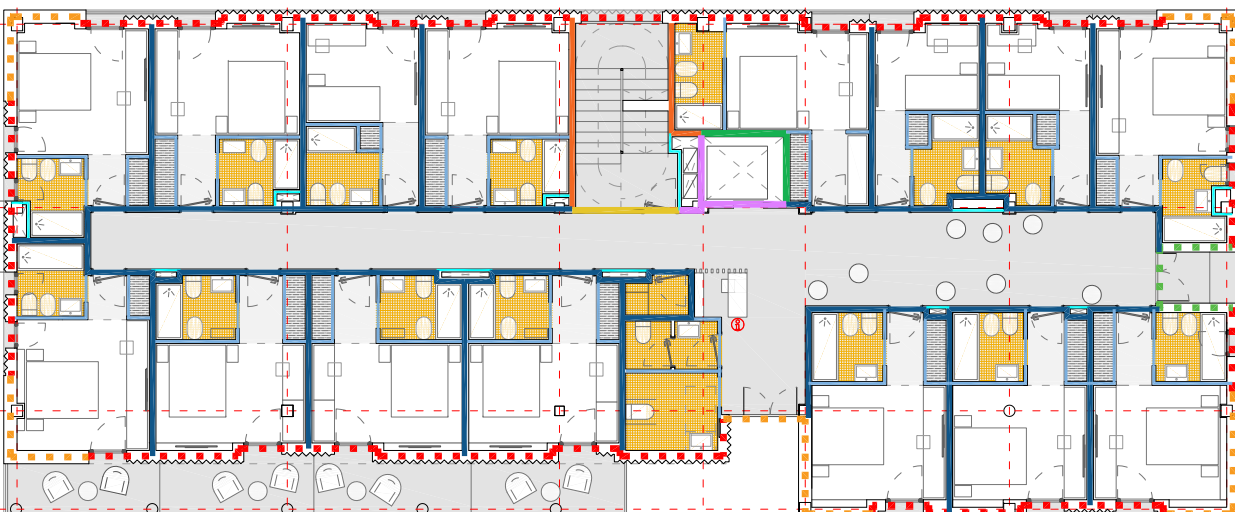

PLANTA BAJA

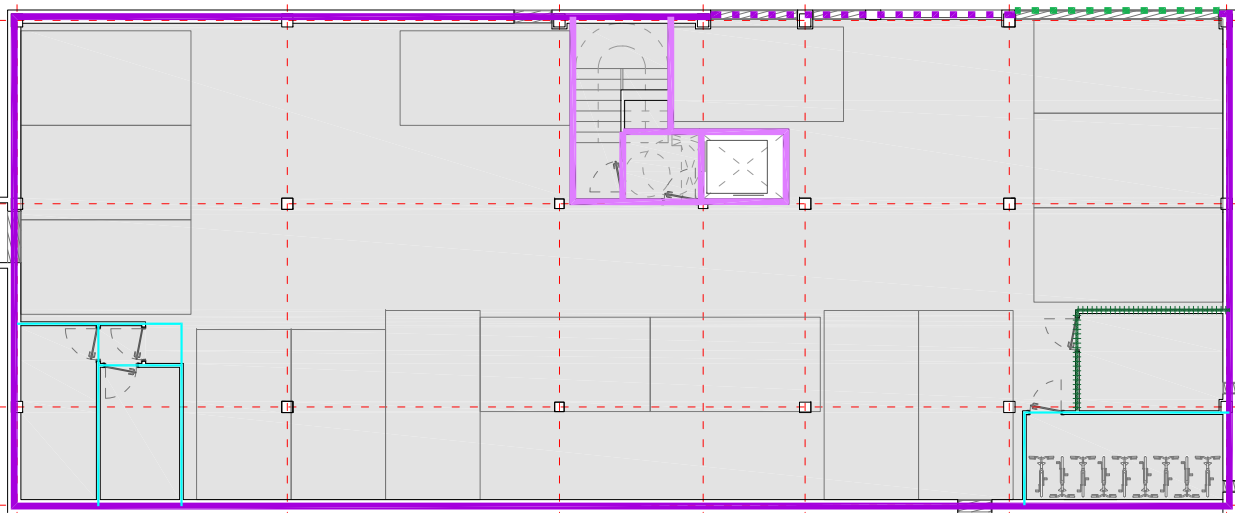

PLANTA SÓTANO

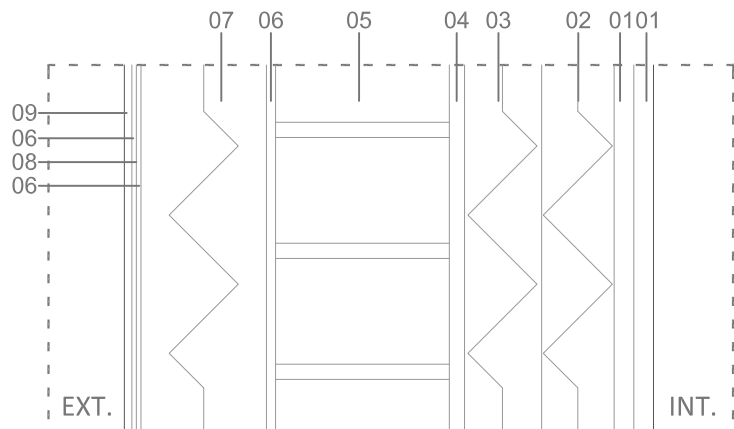


F01: FACHADA SATE LISA

E_{total}=35cm

Resistencia a Fuego ≥ EI-120

Resistencia a Ruido = 55dBA / masa= 235kg/m²

- 01- Placa de yeso (e=1,3cm)
- 01- Placa de yeso (e=1,3cm)
- 02- Estructura de autoportante de pladur con lana de roca (e=4,8cm)
- 03- Aislamiento XPS (e=5cm)
- 04- Mortero hidrófugo (e=1cm)
- 05- 1/2 pie de ladrillo perforado (e=11,5cm)
- 06- Mortero de agarre y regularización
- 07- Aislamiento EPS, (e=10cm), con anclajes de polipropileno y taco expansivo.
- 06- Mortero de agarre y regularización.
- 08- Malla de fibra de vidrio
- 06- Mortero de agarre y regularización.
- 09- Mortero de acabado.

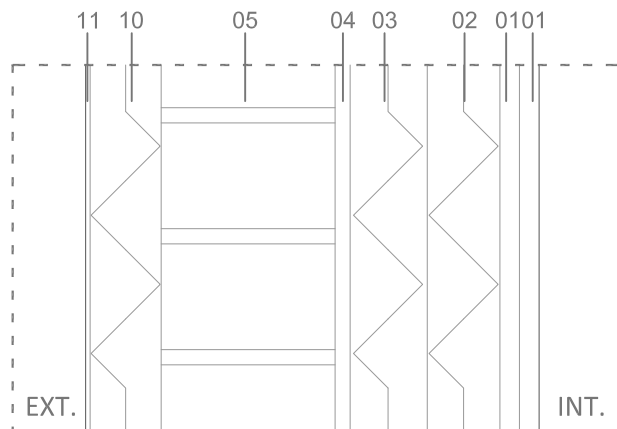


F02: FACHADA CHAPA

E_{total}=30cm

Resistencia a Fuego ≥ EI-120

Resistencia a Ruido = 55dBA / masa= 235kg/m²

- 01- Placa de yeso (e=1,3cm)
- 01- Placa de yeso (e=1,3cm)
- 02- Estructura de autoportante de pladur con lana de roca (e=4,8cm)
- 03- Aislamiento XPS (e=5cm)
- 04- Mortero hidrófugo (e=1cm)
- 05- 1/2 pie de ladrillo perforado (e=11,5cm)
- 10- Aislamiento EPS, (e=5cm), con anclajes de polipropileno y taco expansivo.
- 11- Acabado de chapa plegada.

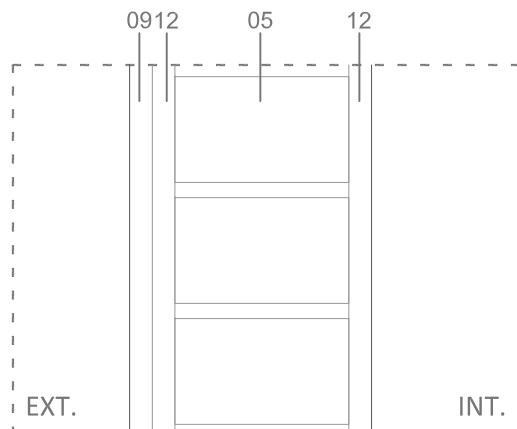


F03: FACHADA CASETÓN 1

E_{total}=16cm

Resistencia a Fuego ≥ EI-120

Resistencia a Ruido = 42dBA / masa= 150kg/m²

- 12- Enfoscado (e=1,5cm)
- 05- 1/2 pie de ladrillo perforado (e=11,5cm)
- 12- Enfoscado (e=1,5cm)
- 09- Mortero de acabado.

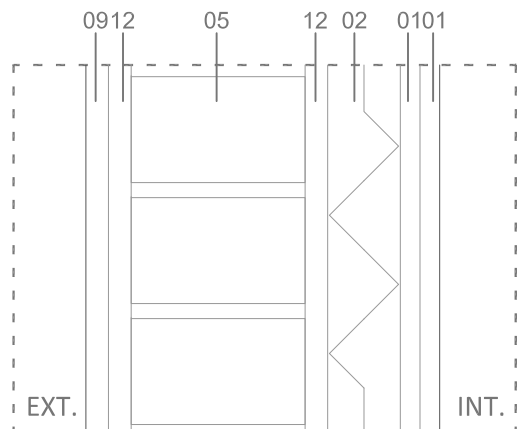


F04: FACHADA CASETÓN 2

E_{total}=23,4cm

Resistencia a Fuego ≥ EI-120

Resistencia a Ruido = 52dBA / masa= 175kg/m²

- 01- Placa de yeso (e=1,3cm)
- 01- Placa de yeso (e=1,3cm)
- 02- Estructura de autoportante de pladur con lana de roca (e=4,8cm)
- 04- Mortero hidrófugo (e=1,5cm)
- 05- 1/2 pie de ladrillo perforado (e=11,5cm)
- 12- Enfoscado (e=1,5cm)
- 09- Mortero de acabado.

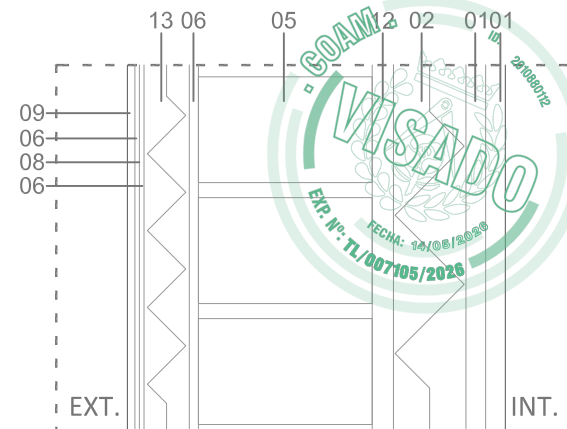


F03: FACHADA LISA

E_{total}=25cm

Resistencia a Fuego ≥ EI-120

Resistencia a Ruido = 55dBA / masa= 235kg/m²

- 01- Placa de yeso (e=1,3cm)
- 01- Placa de yeso (e=1,3cm)
- 02- Estructura de autoportante de pladur con lana de roca (e=4,8cm)
- 04- Mortero hidrófugo (e=1,5cm)
- 05- 1/2 pie de ladrillo perforado (e=11,5cm)
- 06- Mortero de agarre y regularización
- 13- Aislamiento EPS, (e=3cm), con anclajes de polipropileno y taco expansivo.
- 06- Mortero de agarre y regularización.
- 08- Malla de fibra de vidrio
- 06- Mortero de agarre y regularización.
- 09- Mortero de acabado.

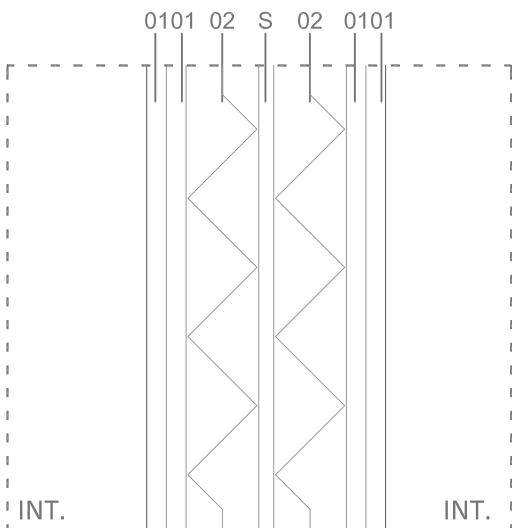


P01: PARTICIÓN ENTRE HAB. Y ENTRE HABITACIONES Y Z. COMUNES

E_{total}=15,8cm

Resistencia a Fuego ≥ EI-60

Resistencia a Ruido = 62,8dBA / masa=45kg/m²

- 01- Placa de yeso (e=1,3cm)
- 01- Placa de yeso (e=1,3cm)
- 02- Estructura autoportante de pladur con lana de roca (e=4,8cm)
- S- Separación de 1cm.
- 02- Estructura autoportante de pladur con lana de roca (e=4,8cm)
- 01- Placa de yeso (e=1,3cm)
- 01- Placa de yeso (e=1,3cm)

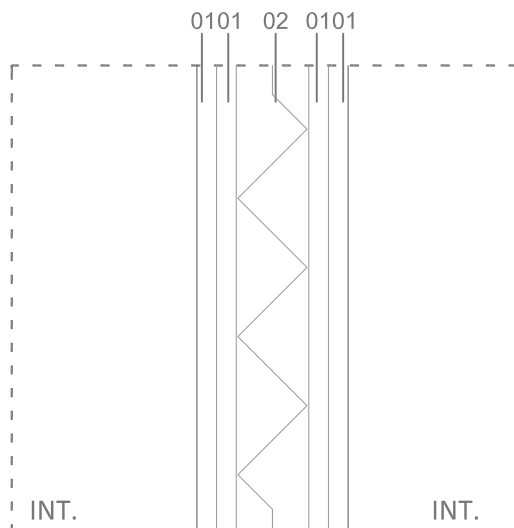


P02: PARTICIÓN INTERIOR

E_{total}=10cm

Resistencia a Fuego -

Resistencia a Ruido = 52dBA / m= 44kg/m²

- 01- Placa de yeso (e=1,3cm)
- 01- Placa de yeso (e=1,3cm)
- 02- Estructura autoportante de pladur con lana de roca (e=4,8cm)
- 01- Placa de yeso (e=1,3cm)
- 01- Placa de yeso (e=1,3cm)

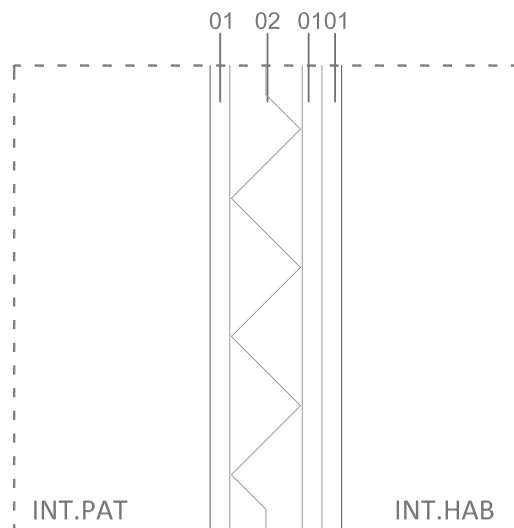


P03: PARTICIÓN ENTRE PATINILLOS Y HABITACIONES

E_{total}=8,7cm

Resistencia a Fuego -

Resistencia a Ruido = 26dBA / m= 43kg/m²

- 01- Placa de yeso (e=1,3cm)
- 02- Estructura autoportante de pladur con lana de roca (e=4,8cm)
- 01- Placa de yeso (e=1,3cm)
- 01- Placa de yeso (e=1,3cm)

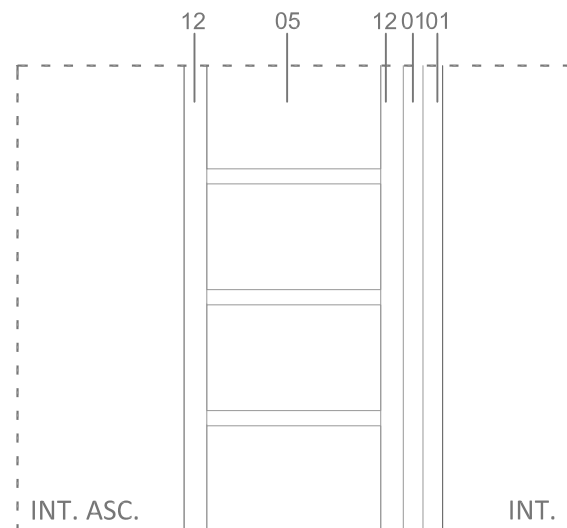


P04: PARTICIÓN ASCENSOR CON ZONAS COMUNES

E_{total}=17,1cm

Resistencia a Fuego ≥ EI-120

Resistencia a Ruido = 42dBA / m=150kg/m²

- 12- Enfoscado (e=1,5cm)
- 02- 1/2 pie de ladrillo perforado (e=11,5cm)
- 12- Enfoscado (e=1,5cm)
- 01- Placa de yeso (e=1,3cm)
- 01- Placa de yeso (e=1,3cm)

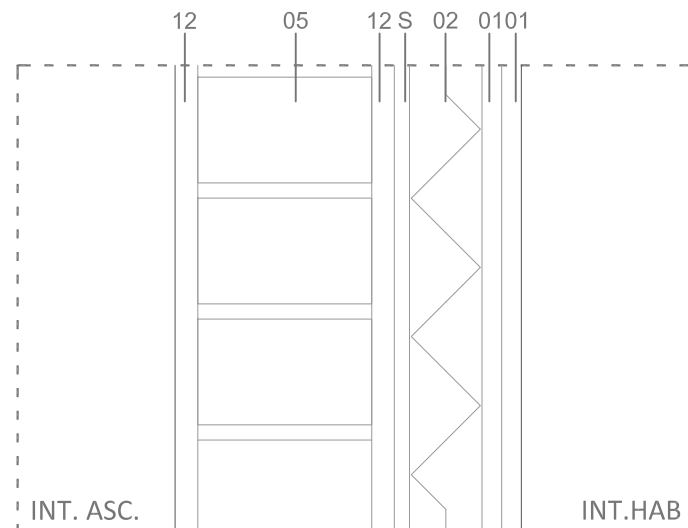


P05: PARTICIÓN ASCENSOR CON HABITACIONES

E_{total}=22,9cm

Resistencia a Fuego ≥ EI-120

Resistencia a Ruido = 60,7dBA / m=177kg/m²

- 12- Enfoscado (e=1,5cm)
- 05- 1/2 pie de ladrillo perforado (e=11,5cm)
- 12- Enfoscado (e=1,5cm)
- S- Separación de 1cm.
- 02- Estructura autoportante de pladur con lana de roca (e=4,8cm)
- 01- Placa de yeso (e=1,3cm)
- 01- Placa de yeso (e=1,3cm)

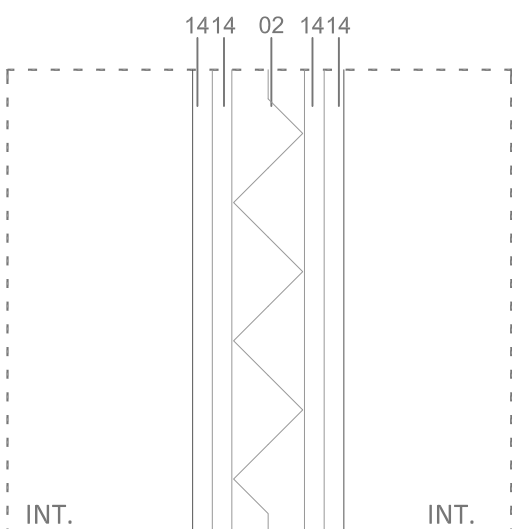


P06: PARTICIÓN INTERIOR ESCALERA CON DISTRIBUIDOR

E_{total}=10cm

Resistencia a Fuego - EI=120

Resistencia a Ruido = 52dBA / m= 44kg/m²

- 14- Placa de yeso RF (e=1,3cm)
- 14- Placa de yeso RF (e=1,3cm)
- 02- Estructura autoportante de pladur con lana de roca (e=4,8cm)
- 14- Placa de yeso RF (e=1,3cm)
- 14- Placa de yeso RF (e=1,3cm)

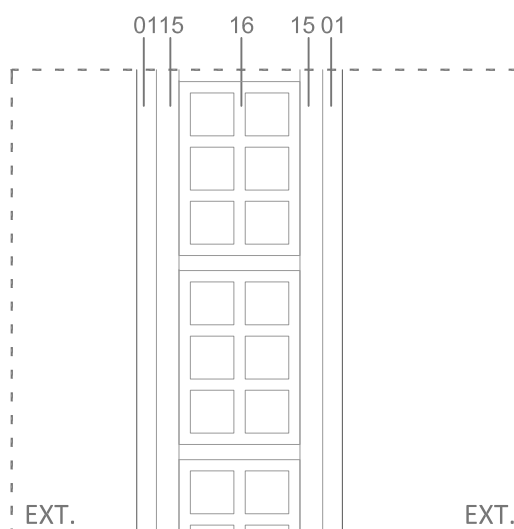


P07: PARTICIÓN CUARTO DE BASURAS

E_{total}=13,6cm

Resistencia a Fuego ≥ EI-120

Resistencia a Ruido = 42,7dBA / m=103,5kg/m²

- 01- Placa de yeso (e=1,3cm)
- 15- Guarnecido (e=1,5cm)
- 16- Ladrillo hueco doble (e=8cm)
- 15- Guarnecido (e=1,5cm)
- 01- Placa de yeso (e=1,3cm)

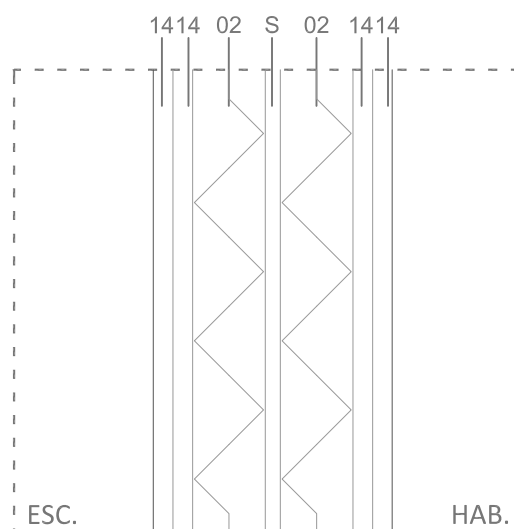

P08: PARTICIÓN ENTRE ESCALERA Y HABITACIONES

E_{total}=15,8cm

Resistencia a Fuego ≥ EI-120

Resistencia a Ruido = 62,8dBA / m=50kg/m²

- 14- Placa de yeso RF (e=1,3cm)
- 14- Placa de yeso RF (e=1,3cm)
- 02- Estructura autoportante de pladur con lana de roca (e=4,8cm)
- S- Separación de 1cm.
- 02- Estructura autoportante de pladur con lana de roca (e=4,8cm)
- 14- Placa de yeso RF (e=1,3cm)
- 14- Placa de yeso RF (e=1,3cm)



APUNTOARQUITECTURA
teléfono: 6 49 6 1 2 4 4 9
www.apuntoarquitectura.com
oficina@apuntoarquitectura.com

PROYECTO
PROYECTO BÁSICO DE OBRAS PARA EL CAMBIO DE
USO DE EDIFICIO RESIDENCIAL A TERCARIO
HOSPEDAJE. LICENCIA DE ACTIVIDAD_
HOTEL DE 2 ESTRELLAS. CI. Haro 5; 28043 Madrid

TITULAR
HARO 5 VENTURES S.L.
N.I.F.: B22599070
REPRESENTANTE
Rafael Garrido Rodrigo
D.N.I.: 00839470Q

TÉCNICO
Jorge Serrano de La Torre
COLEGIADO COAM 17.677

DESCRIPCIÓN
CONSTRUCCIÓN: Particiones verticales

NÚMERO DE PLANO FECHA

C03


17.04.2026

ESCALA


1:5




QR validation

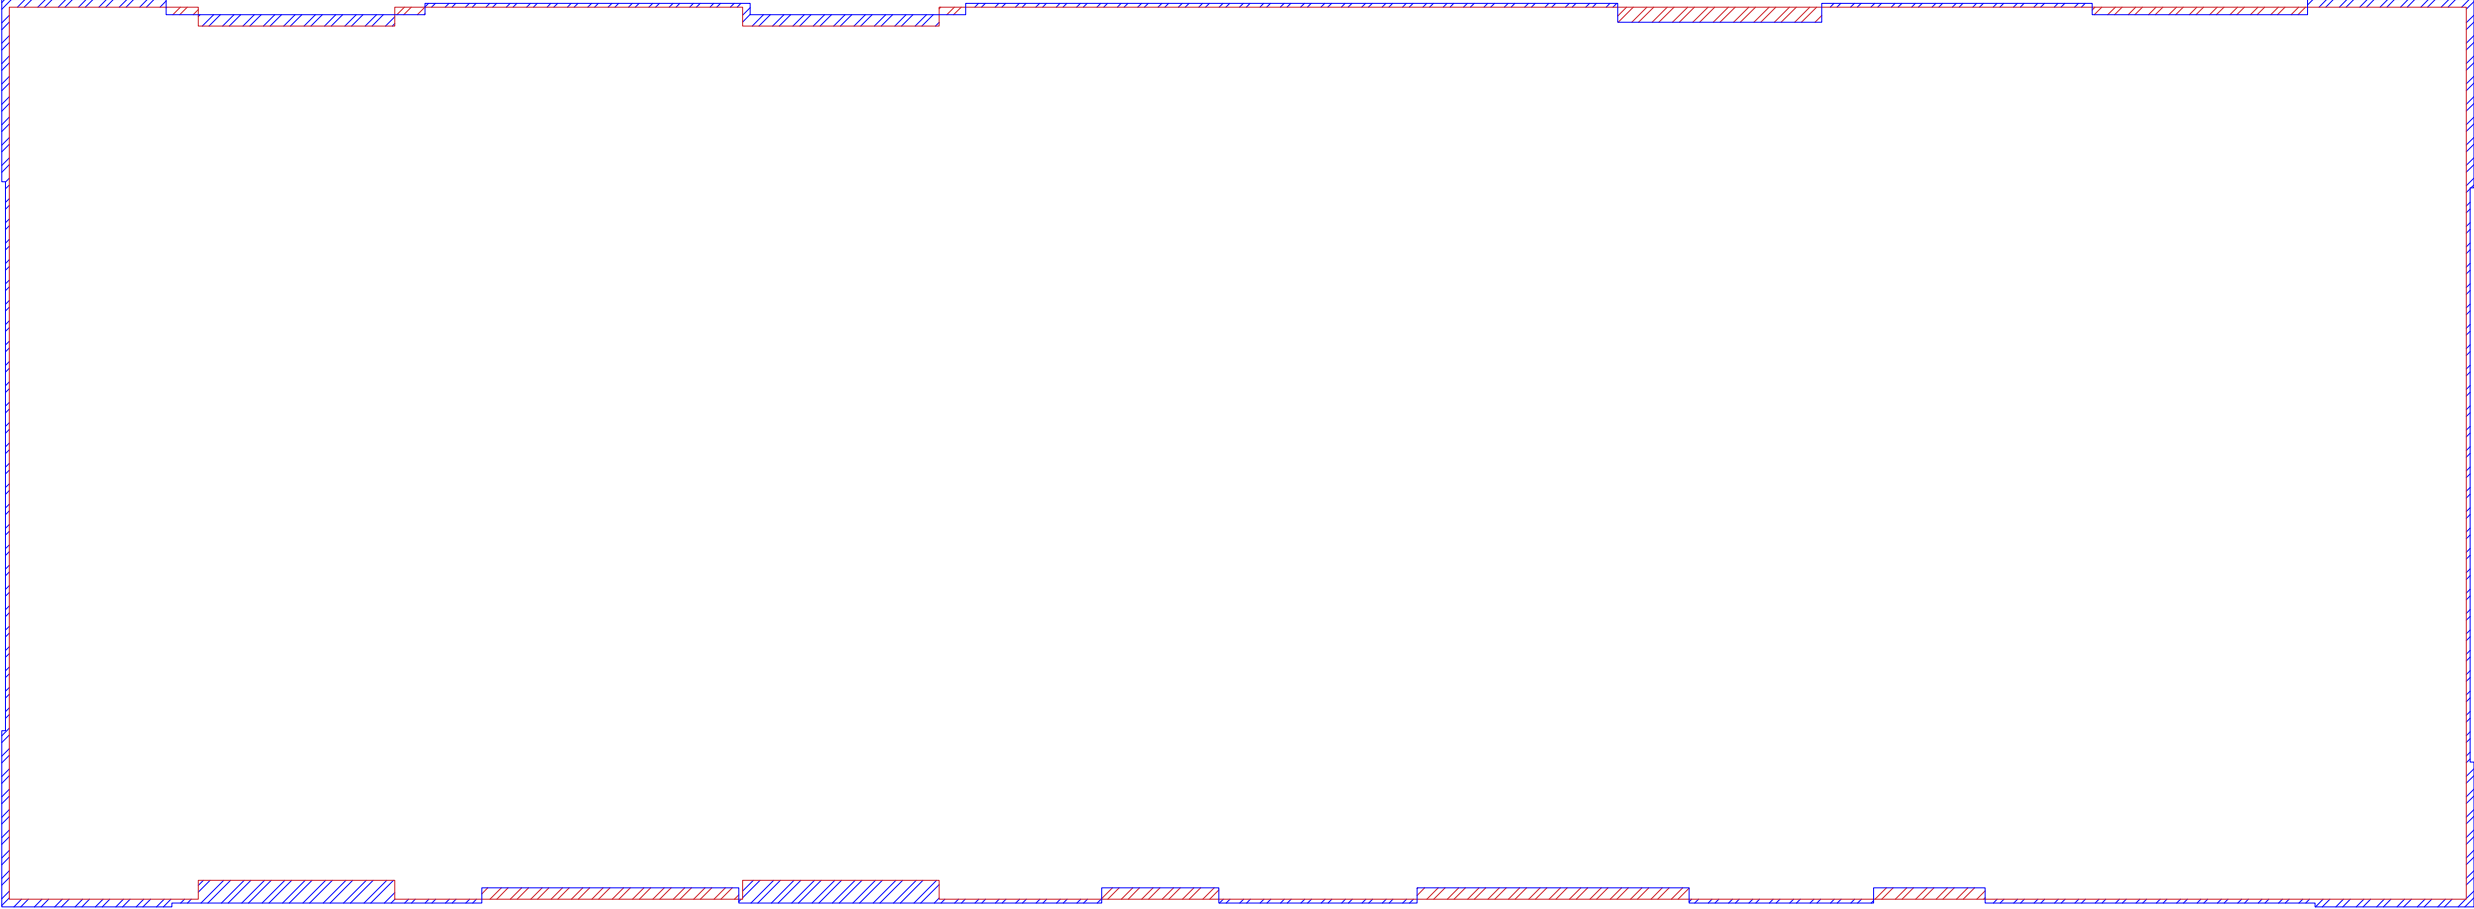

PLANTA SEGUNDA

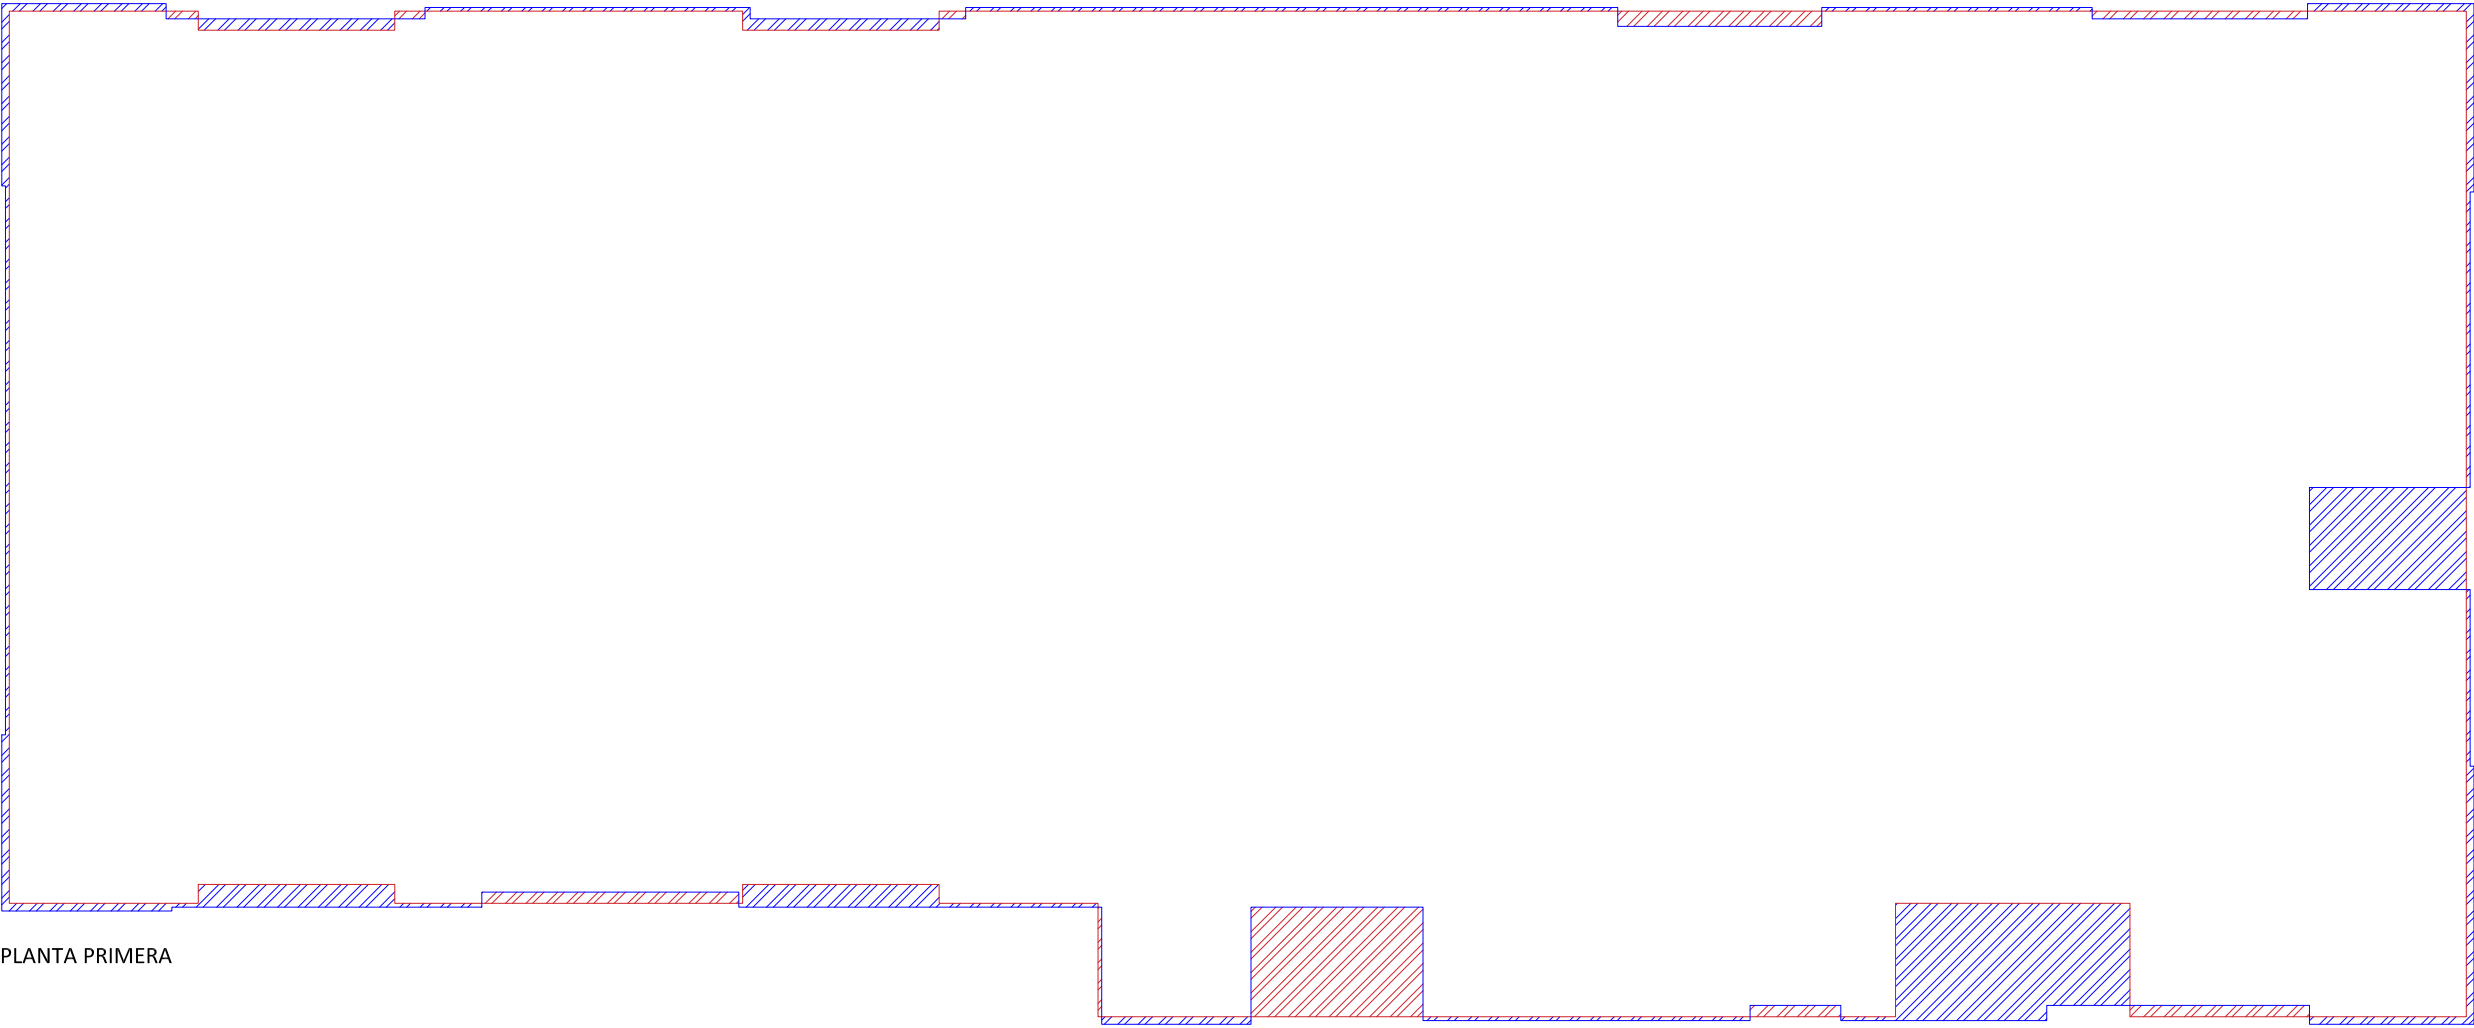


PLANTA PRIMERA

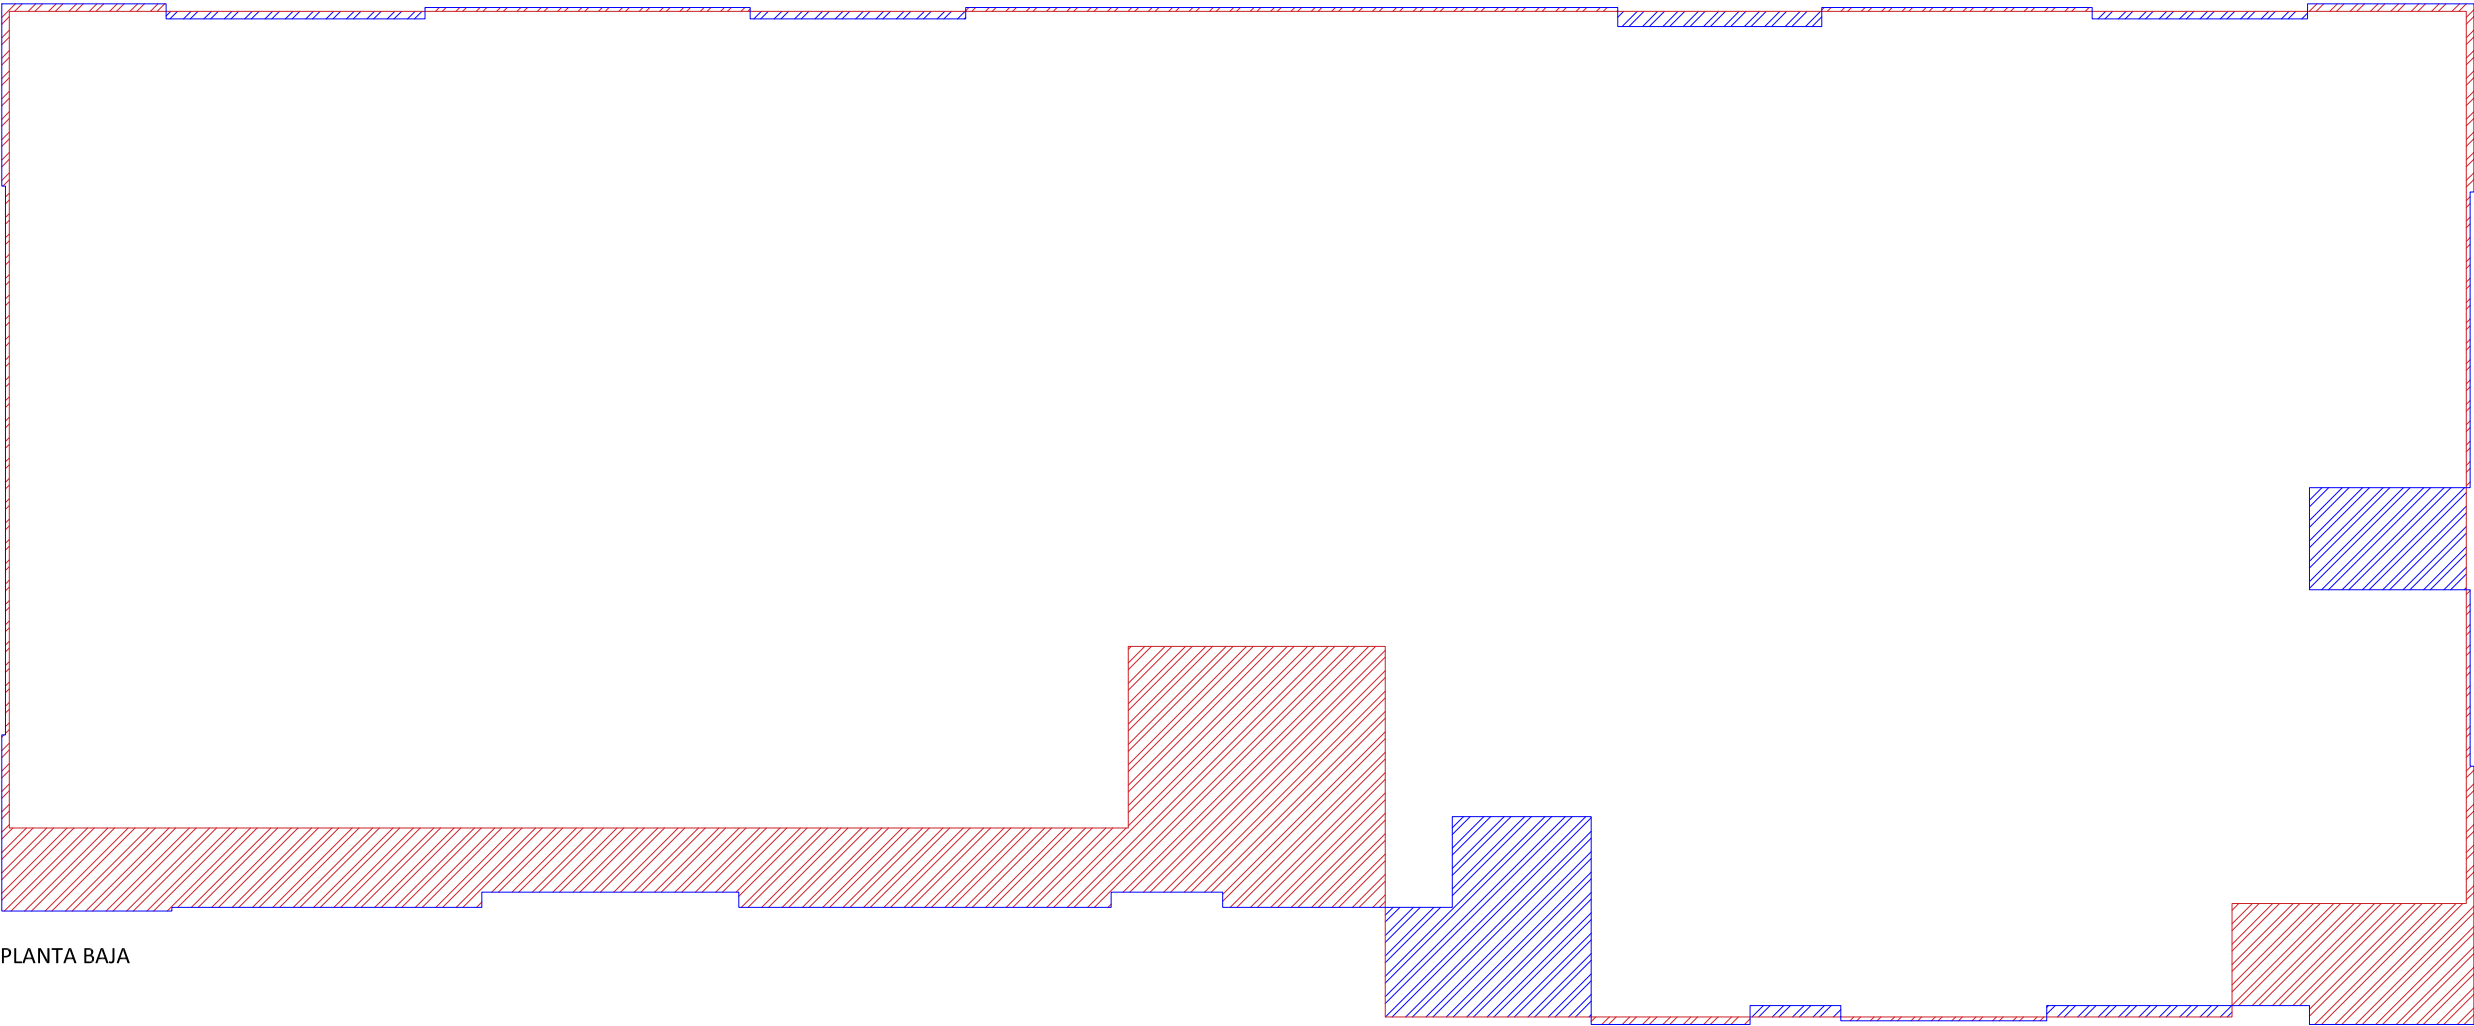

PLANTA BAJA

- REFORMADO
- DEMOLICIÓN
- ACTUAL
- CONSTRURCCIÓN

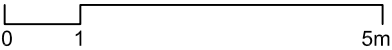

APUNTOARQUITECTURA
teléfono: 6 4 9 6 1 2 4 4 9
www.apuntoarquitectura.com
oficina@apuntoarquitectura.com

PROYECTO
PROYECTO BÁSICO DE OBRAS PARA EL CAMBIO DE
USO DE EDIFICIO RESIDENCIAL A TERCIARIO
HOSPEDAJE. LICENCIA DE ACTIVIDAD_
HOTEL DE 2 ESTRELLAS. Cl. Haro 5; 28043 Madrid
TITULAR
HARO 5 VENTURES S.L.
N.I.F.: B22599070
REPRESENTANTE
Rafael Garrido Rodrigo
D.N.I.: 00839470Q

TÉCNICO
Jorge Serrano de La Torre
COLEGIADO COAM 17.677

DESCRIPCIÓN

CONSTRUCCIÓN: Actuaciones en fachada

NÚMERO DE PLANO

FECHA

ESCALA

C04

17.04.2026

1:100



Sup. de iluminación: 1.72m²
Sup. de ventilación: 2.02m²

PVC		
ANCHO 1000	ALTO 2350	VIDRIO alslante RPT (4+12+6)
1 HOJA OSCILOBATIENTE		
color gris		
Manillas y pernios		
-		
46 UD		

Sup. de iluminación: 0.92m²
Sup. de ventilación: 1.13m²

PVC		
ANCHO 1000	ALTO 1350	VIDRIO alslante RPT (4+12+6)
1 HOJA OSCILOBATIENTE		
color gris		
Manillas y pernios		
-		
1 UD		

Sup. de iluminación: 0.80m²

PVC		
ANCHO 500	ALTO 2350	VIDRIO alslante RPT (4+12+6)
1 HOJA FIJA		
color gris		
Manillas y pernios		
-		
2 UD		

Sup. de iluminación: 1.00m²
Sup. de ventilación: 0.69m²

PVC		
ANCHO 700	ALTO 2350	VIDRIO alslante RPT (4+12+6)
1 HOJA OSCILOBATIENTE y 1 HOJA FIJA		
color gris		
Manillas y pernios		
-		
10 UD		

Sup. de iluminación: 1.00m²
Sup. de ventilación: 0.69m²

PVC		
ANCHO 700	ALTO 2350	VIDRIO alslante RPT (4+12+6)
1 HOJA OSCILOBATIENTE y 1 HOJA FIJA		
color gris		
Manillas y pernios		
-		
2 UD		

Sup. de iluminación: 0.36m²
Sup. de ventilación: 0.75m²


PVC		
ANCHO 600	ALTO 1250	VIDRIO alslante RPT (4+12+6)
1 HOJA OSCILOBATIENTE		
color gris		
Manillas y pernios		
-		
12 UD		


Sup. de iluminación: 0.76m²
Sup. de ventilación: 1.02m²

PVC		
ANCHO 2150	ALTO 1050	VIDRIO alslante RPT (4+12+6)
1 HOJA FIJA Y 1 HOJA BATIENTE		
color gris		
Manillas y pernios		
-		
3 UD		


Sup. de iluminación: 1.32m²
Sup. de ventilación: 1.57m²

PVC		
ANCHO 1000	ALTO 1850	VIDRIO alslante RPT (4+12+6)
1 HOJA OSCILOBATIENTE		
color gris		
Manillas y pernios		
-		
1 UD		

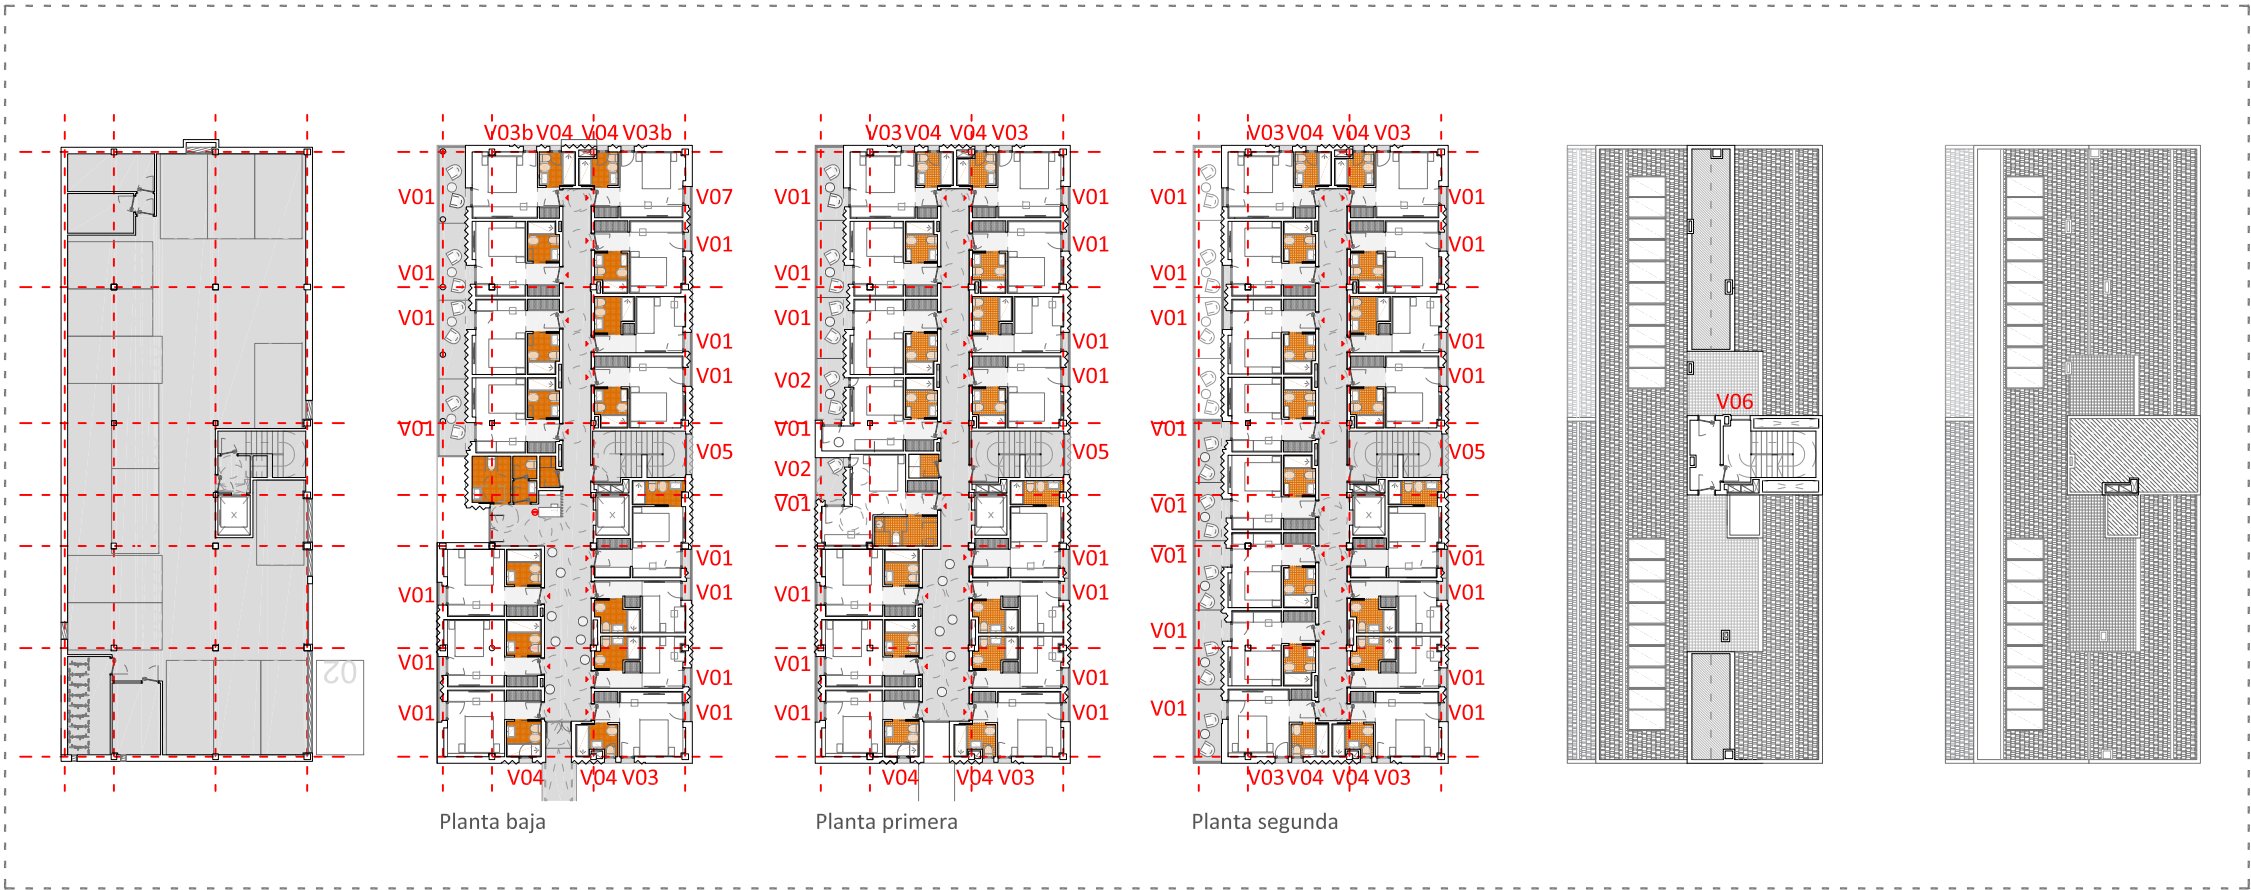


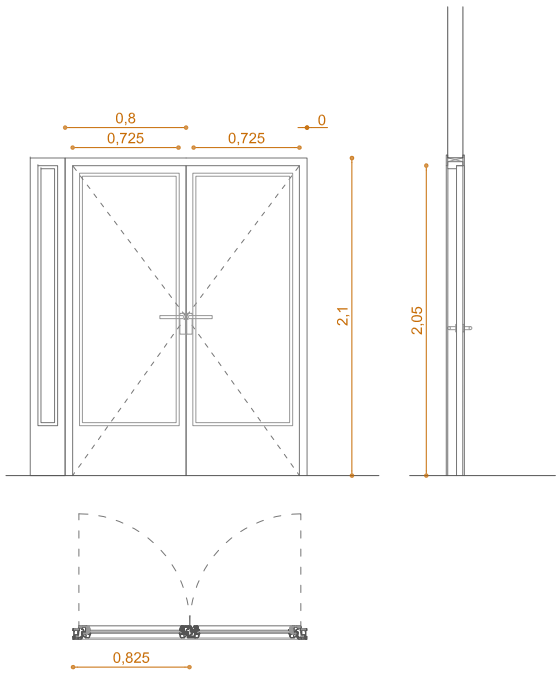


P01	
Nº	1 unidad
Dimensiones hoja (A x H mm)	Puertas de acceso Hoja (825 x 2050)
Hoja	Vidrio aislante RPT (4+12+6)
Preferencia	Acero
Varios	Cerraduras de seguridad

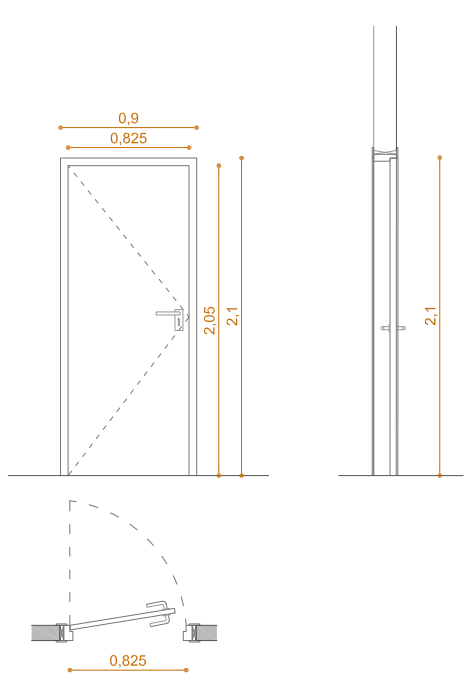


P02	
Nº	7 unidades
Dimensiones hoja (A x H mm)	Puertas de paso RF Hoja (825 x 2050)
Hoja	Madera
Preferencia	Madera
Varios	Cerraduras de seguridad, EI-60

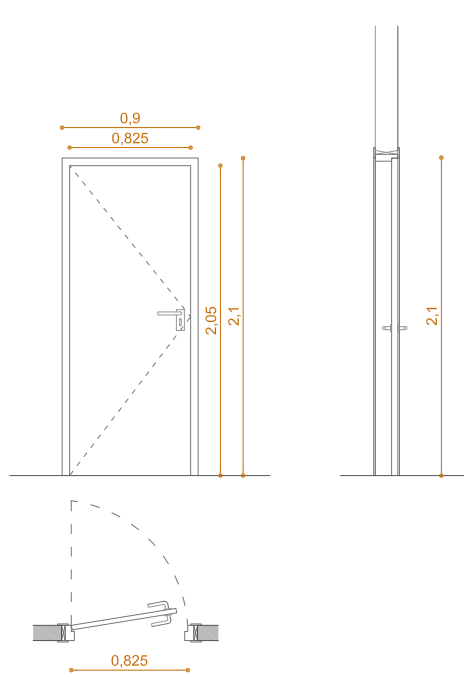


P03	
Nº	49 unidades
Dimensiones hoja (A x H mm)	Puerta de acceso a habitaciones RF Hoja (825 x 2050)
Hoja	Madera lacada en blanco
Preferencia	Madera
Varios	Cerraduras de seguridad, EI-30

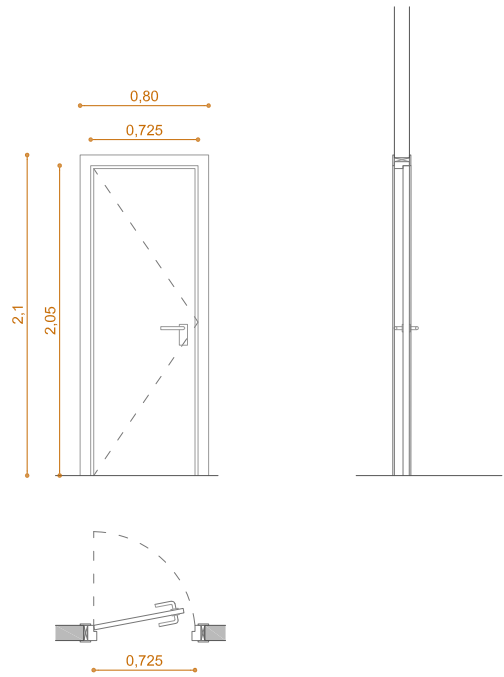


P04	
Nº	2 unidades
Dimensiones hoja (A x H mm)	Puerta de acceso de paso Hoja (725 x 2050)
Hoja	Madera lacada en blanco
Preferencia	Madera
Varios	Pestillo

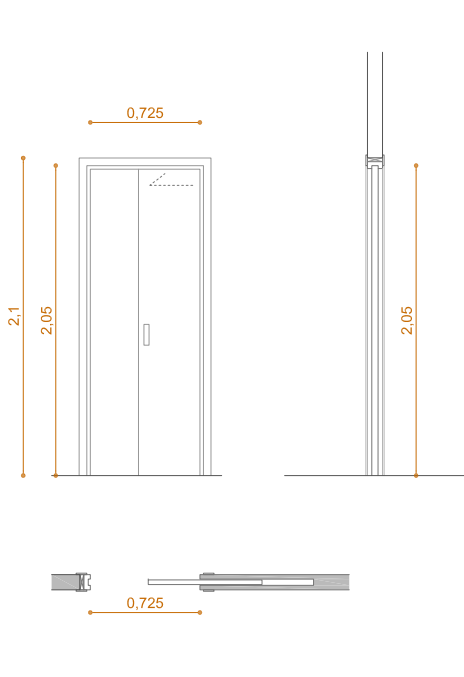


P05	
Nº	46 unidades
Dimensiones hoja (A x H mm)	Puerta corredera Hoja (725 x 2050)
Hoja	Madera lacada en blanco
Preferencia	Madera
Varios	Pestillo

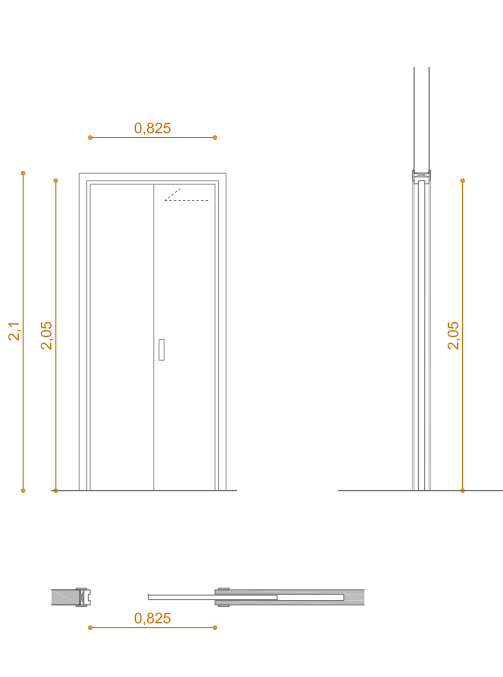


P06	
Nº	2 unidades
Dimensiones hoja (A x H mm)	Puerta corredera accesible Hoja (825 x 2050)
Hoja	Madera lacada en blanco
Preferencia	Madera
Varios	Pestillo

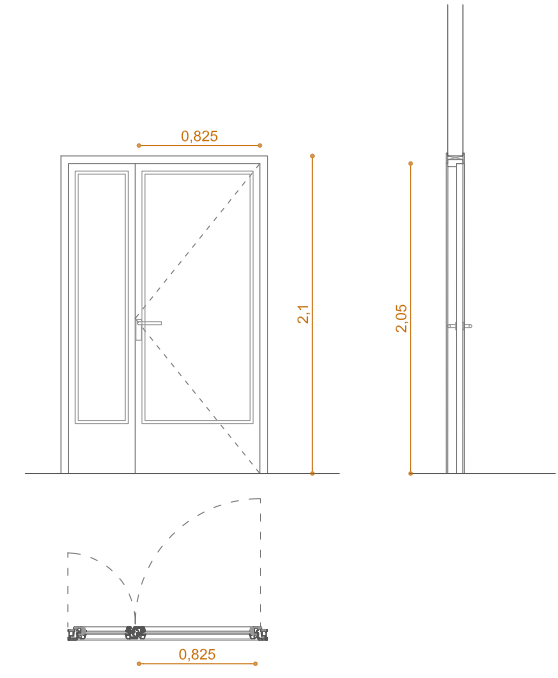


P07	
Nº	2 unidades
Dimensiones hoja (A x H mm)	Puertas de acceso Hoja (825 x 2050)
Hoja	Vidrio aislante RPT (4+12+6)
Preferencia	Acero
Varios	Cerraduras de seguridad

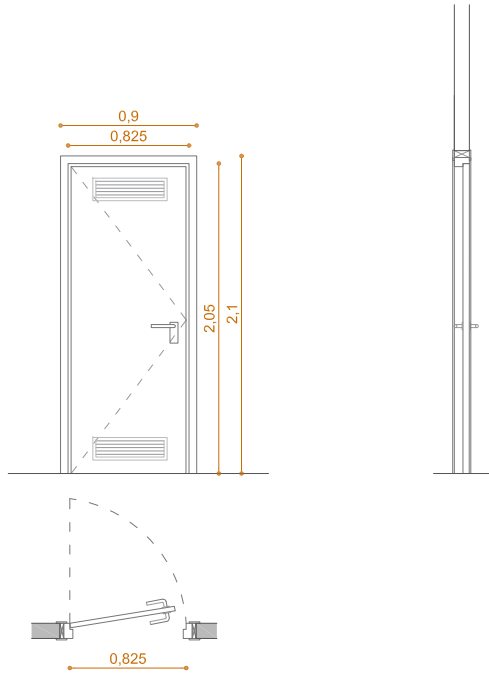


P08	
Nº	6 unidades
Dimensiones hoja (A x H mm)	Puertas de cuarto de instalaciones Hoja (825 x 2050)
Hoja	Acero galvanizado. Acabado esmalte sintético
Preferencia	Acero galvanizado
Varios	Cerraduras de seguridad, manillas, pernos, rejillas de ventilación

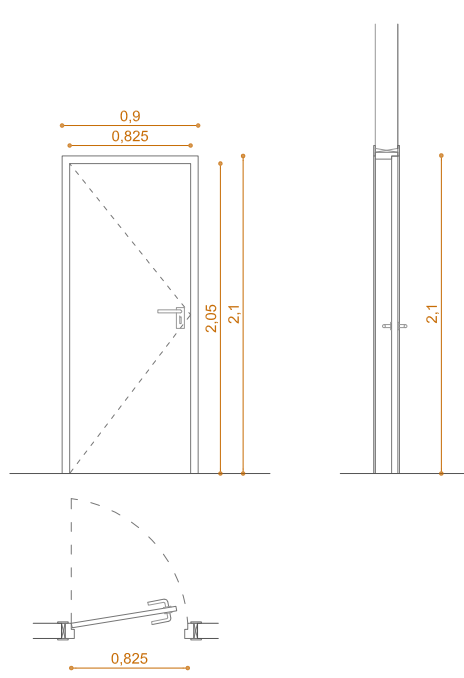


P09	
Nº	2 unidades
Dimensiones hoja (A x H mm)	Puerta de acceso Hoja (825 x 2050)
Hoja	Madera lacada en blanco
Preferencia	Madera
Varios	Pestillo

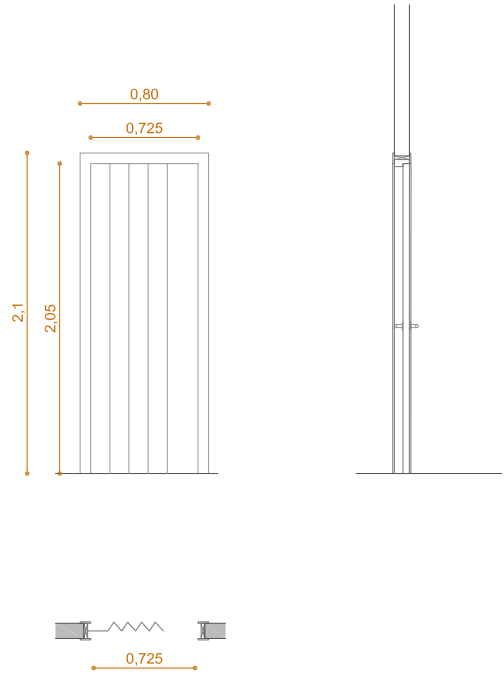

P10	
Nº	1 unidad
Dimensiones hoja (A x H mm)	Puerta de acceso Hoja (725 x 2050)
Hoja	Madera lacada en blanco
Preferencia	Madera
Varios	Pestillo

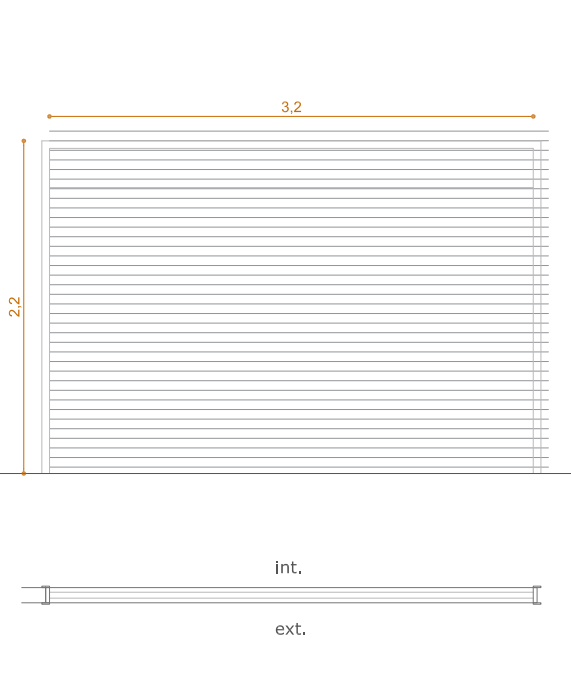

P09	
Nº	1 unidad
Dimensiones hoja (A x H mm)	Puertas de vehículo Hoja motorizada remota
Hoja	Acero galvanizado. Acabado esmalte sintético
Preferencia	Acero galvanizado
Varios	Cerraduras de seguridad, manillas y pernos. Dispone de sist de seguridad que provoque su parada en caso de existir algún obstáculo.

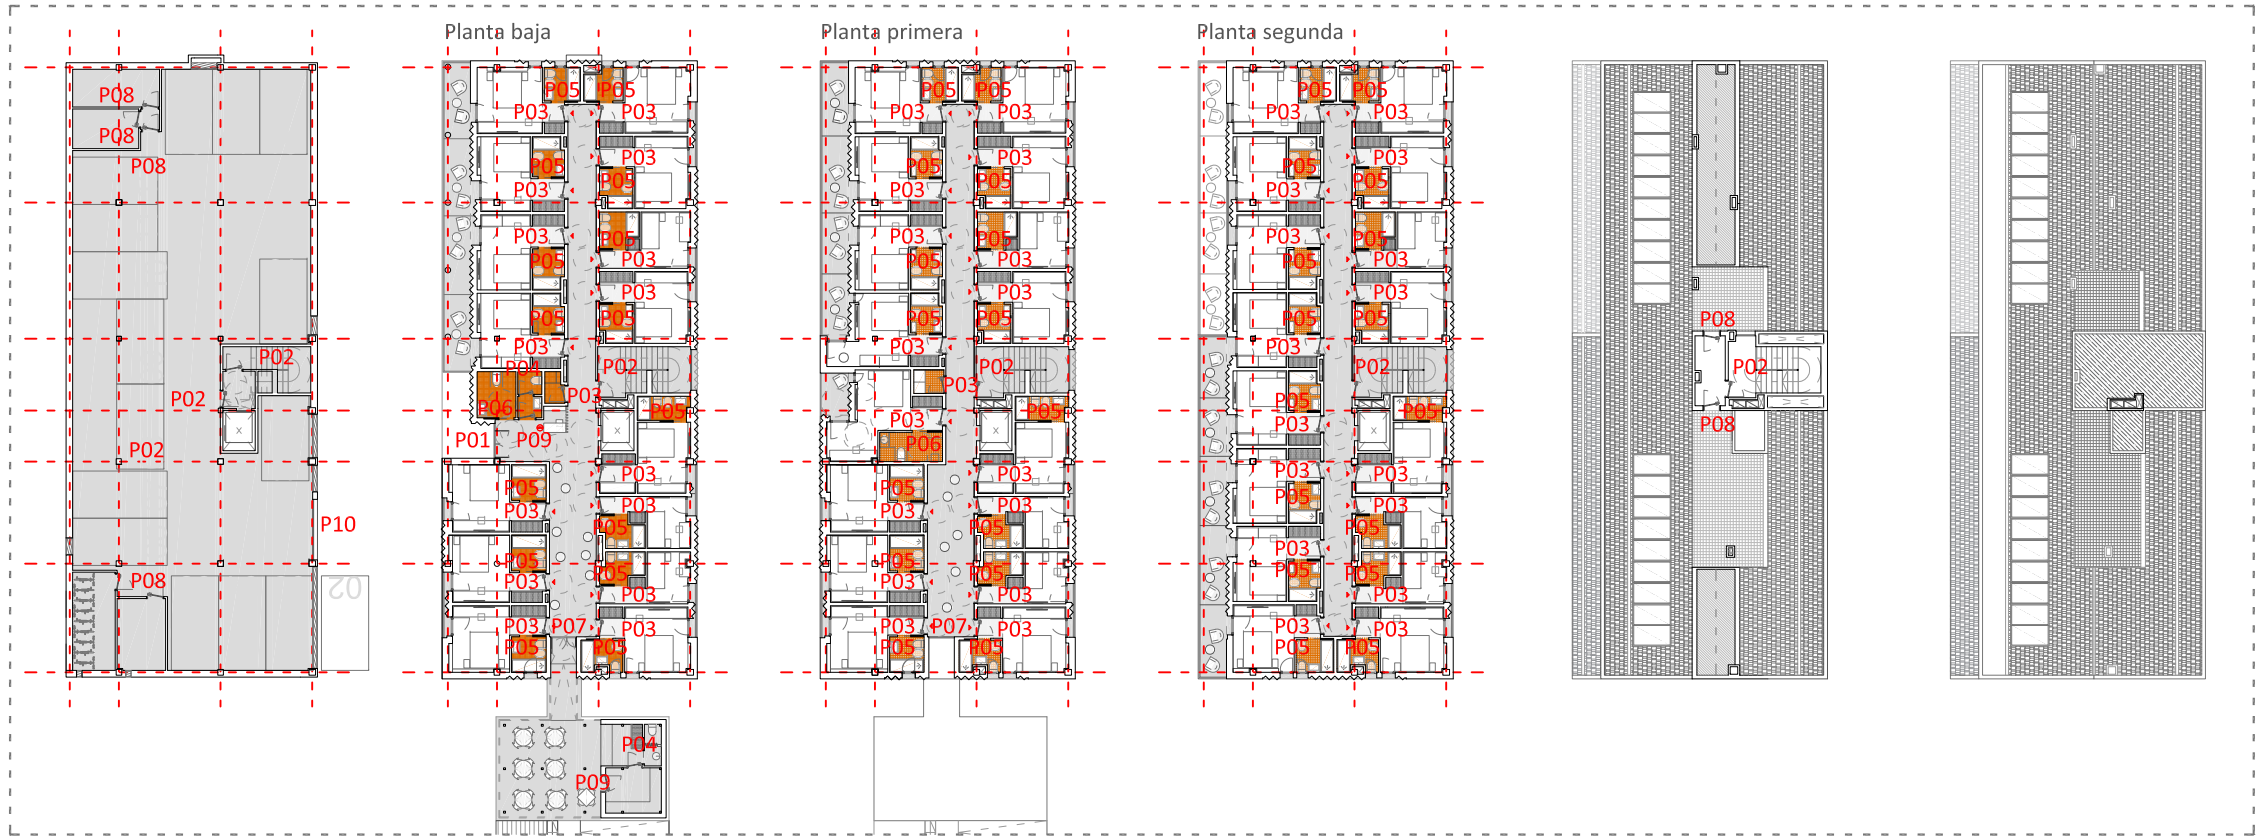

0 1 3m

APUNTOARQUITECTURA
teléfono: 649612449
www.apuntoarquitectura.com
oficina@apuntoarquitectura.com

PROYECTO
PROYECTO BÁSICO DE OBRAS PARA EL CAMBIO DE
USO DE EDIFICIO RESIDENCIAL A TERCIARIO
HOSPEDAJE. LICENCIA DE ACTIVIDAD_
HOTEL DE 2 ESTRELLAS. Cl. Haro 5; 28043 Madrid
TITULAR
HARO 5 VENTURES S.L.
N.I.F.: B22599070
REPRESENTANTE
Rafael Garrido Rodrigo
D.N.I.: 00839470Q


TÉCNICO
Jorge Serrano de La Torre
COLEGIADO COAM 17.677
DESCRIPCIÓN
CONSTRUCCIÓN: Carpinterías 2

NÚMERO DE PLANO FECHA ESCALA

C06 17.04.2026 1:50




QR verification

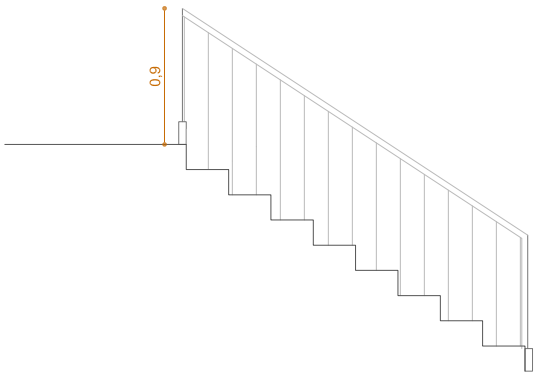

20mm barroses-40mm pasamanos	
LARGO TOTAL 3002	ALTO 900
Barandilla de acero. Barroses de 860mm de alto.	
Color gris oscuro RAL 7016 o similar	
Anclajes	
Atornillada a paramentos	
Escaleras	

C-02

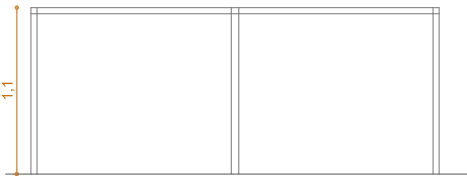


40mm pasamanos	
LARGO TOTAL 98,35	ALTO 1100
Barandilla de acero. Vidrio de 1060mm de alto.	
Color gris oscuro RAL 7016 o similar	
Anclajes	
Atornillada a paramentos	
Escaleras	

C-02




40mm pasamanos	
LARGO TOTAL 95,6	ALTO 1100
Barandilla de acero. Vidrio de 1060mm de alto.	
Color gris oscuro RAL 7016 o similar	
Anclajes	
Atornillada a paramentos	
Exterior	

C-04

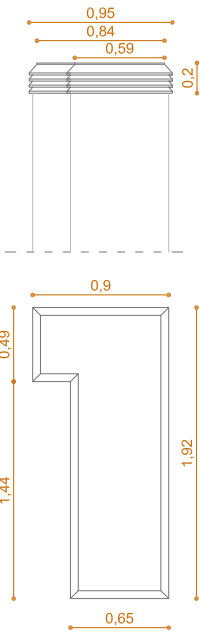

ANCHO x LARGO 90 x 1920	ALTO 200	GRUESO 2
Lamas de aluminio		
Aluminio color negro		
Uniones soldadas		
Remate chimenea		
1 UD : Chimenea		

C-05

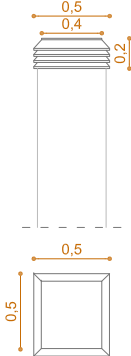







ALTO 200	ANCHO	500 x 500	750 x 340
GRUESO 2		400 x 440	650 x 340
		600 x 550	750 x 410
Lamas de aluminio			
Aluminio color negro			
Uniones soldadas			
Remate chimenea			
6 UD : Chimenea			

C-06



ALTO 200	ANCHO	1400 x 500	2300 x 500
GRUESO 2		900 x 500	1630 x 350
		300 x 300	1150 x 500
Rejilla de ventilación del garaje			
5 UDS			



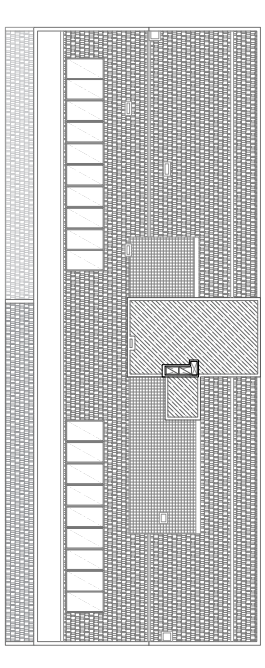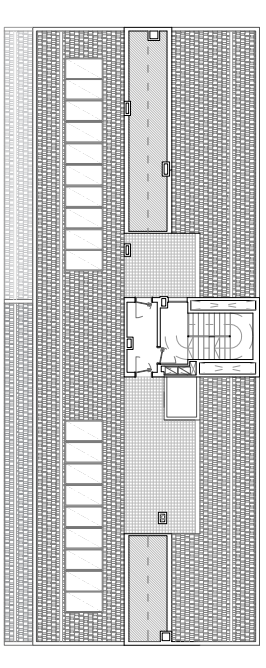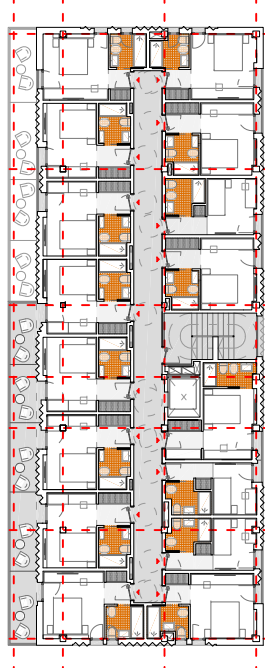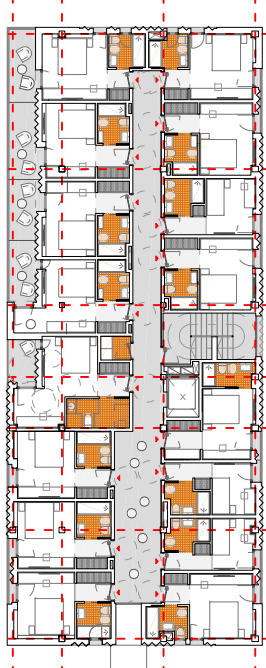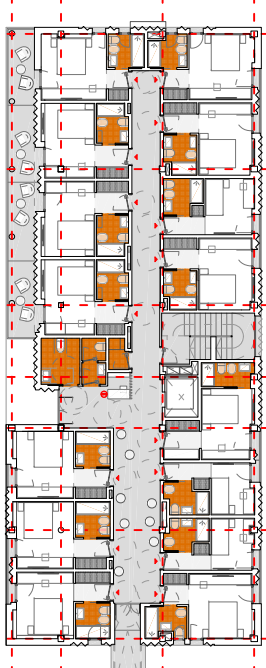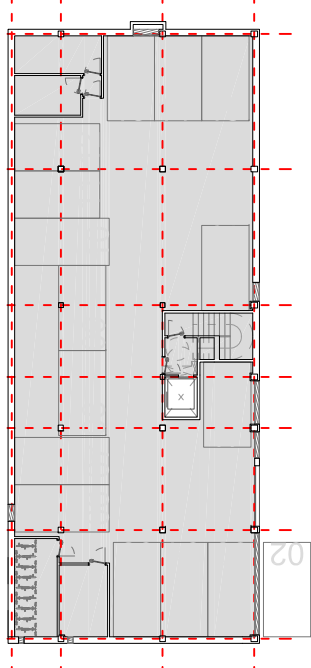

Planta bajaPlanta primeraPlanta segunda

013m

013m

APUNTOARQUITECTURA

teléfono: 649612449

www.apuntoarquitectura.com

oficina@apuntoarquitectura.com

PROYECTO

PROYECTO BÁSICO DE OBRAS PARA EL CAMBIO DE

USO DE EDIFICIO RESIDENCIAL A TERCIARIO

HOSPEDAJE. LICENCIA DE ACTIVIDAD_

HOTEL DE 2 ESTRELLAS. Cl. Haro 5; 28043 Madrid

TITULAR

HARO 5 VENTURES S.L.

N.I.F.: B22599070

REPRESENTANTE

Rafael Garrido Rodrigo

D.N.I.: 00839470Q

TÉCNICO

Jorge Serrano de La Torre

COLEGIADO COAM 17.677

DESCRIPCION

CONSTRUCCION: Carpinterías 3

NÚMERO DE PLANO

FECHA

ESCALA

C07

17.04.2026

1:50

