


29.00
28.00
27.00
26.00
25.00
24.00
23.00
22.00
21.00
20.00
19.00
18.00
17.00
16.00
15.00
14.00
13.00
12.00
11.00
10.00
9.00
8.00
7.00
6.00
5.00
4.00
3.00

ALÇADO NASCENTE



29.00
28.00
27.00
26.00
25.00
24.00
23.00
22.00
21.00
20.00
19.00
18.00
17.00
16.00
15.00
14.00
13.00
12.00
11.00
10.00
9.00
8.00
7.00
6.00
5.00
4.00
3.00

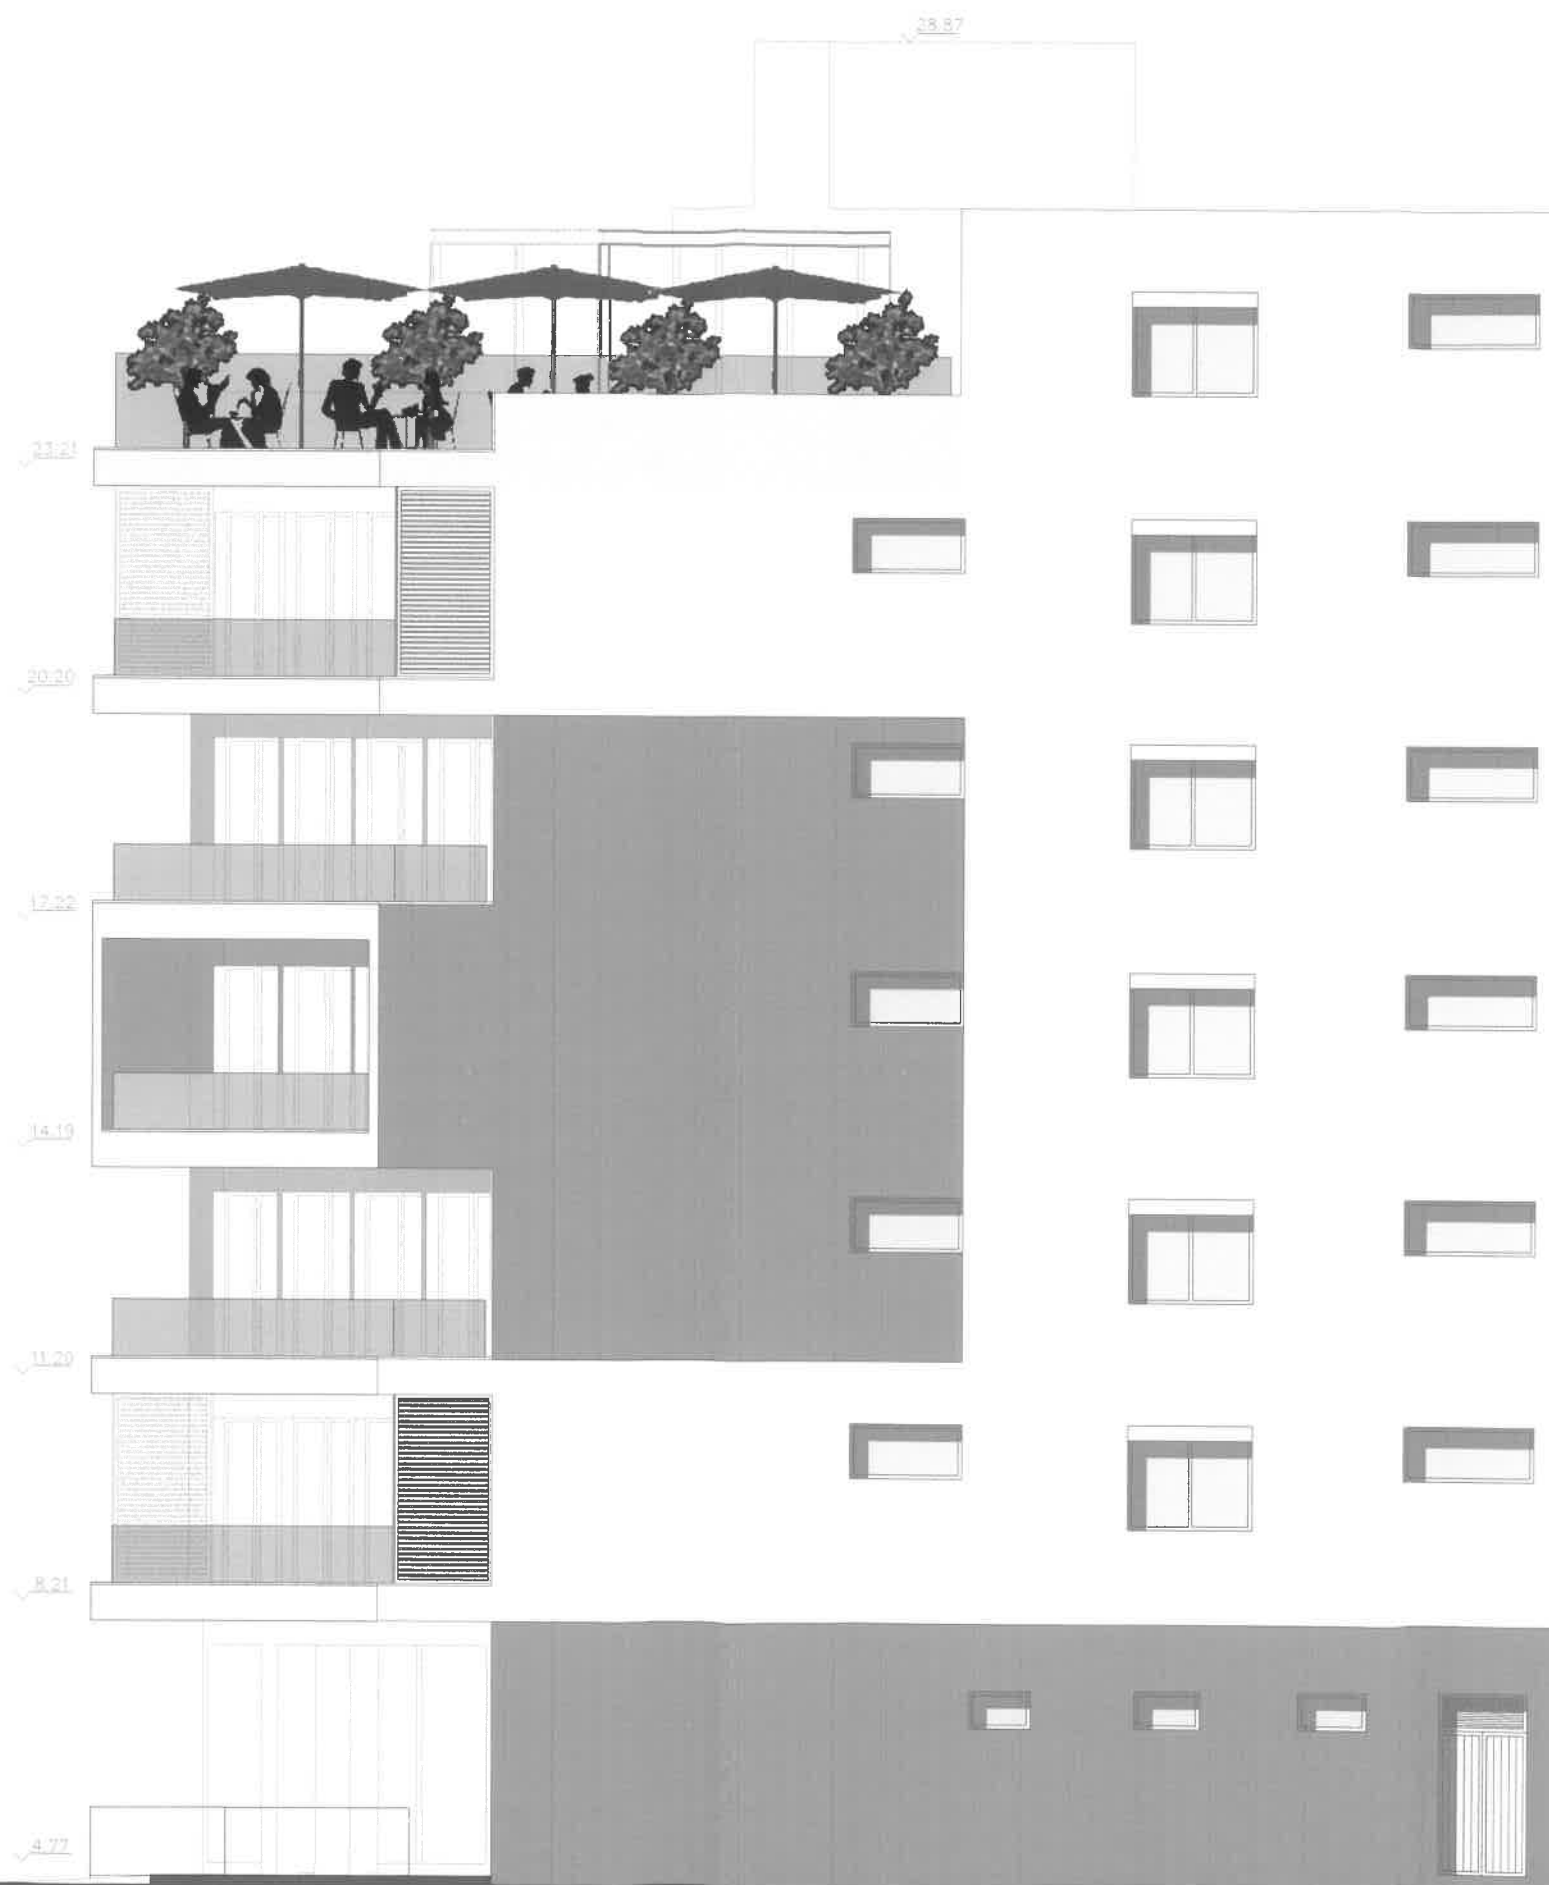

23.21
20.30
17.22
14.13
11.20
8.21
4.77

ALÇADO NASCENTE

29.00
28.00
27.00
26.00
25.00
24.00
23.00
22.00
21.00
20.00
19.00
18.00
17.00
16.00
15.00
14.00
13.00
12.00
11.00
10.00
9.00
8.00
7.00
6.00
5.00
4.00
3.00

Pérgula em estrutura metálica pintada de branco com cobertura retrátil
RAL 9010

Lamelas de proteção

Guarda de vidro temperado laminado

Fachada isolada com sistema tipo "capotto" e revestimento cor branco
RAL 9010

Lamelas de madeira com estrutura de alumínio, acabamento em madeira natural

Janelas de alumínio cor natural, com vidro duplo e lamelas retráteis cor cinza claro

Fachada isolada com sistema tipo "capotto" e revestimento cor branco
RAL 9010

Fachada isolada com sistema tipo "capotto" e revestimento cor castanho "acinzentado"
RAL 8019

Guarda de vidro temperado laminado

Fachada isolada com sistema tipo "capotto" e revestimento cor castanho "acinzentado"
RAL 8019

Fachada isolada com sistema tipo "capotto" e revestimento cor castanho "acinzentado"
RAL 8019

Fachada revestida com painel fenólico aspecto madeira

Janelas de vidro temperado

ALÇADO SUL

28.87

23.21

20.20


17.22

14.19

11.20


8.21

4.22

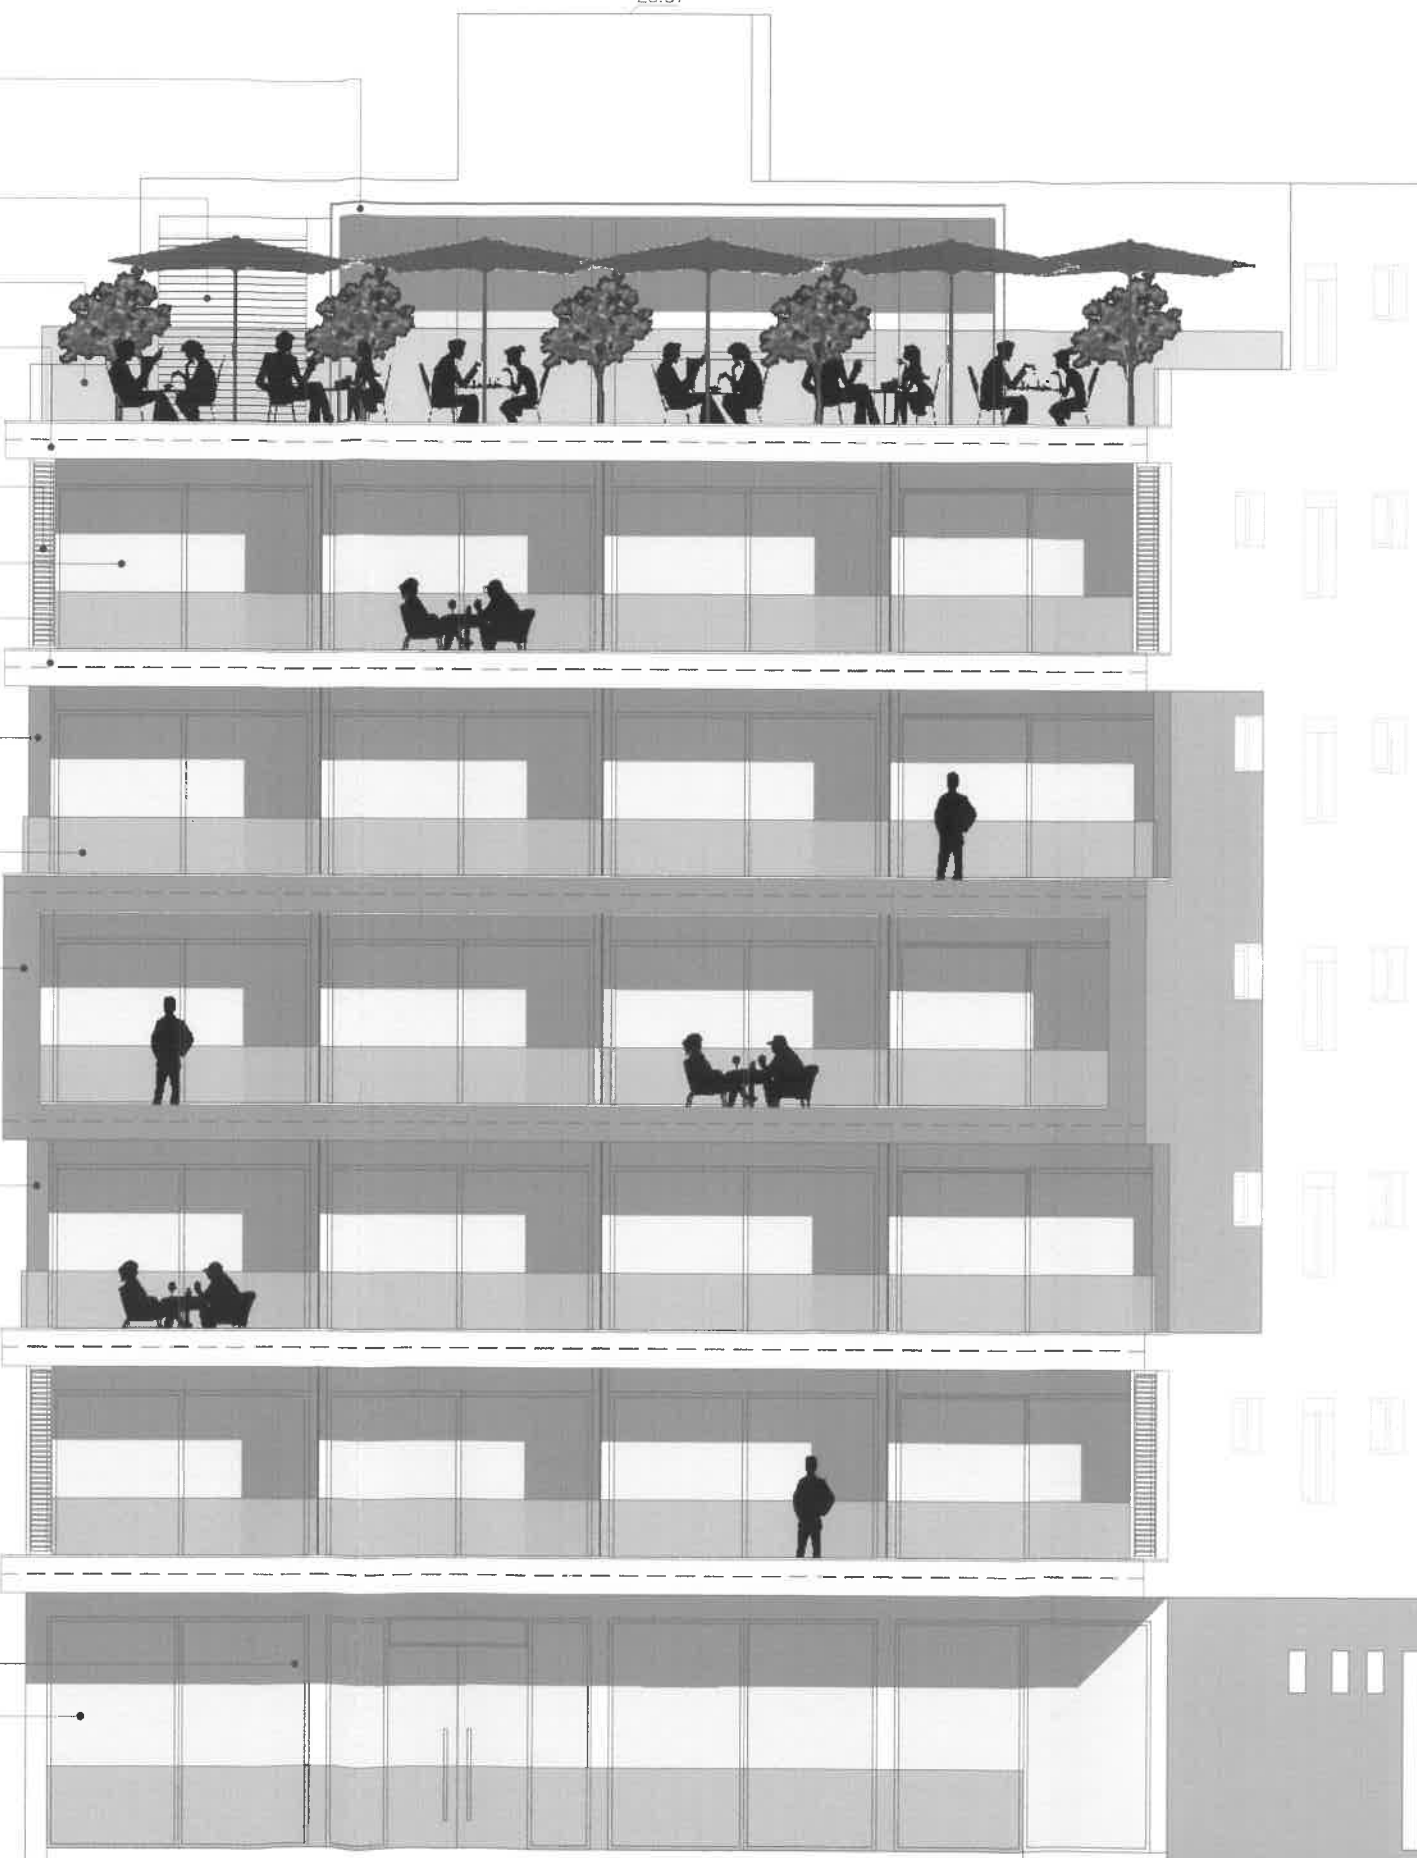


29.00
28.00
27.00
26.00
25.00
24.00
23.00
22.00
21.00
20.00
19.00
18.00
17.00
16.00
15.00
14.00
13.00
12.00
11.00
10.00
9.00
8.00
7.00
6.00
5.00
4.00
3.00

ALÇADO SUL

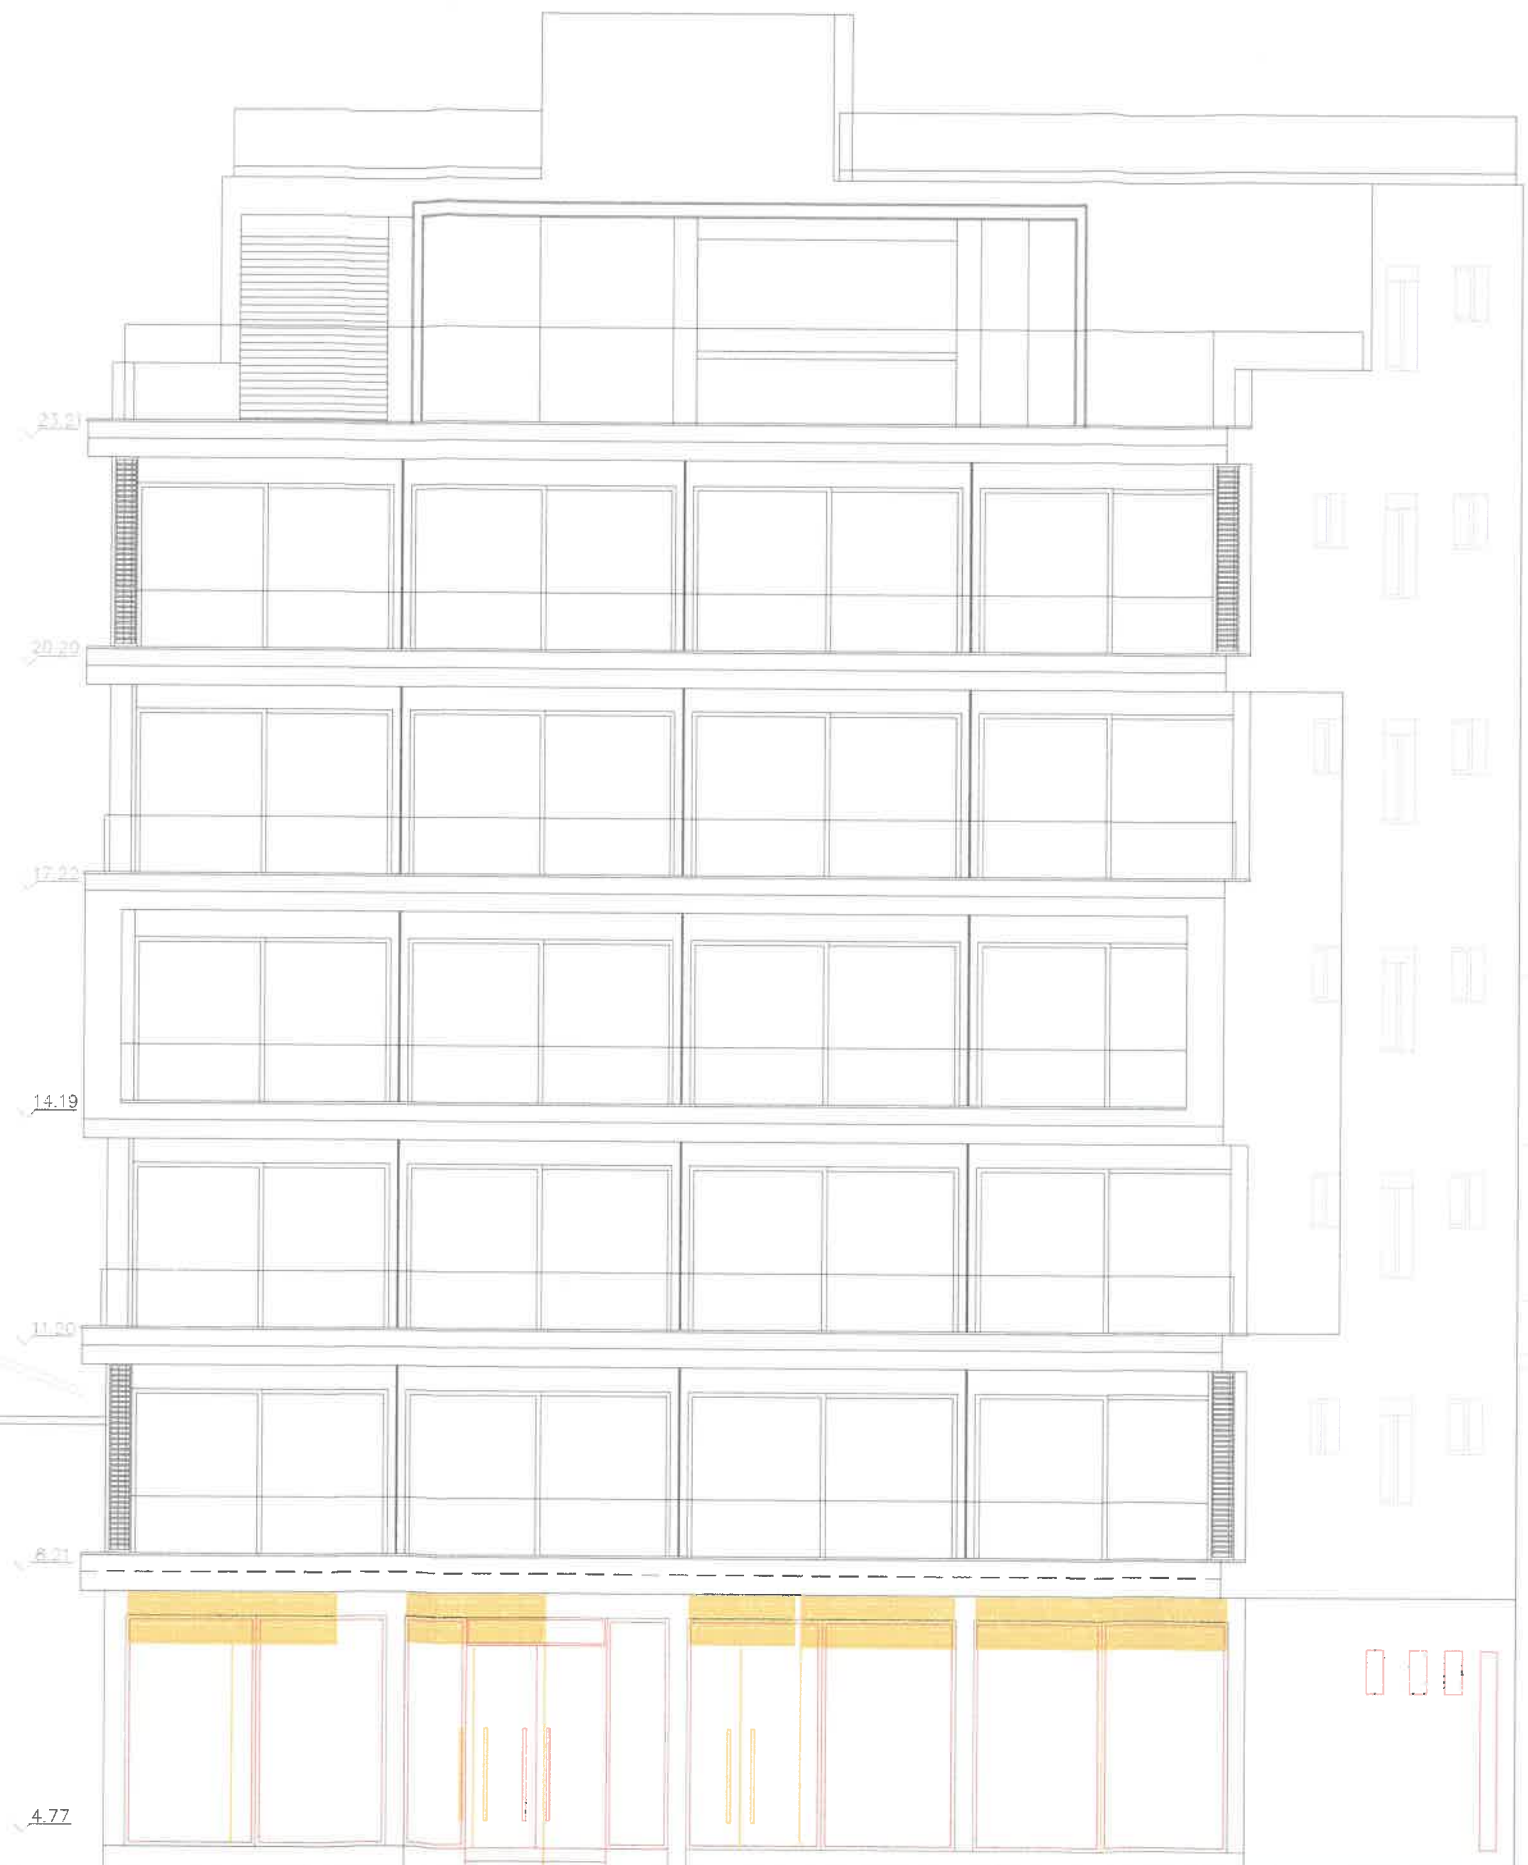


29.00
28.00
27.00
26.00
25.00
24.00
23.00
22.00
21.00
20.00
19.00
18.00
17.00
16.00
15.00
14.00
13.00
12.00
11.00
10.00
9.00
8.00
7.00
6.00
5.00
4.00
3.00

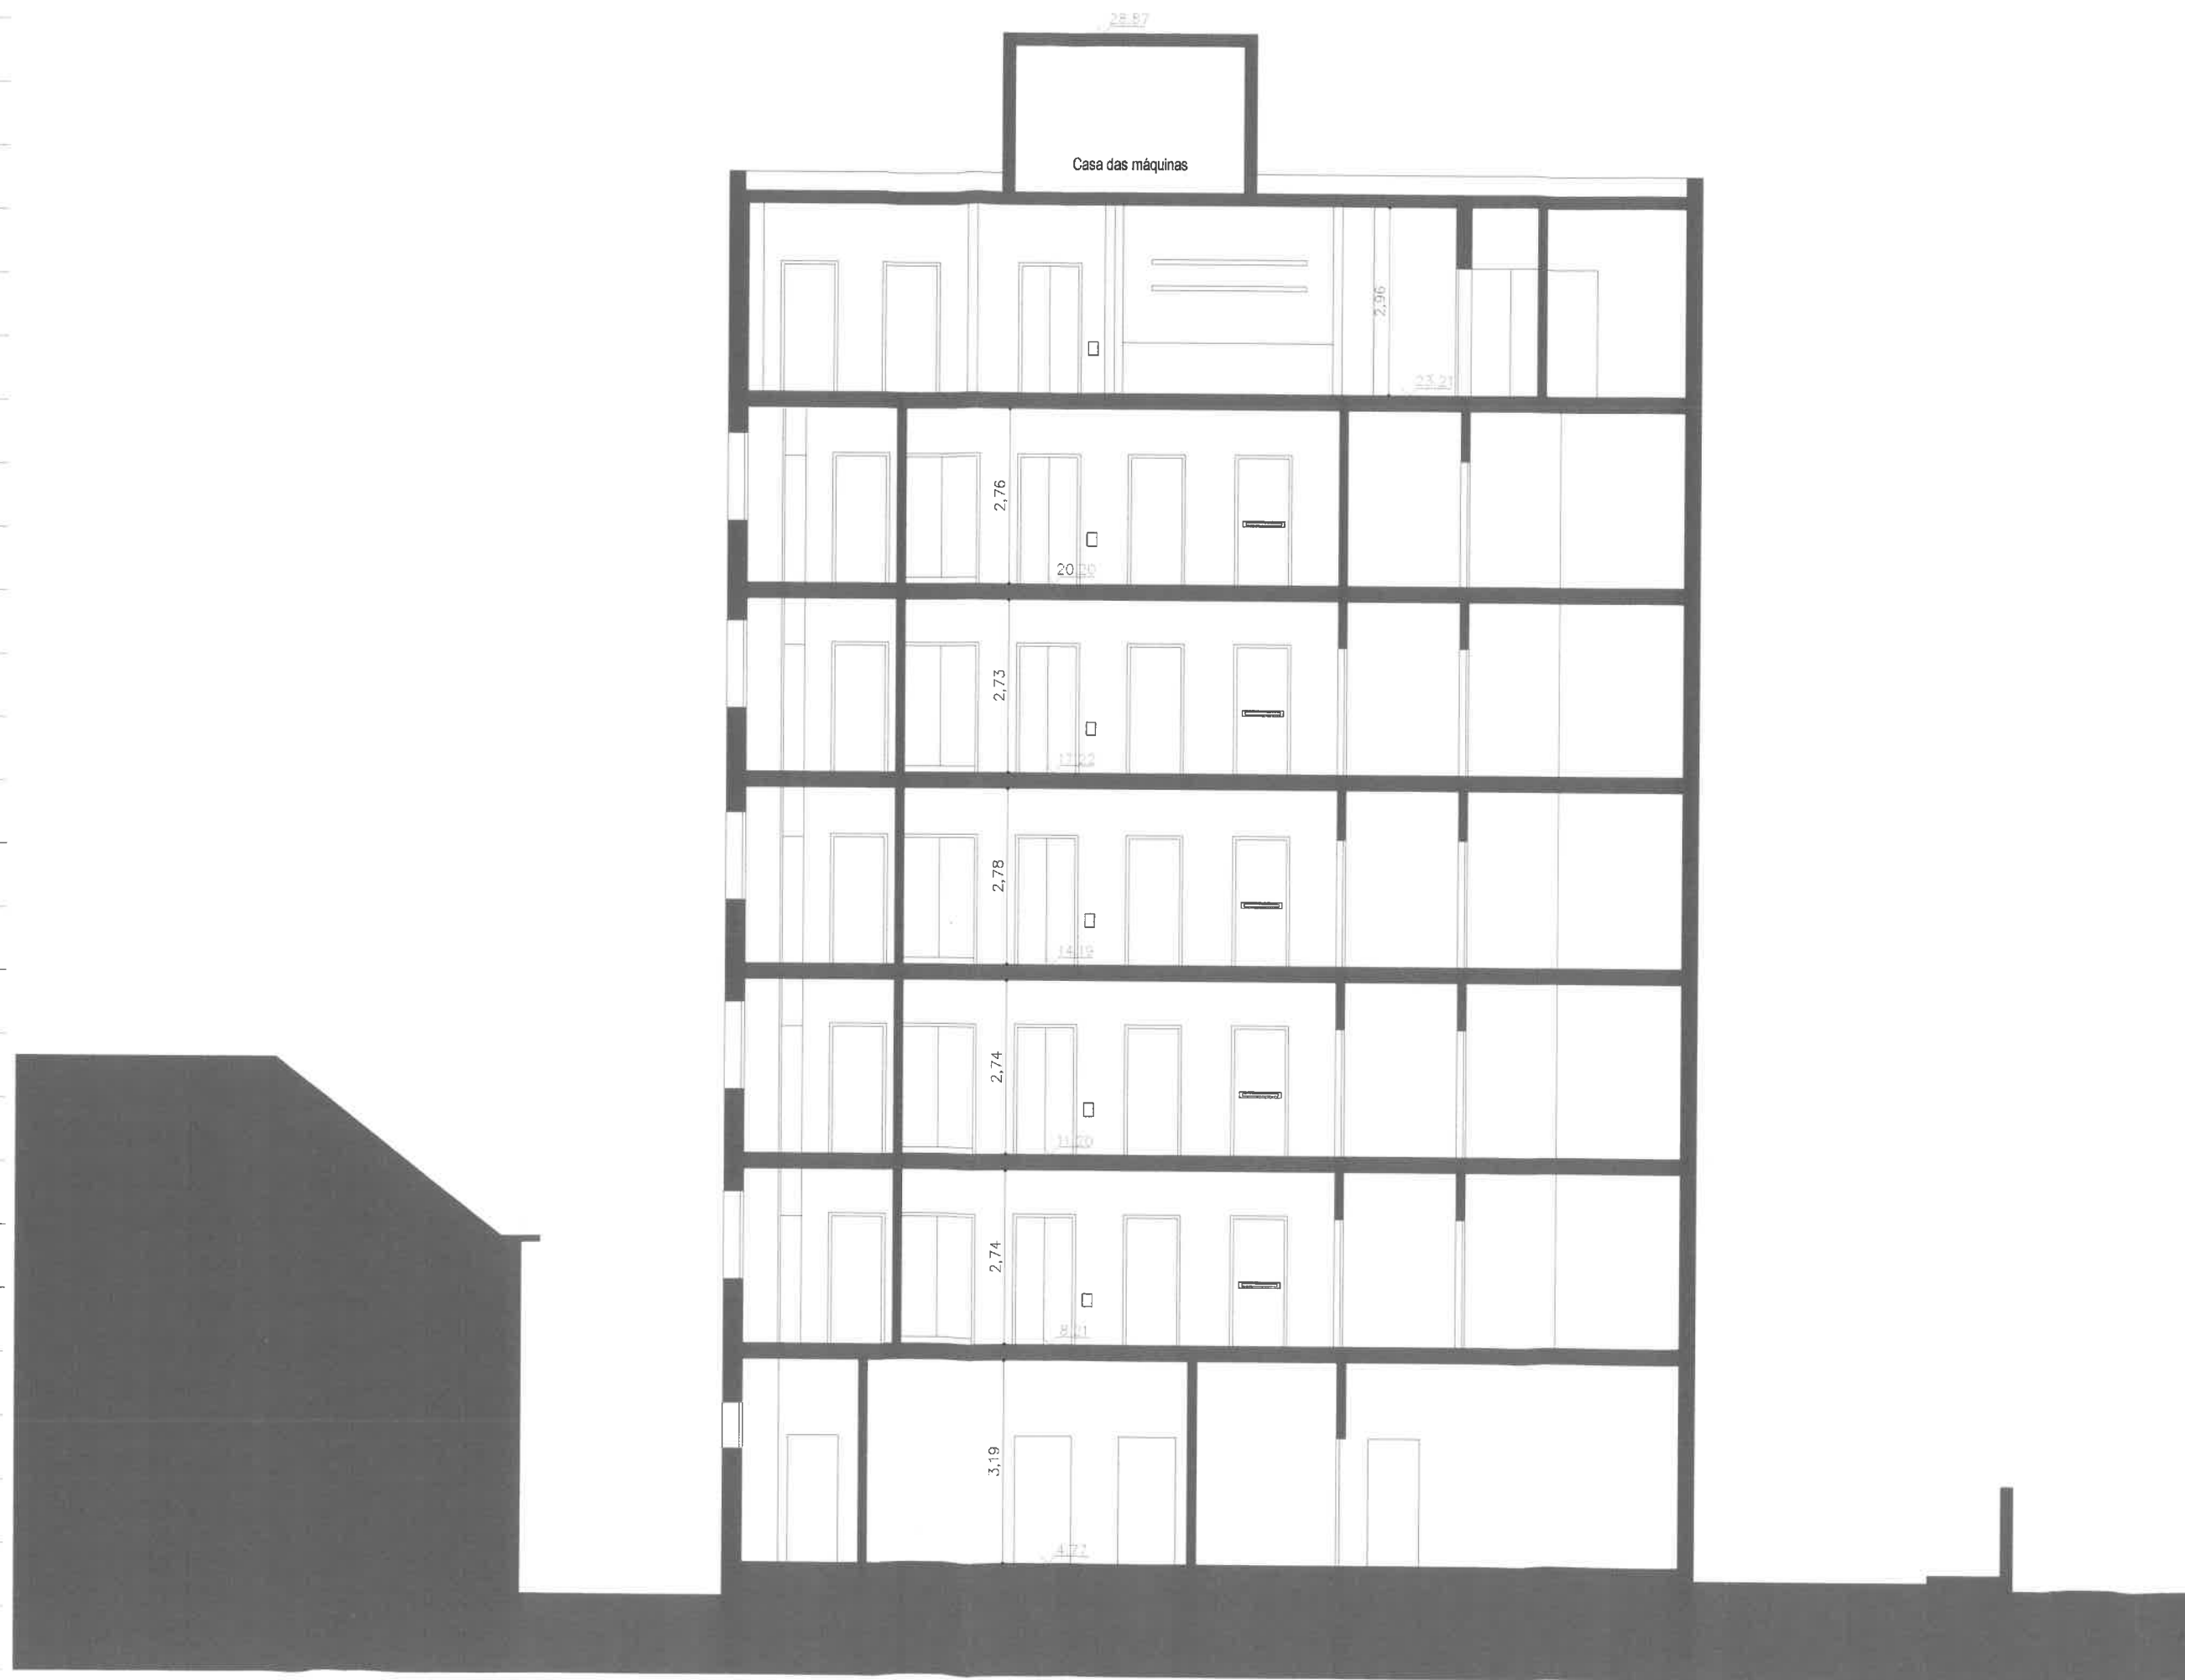


CORTE A-A

29.00
28.00
27.00
26.00
25.00
24.00
23.00
22.00
21.00
20.00
19.00
18.00
17.00
16.00
15.00
14.00
13.00
12.00
11.00
10.00
9.00
8.00
7.00
6.00
5.00
4.00
3.00

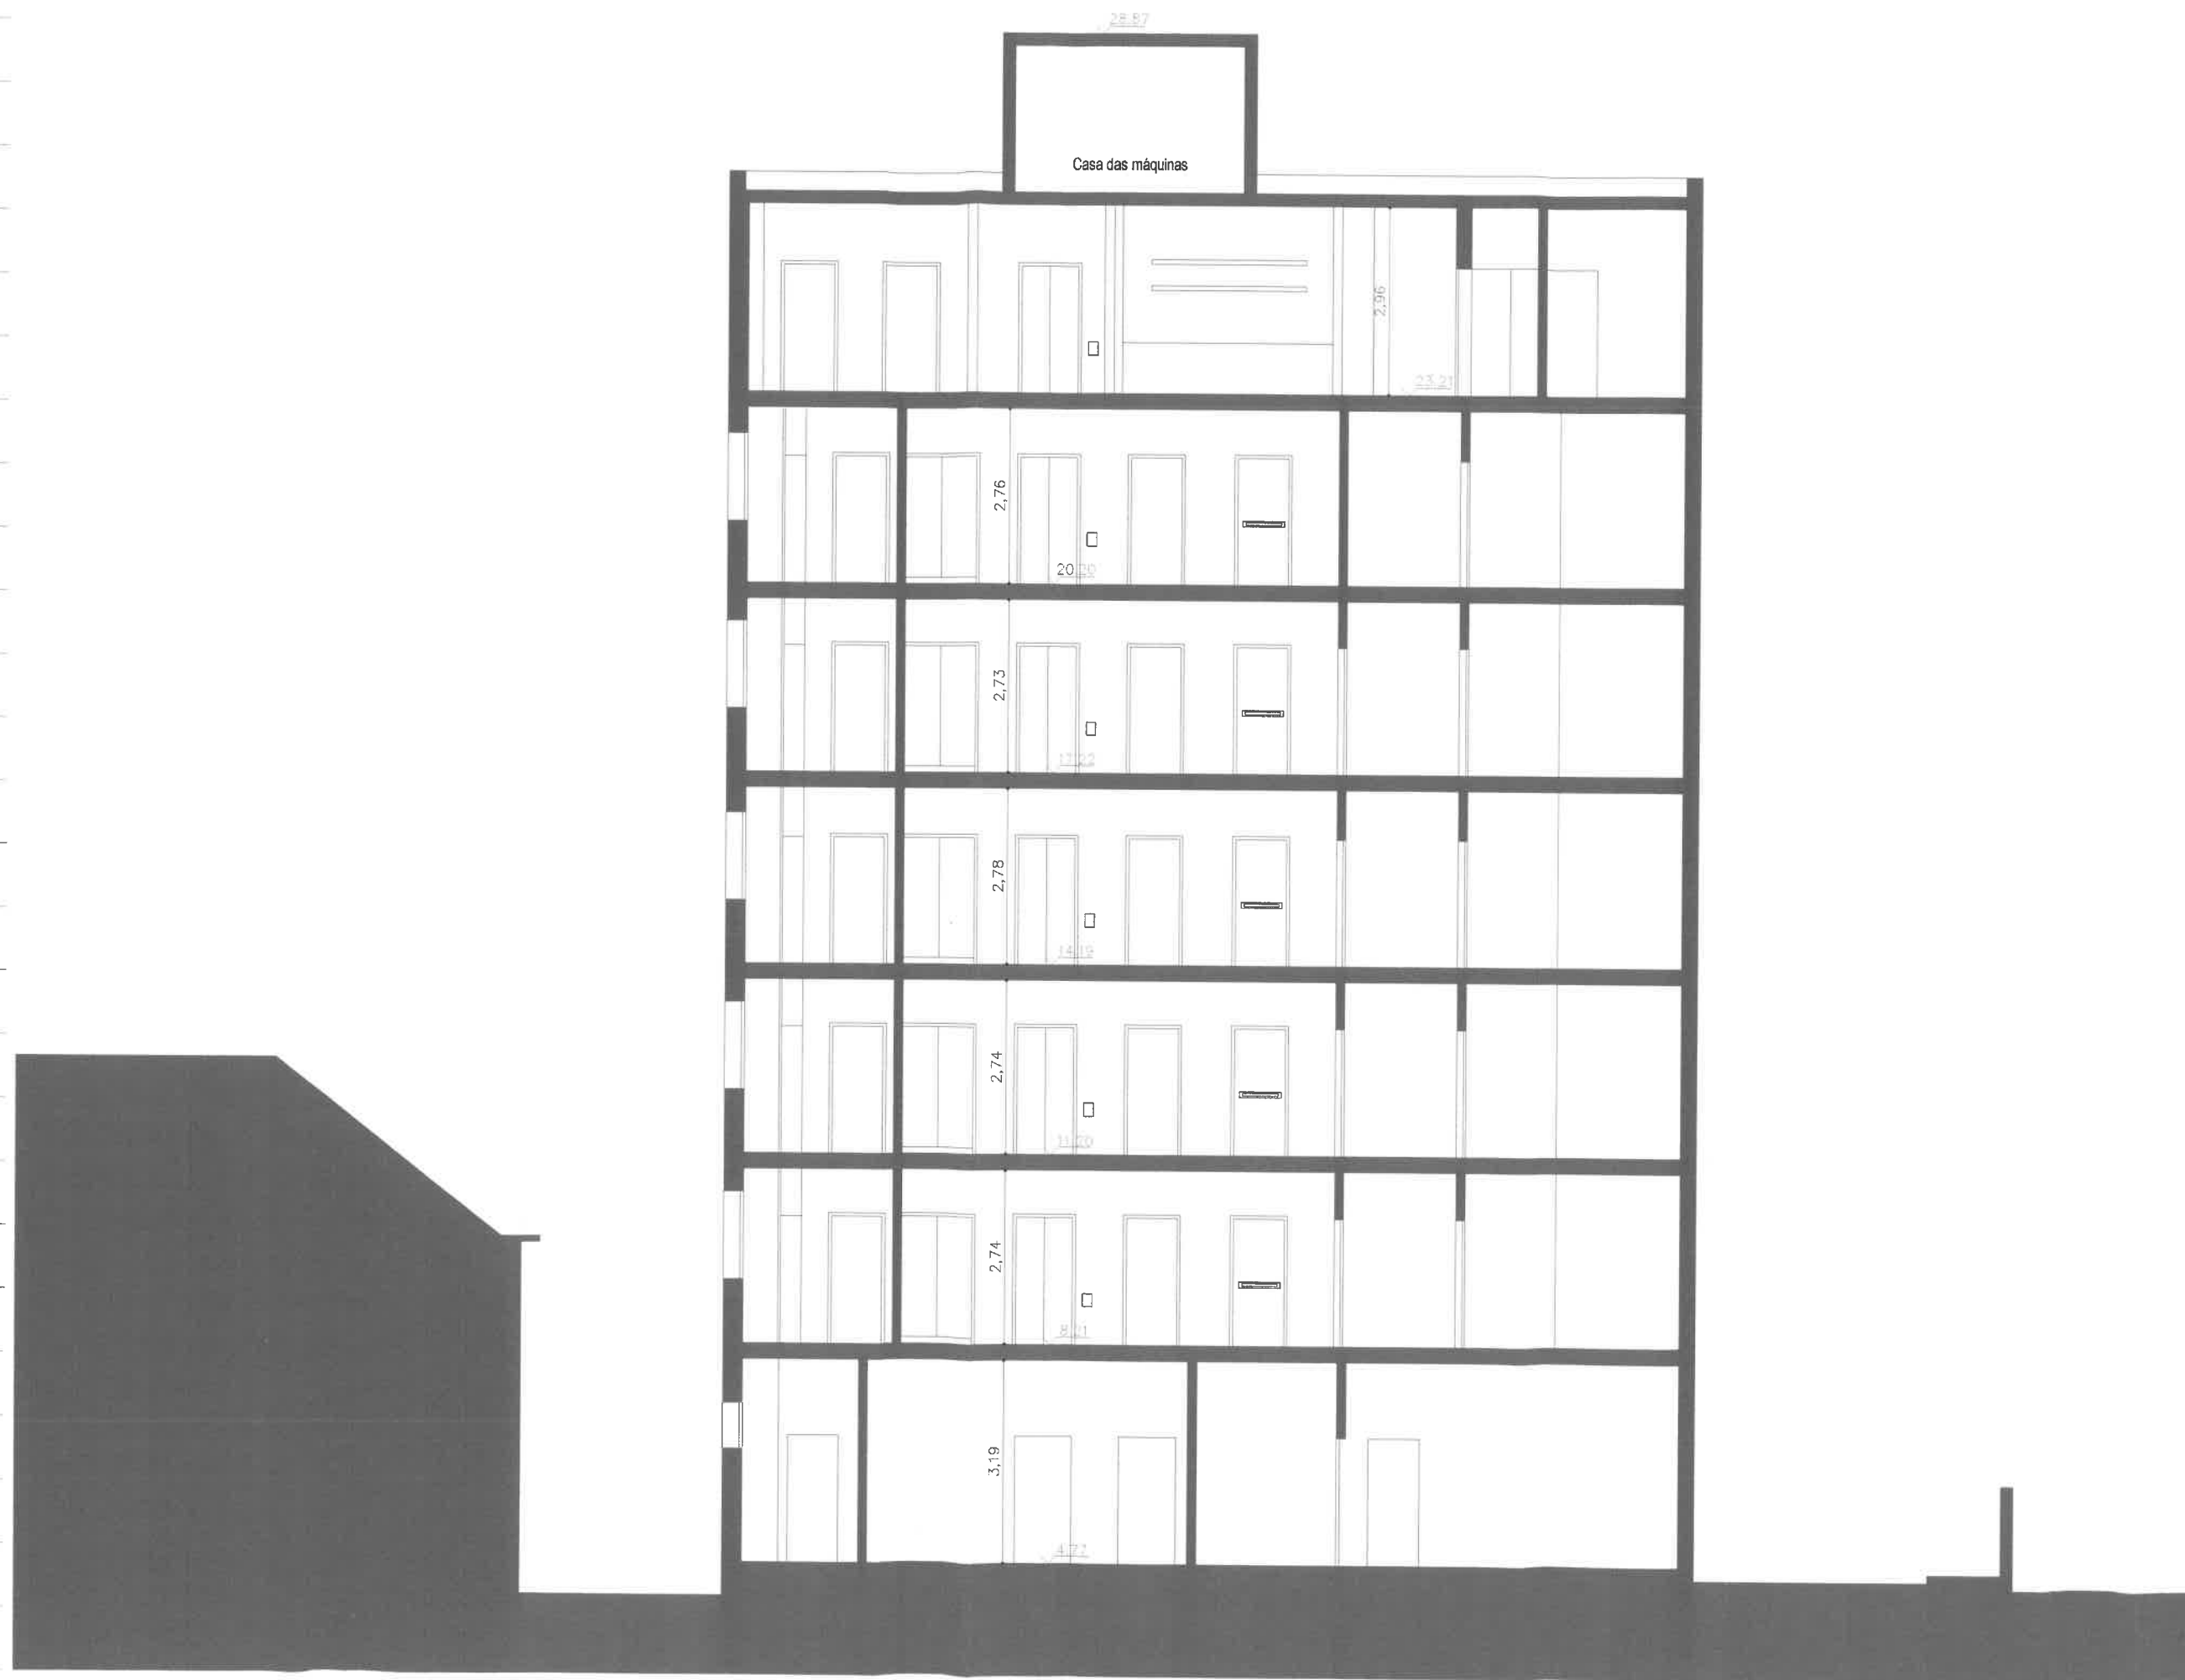


CORTE A-A

29.00
28.00
27.00
26.00
25.00
24.00
23.00
22.00
21.00
20.00
19.00
18.00
17.00
16.00
15.00
14.00
13.00
12.00
11.00
10.00
9.00
8.00
7.00
6.00
5.00
4.00
3.00

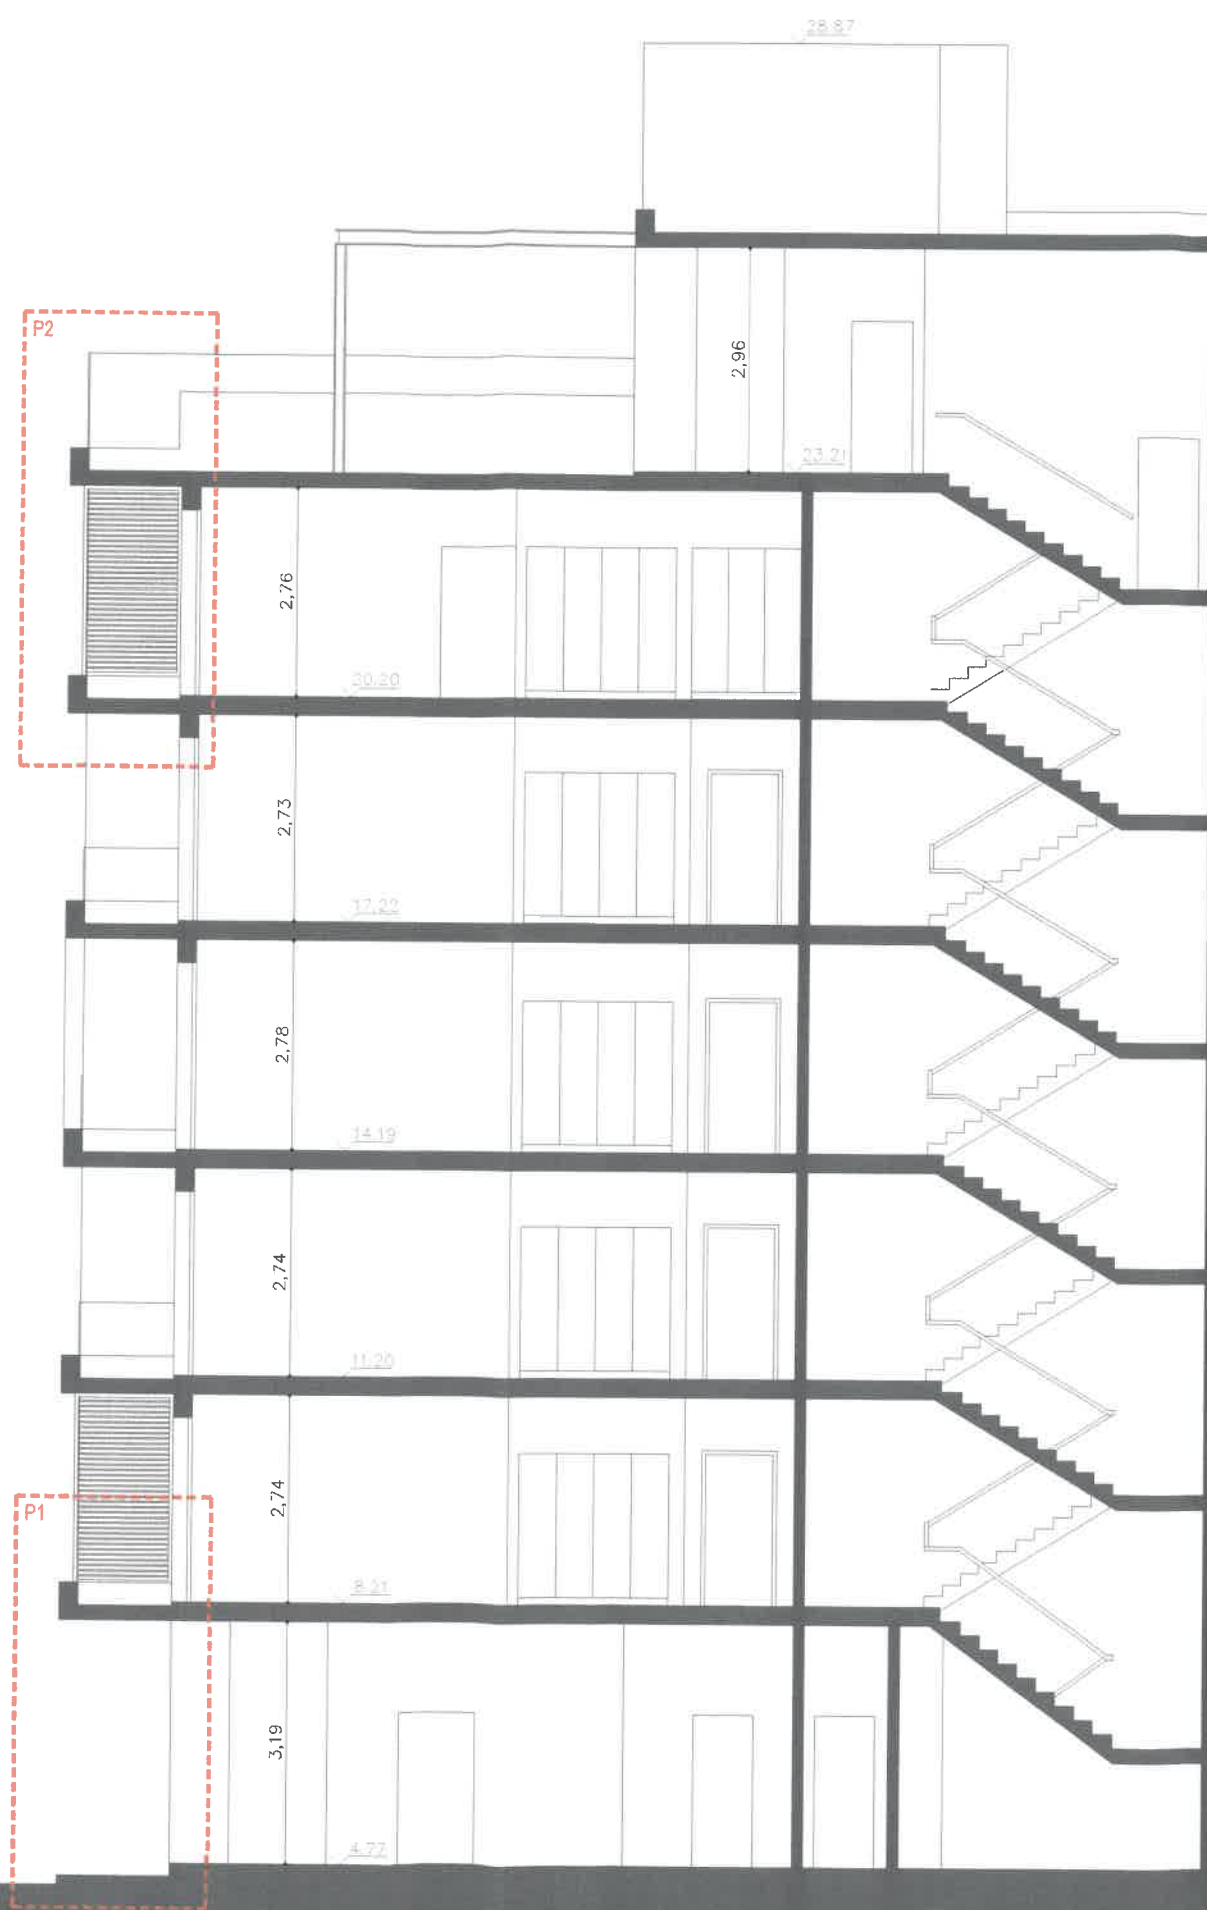

CORTE B-B


29.00
28.00
27.00
26.00
25.00
24.00
23.00
22.00
21.00
20.00
19.00
18.00
17.00
16.00
15.00
14.00
13.00
12.00
11.00
10.00
9.00
8.00
7.00
6.00
5.00
4.00
3.00

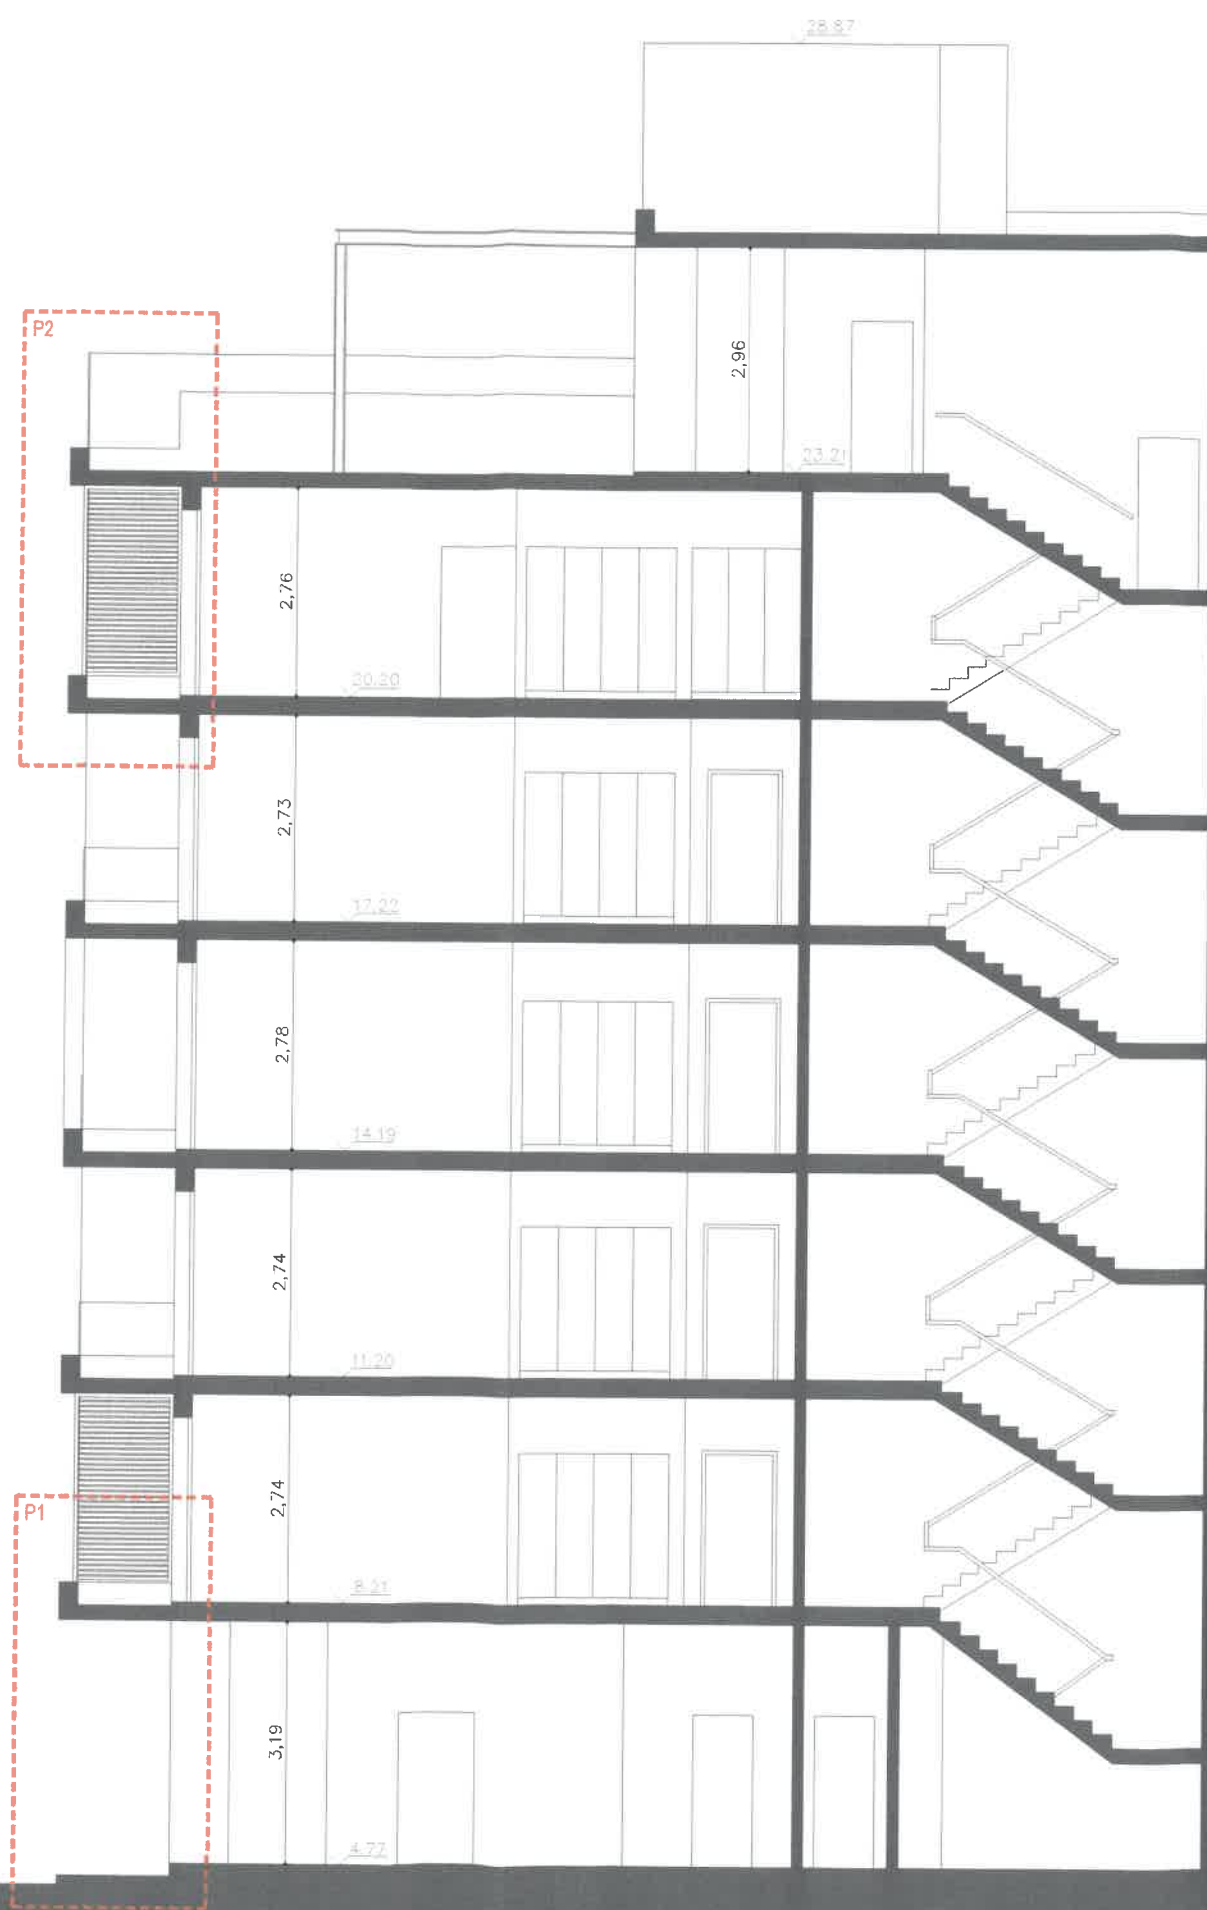



CORTE B-B





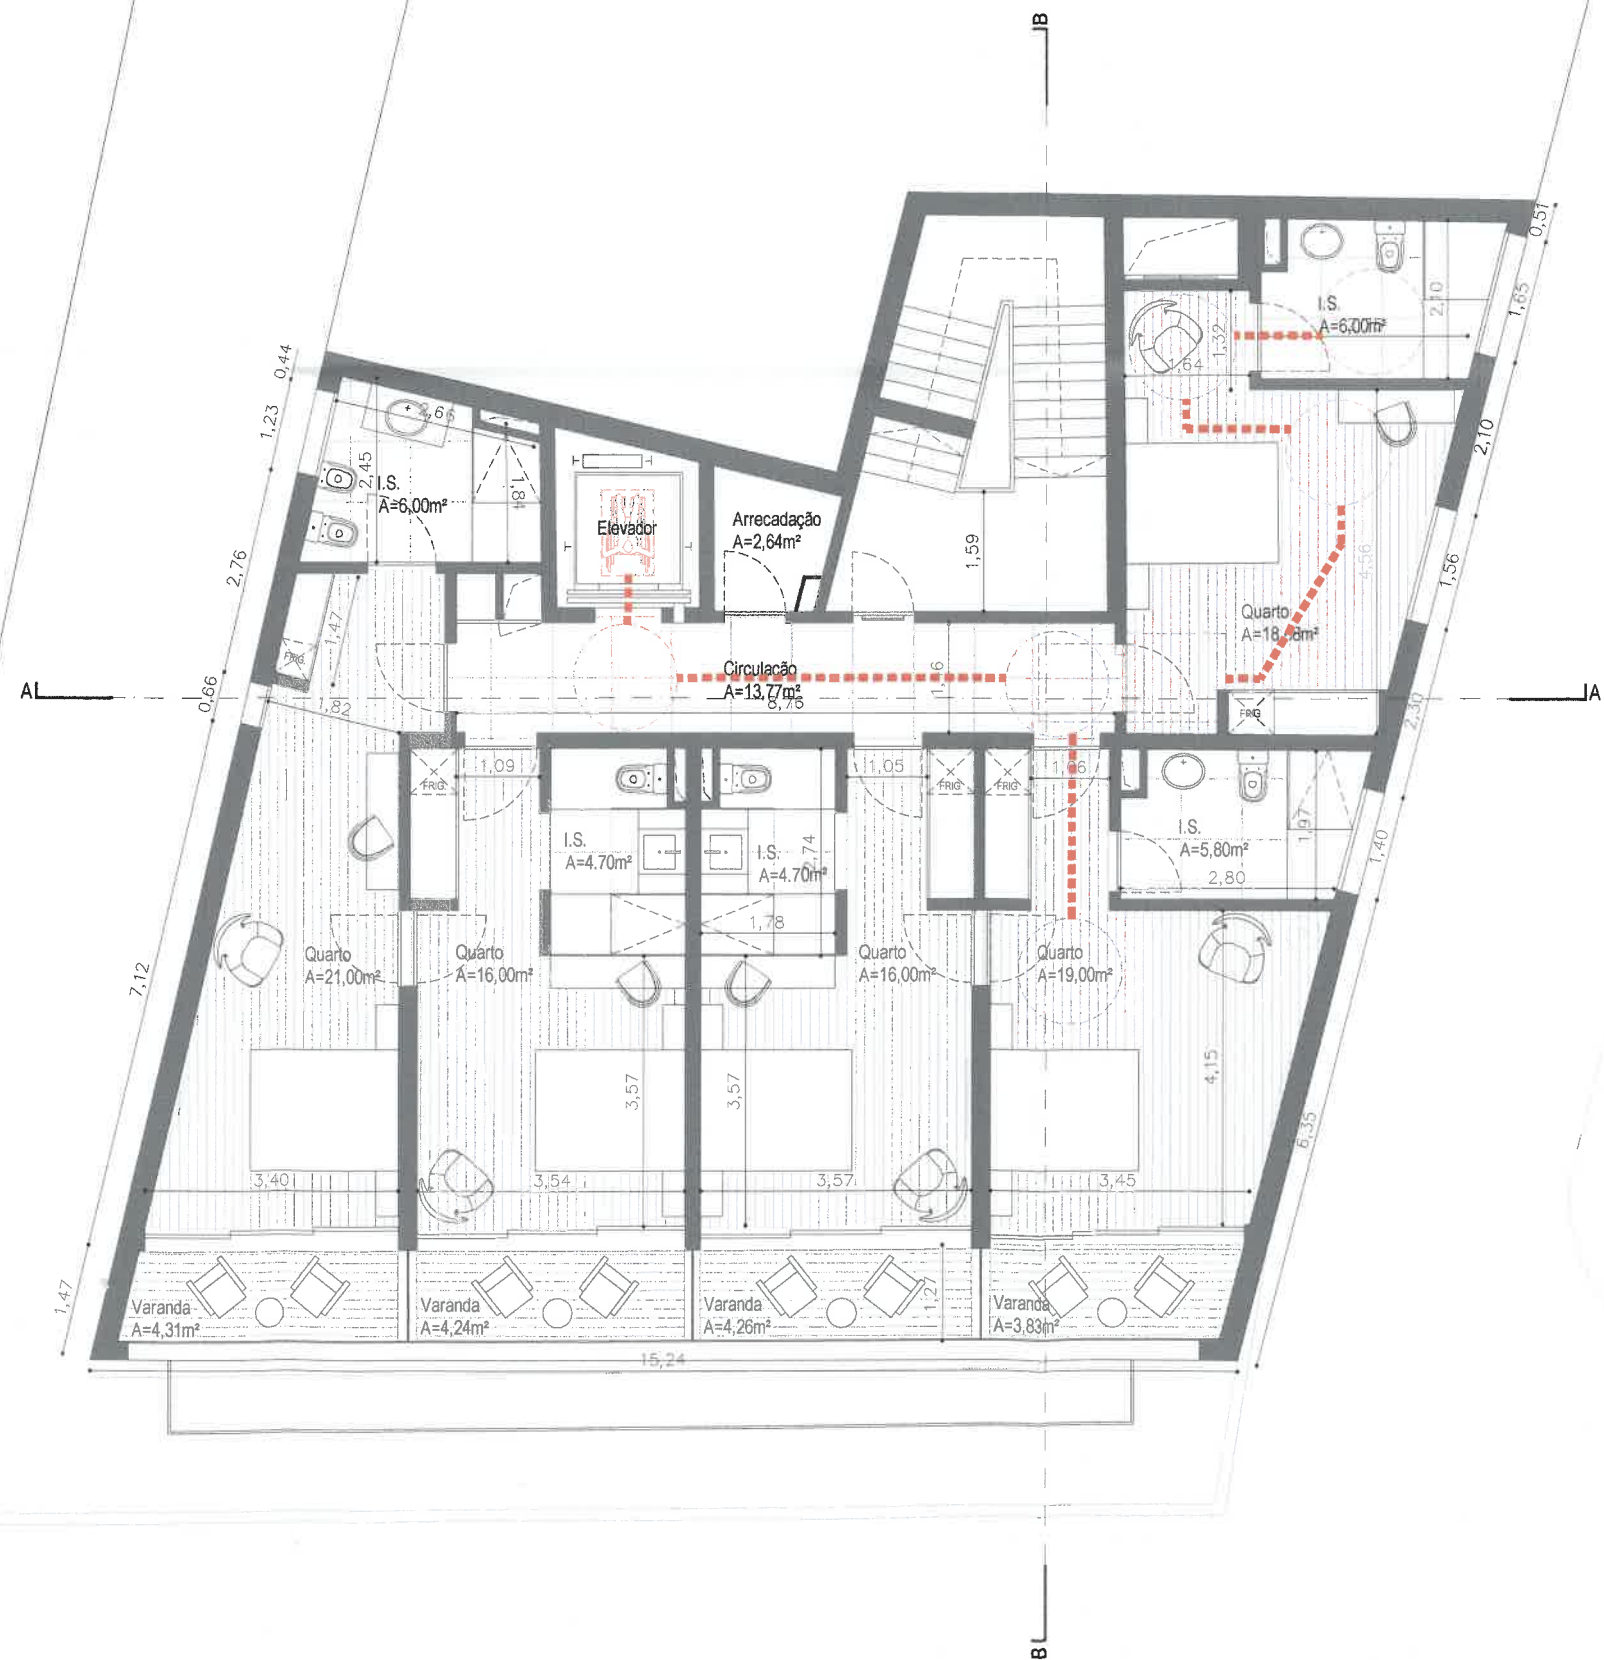

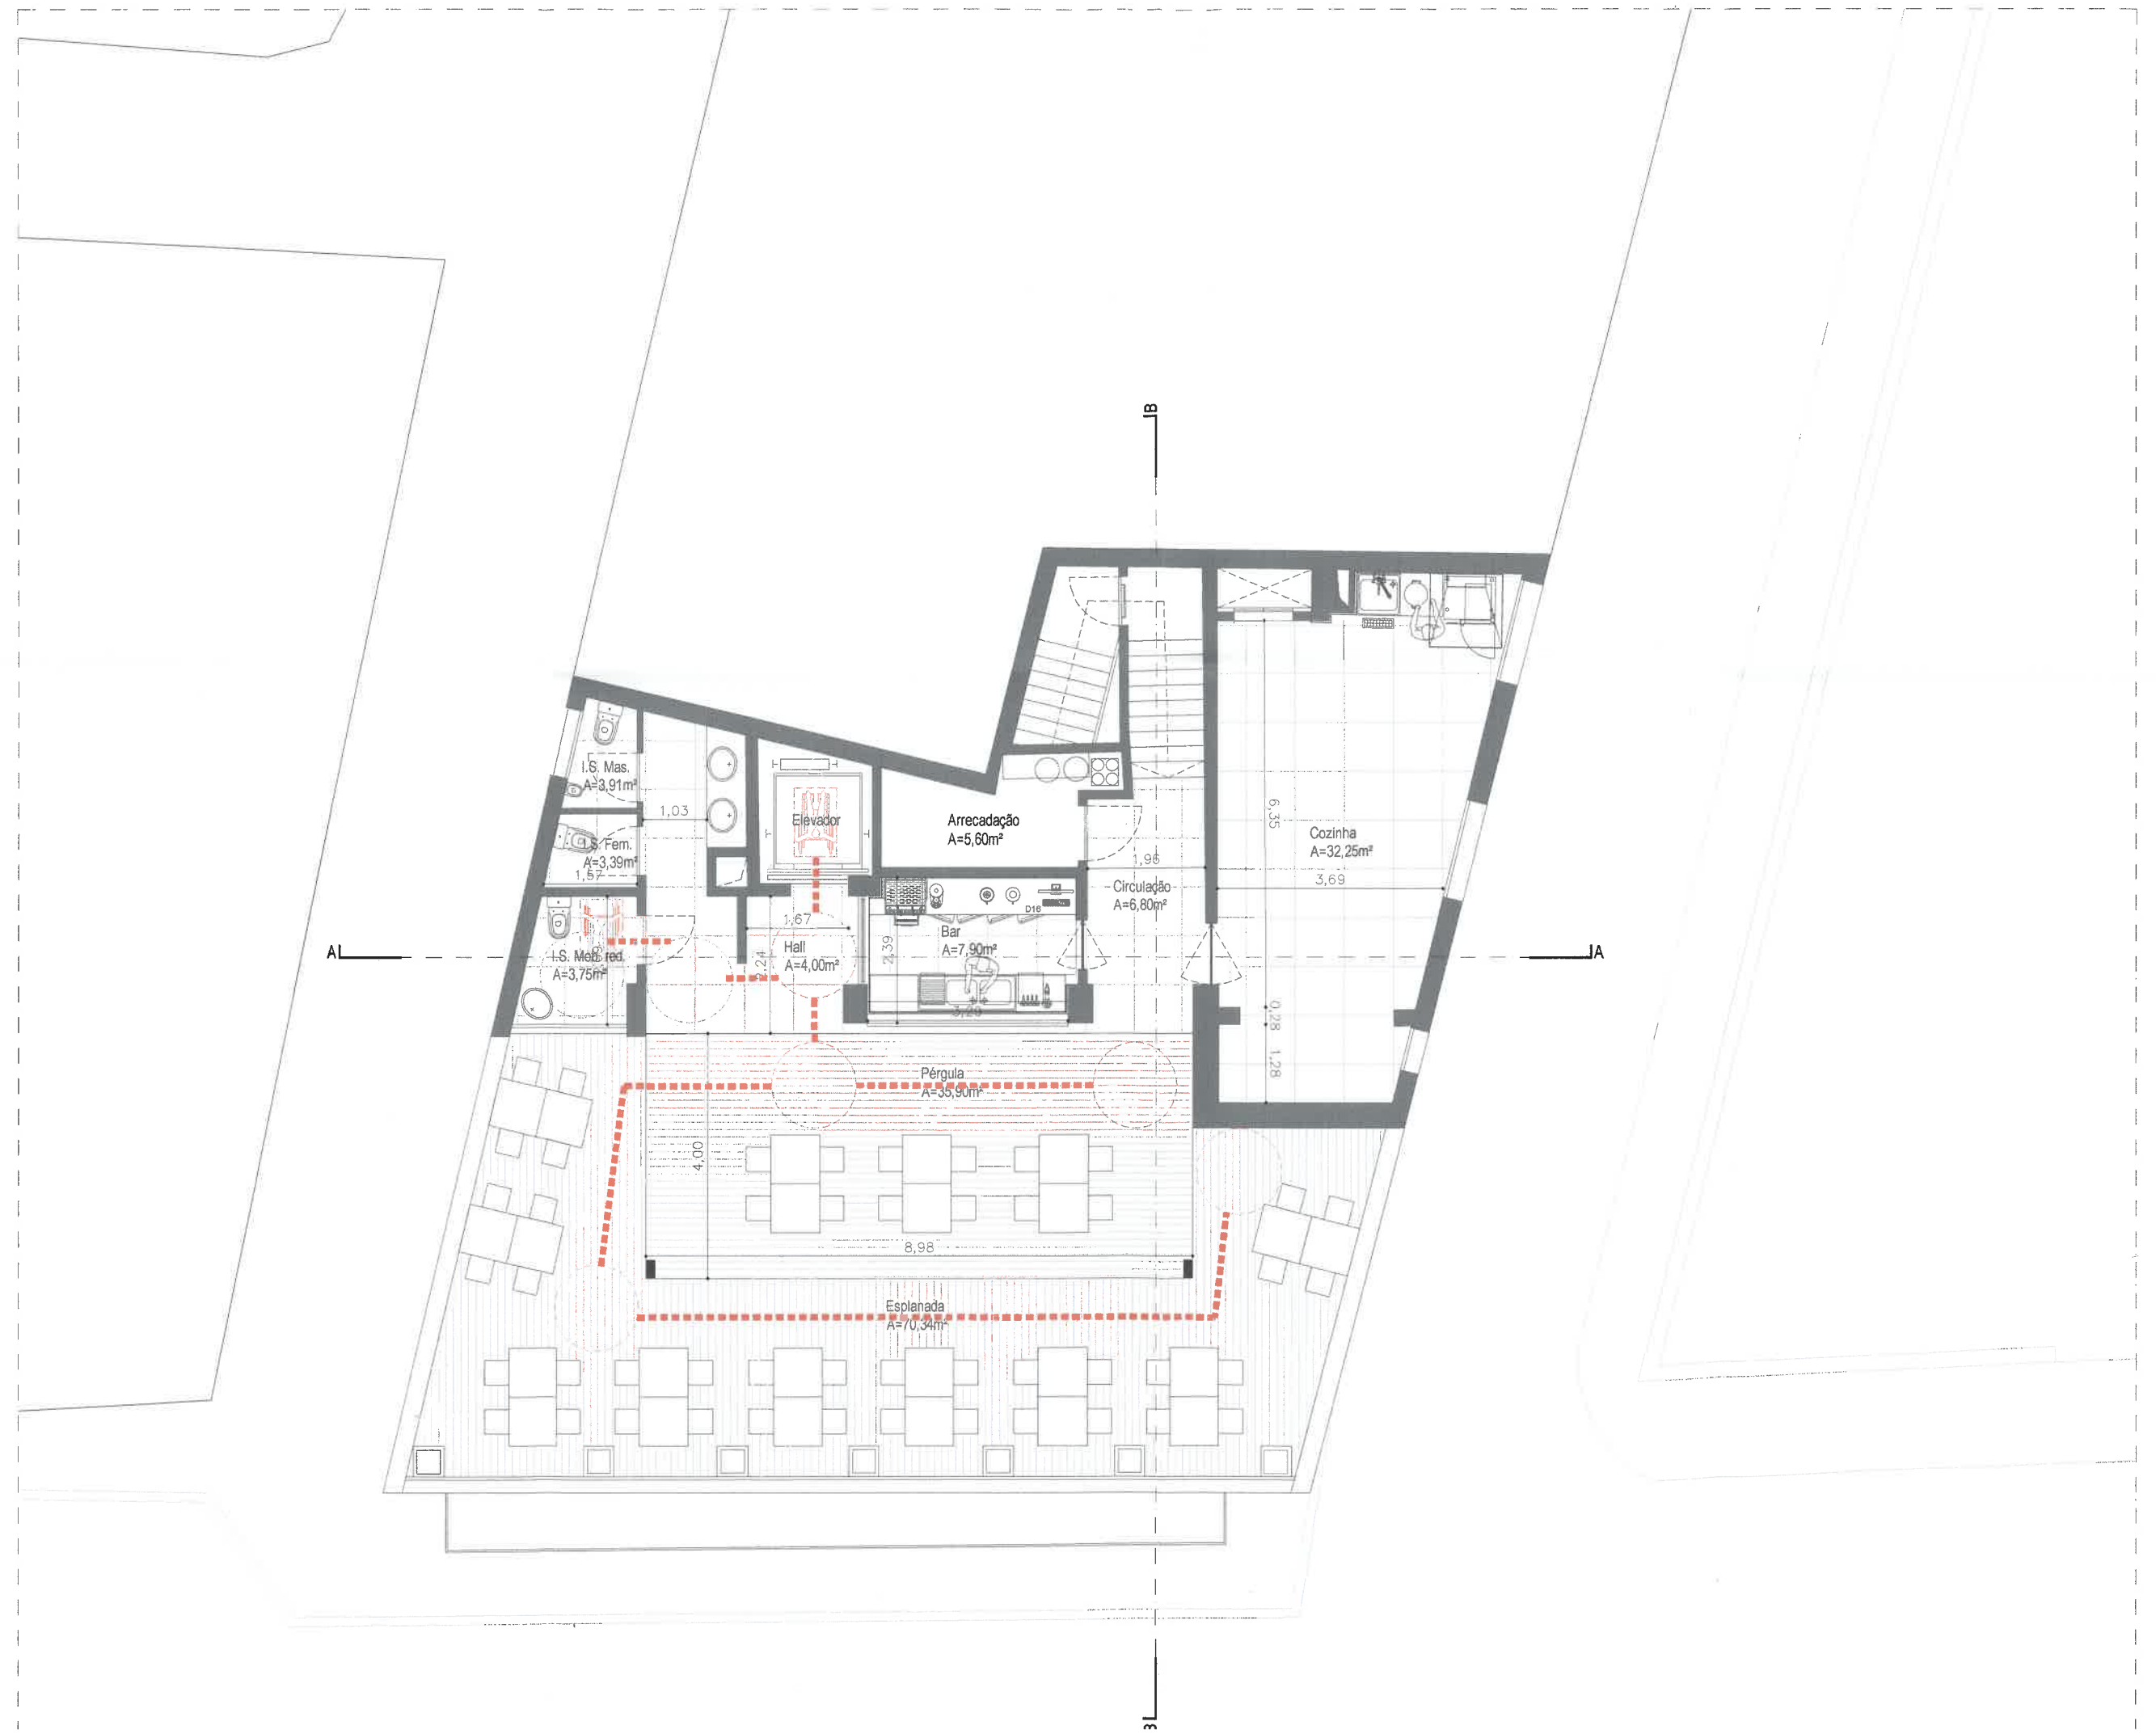

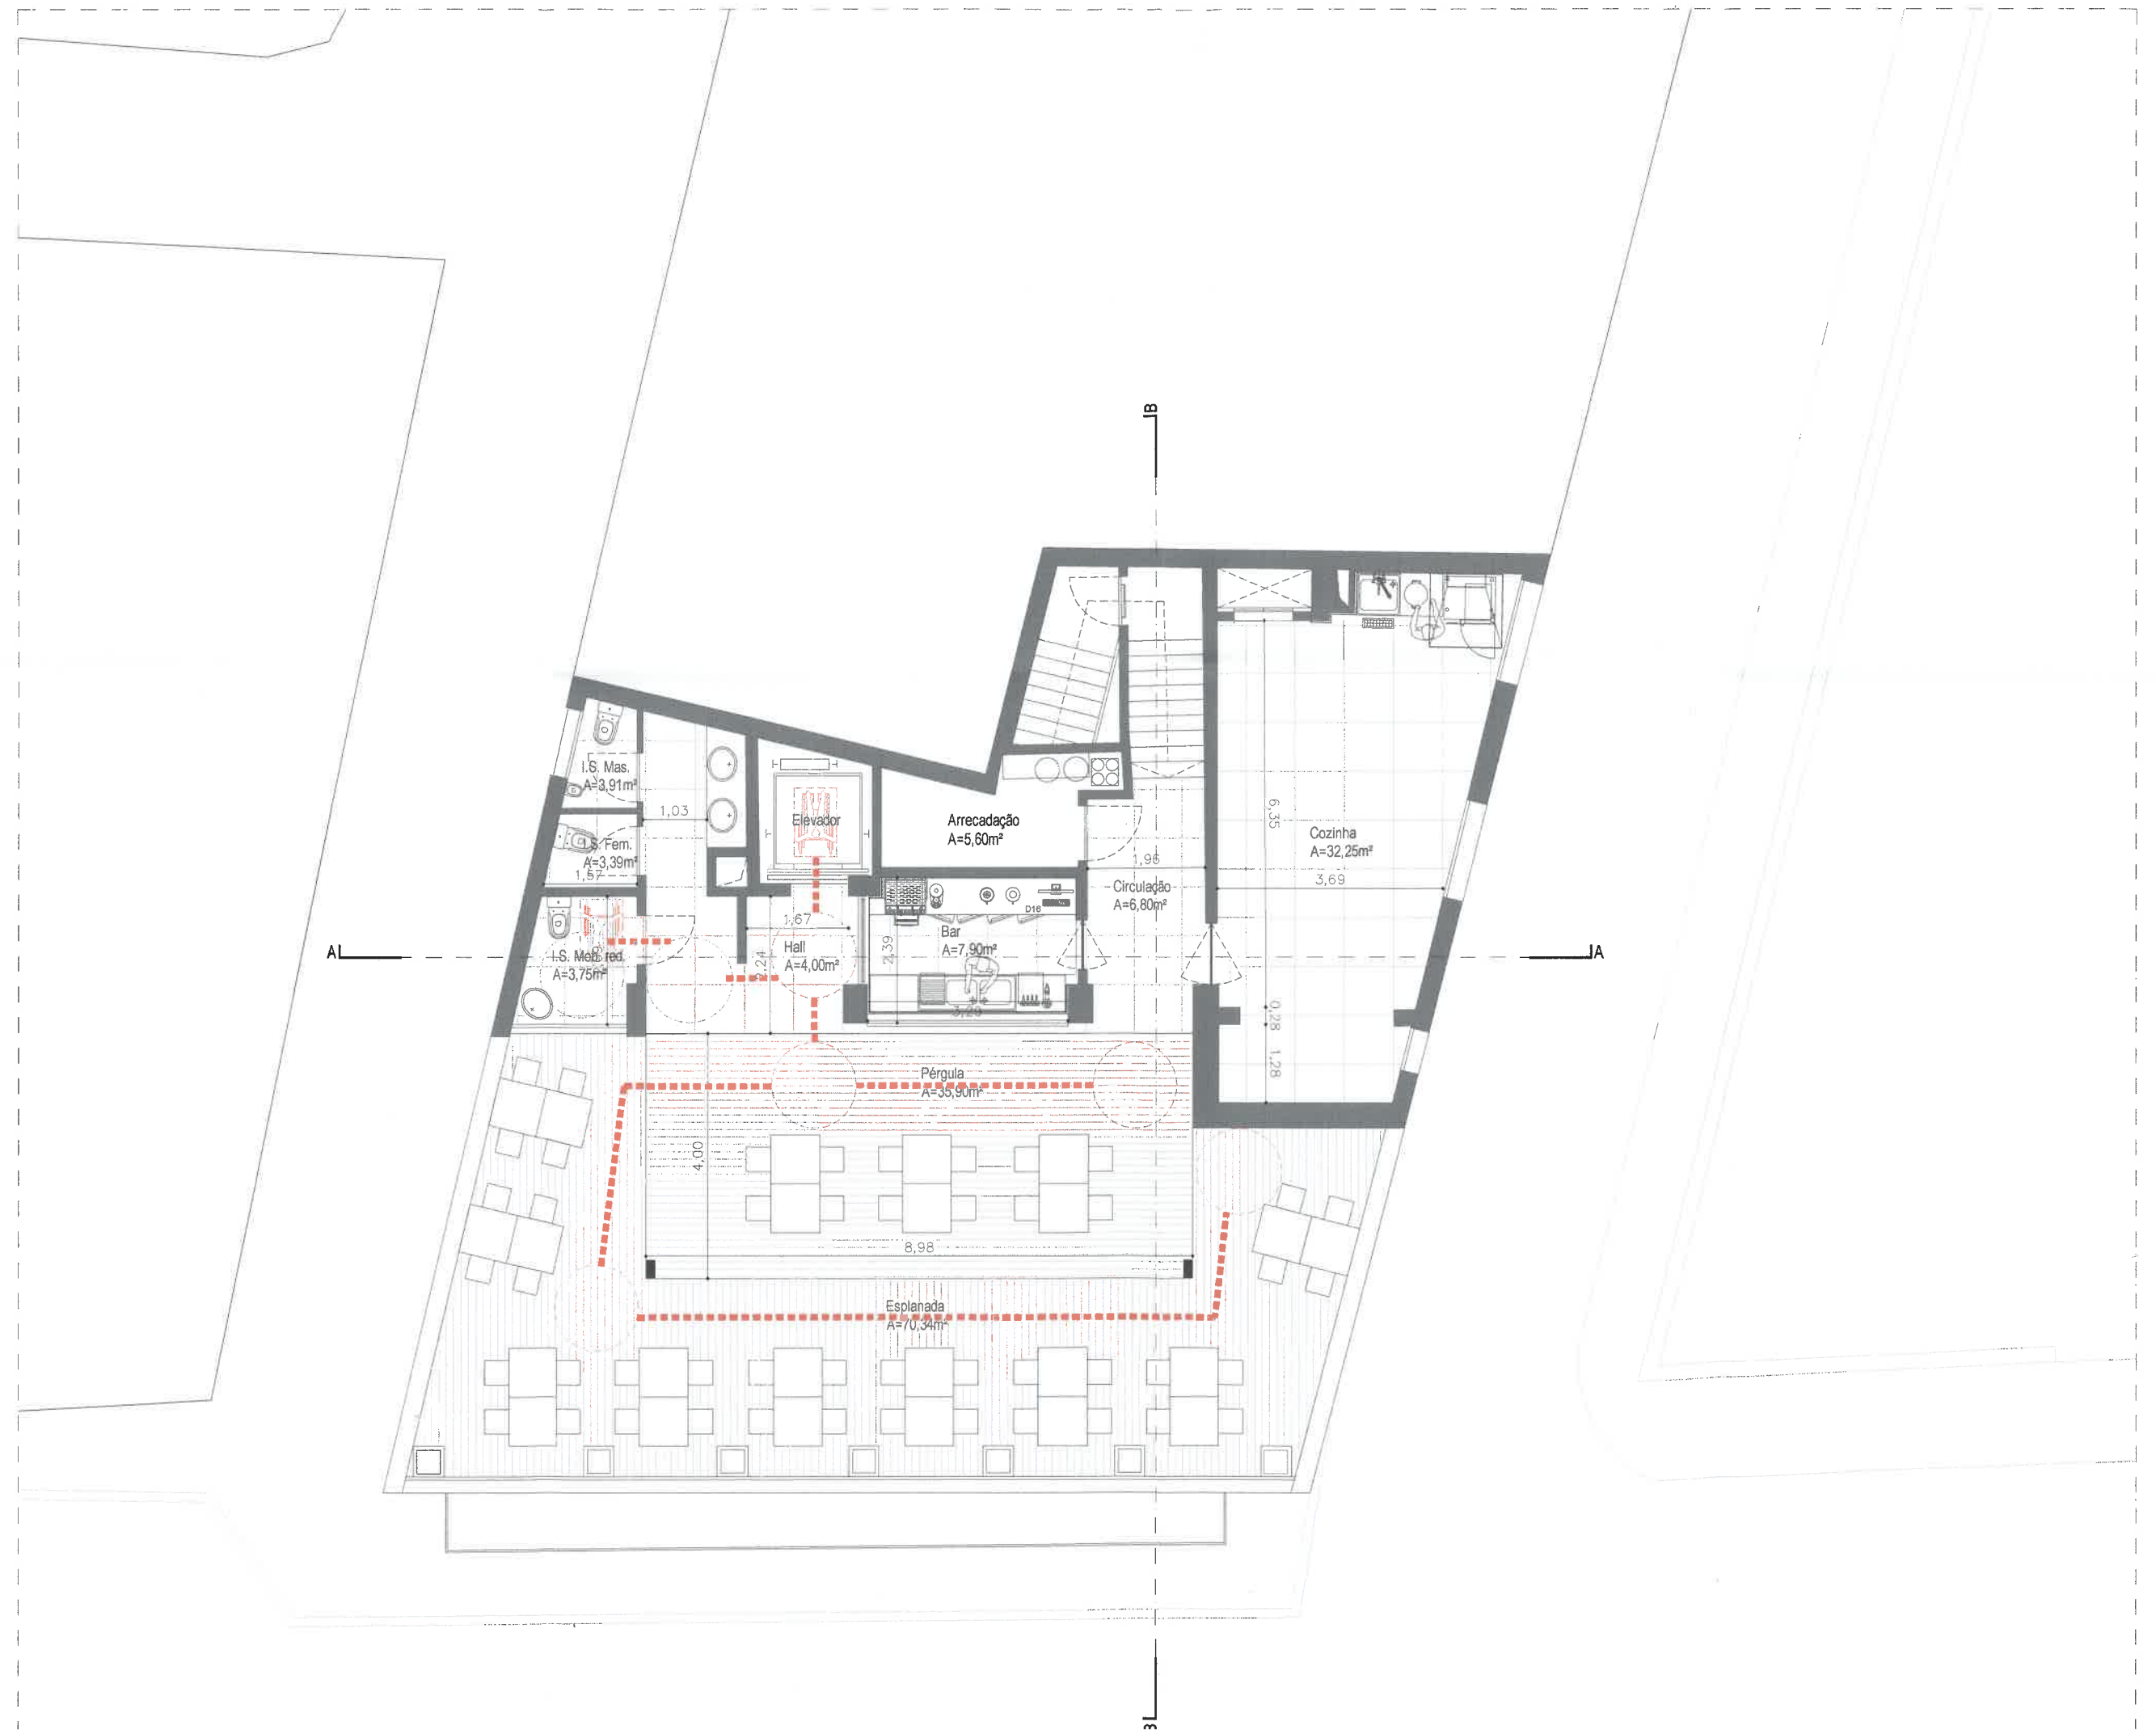


29.00
28.00
27.00
26.00
25.00
24.00
23.00
22.00
21.00
20.00
19.00
18.00
17.00
16.00
15.00
14.00
13.00
12.00
11.00
10.00
9.00
8.00
7.00
6.00
5.00
4.00
3.00

ALÇADO POENTE



29.00
28.00
27.00
26.00
25.00
24.00
23.00
22.00
21.00
20.00
19.00
18.00
17.00
16.00
15.00
14.00
13.00
12.00
11.00
10.00
9.00
8.00
7.00
6.00
5.00
4.00
3.00

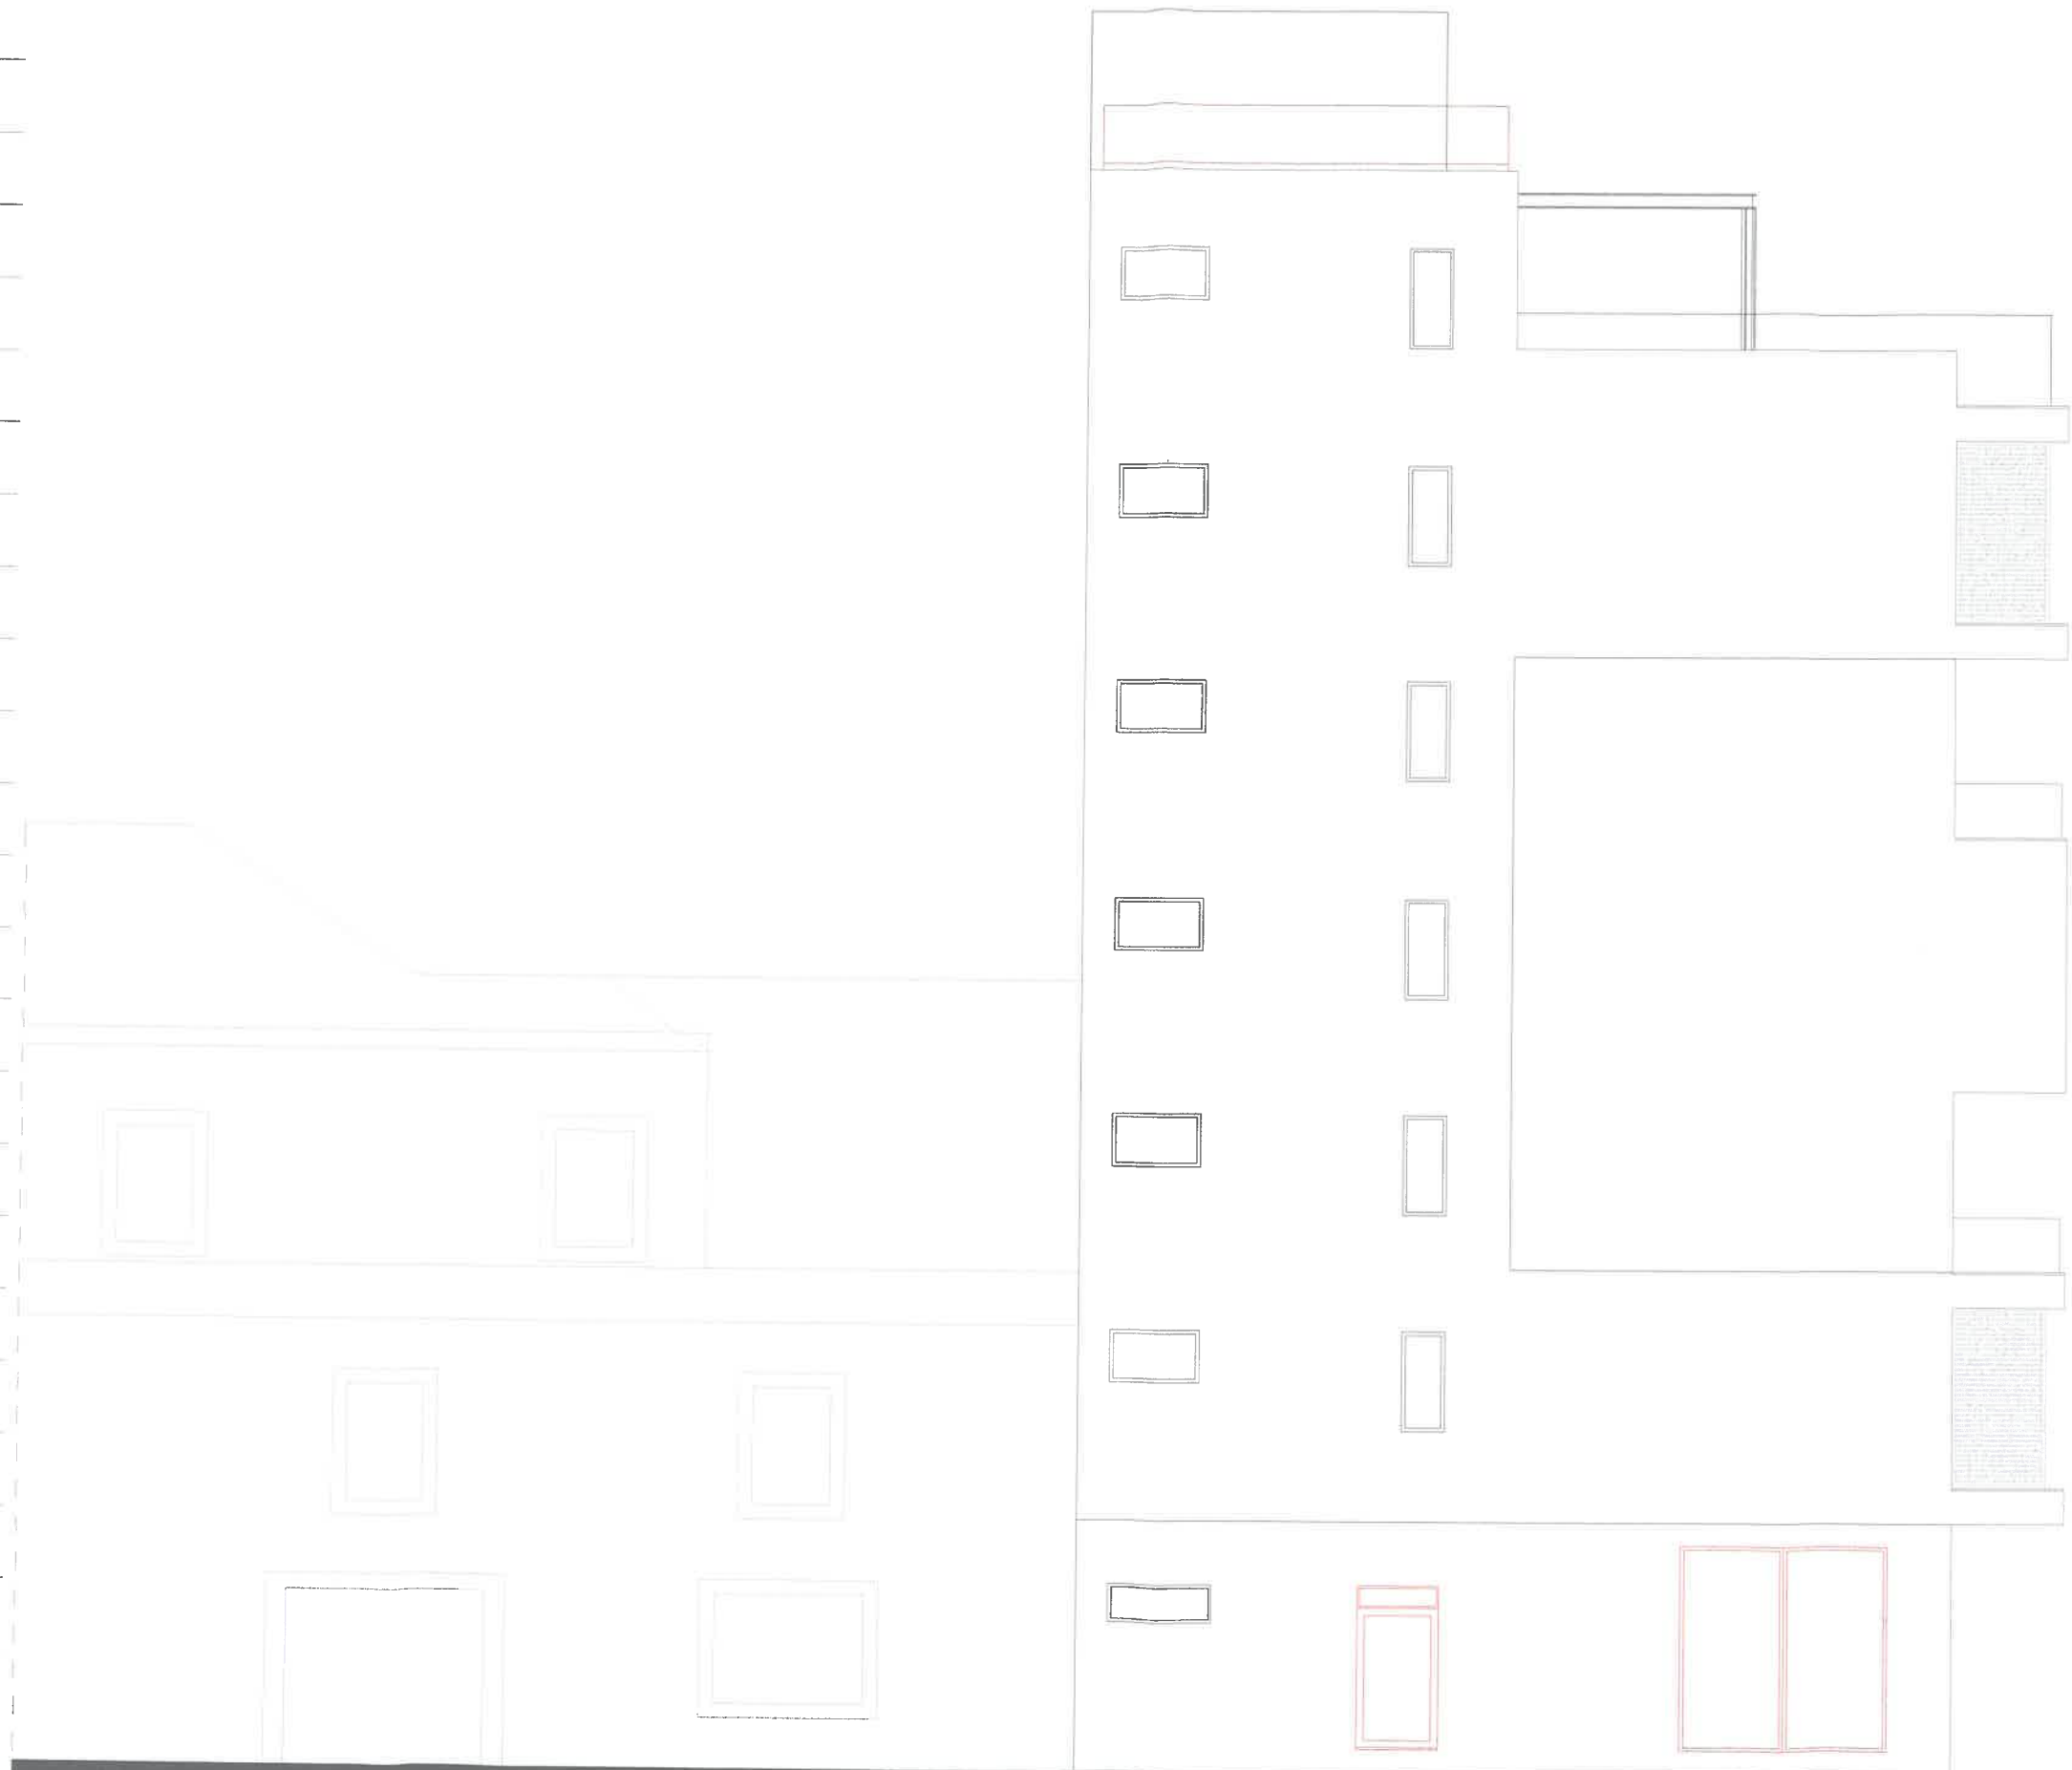

ALÇADO POENTE